


SECTION VIEW

CHANNEL RUNG


NOTE:-
MATERIAL HDG 2mm
Rung Spacing 250mm ALL flange 32 mm
Hot Dip Galvnaiztion 85 M without Epoxy
MIG WELDING
Cover Height 12mm


COVER

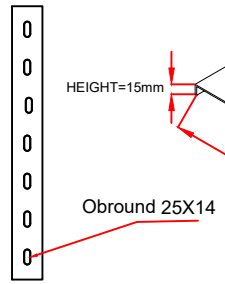


Obround 25X14

Rungs

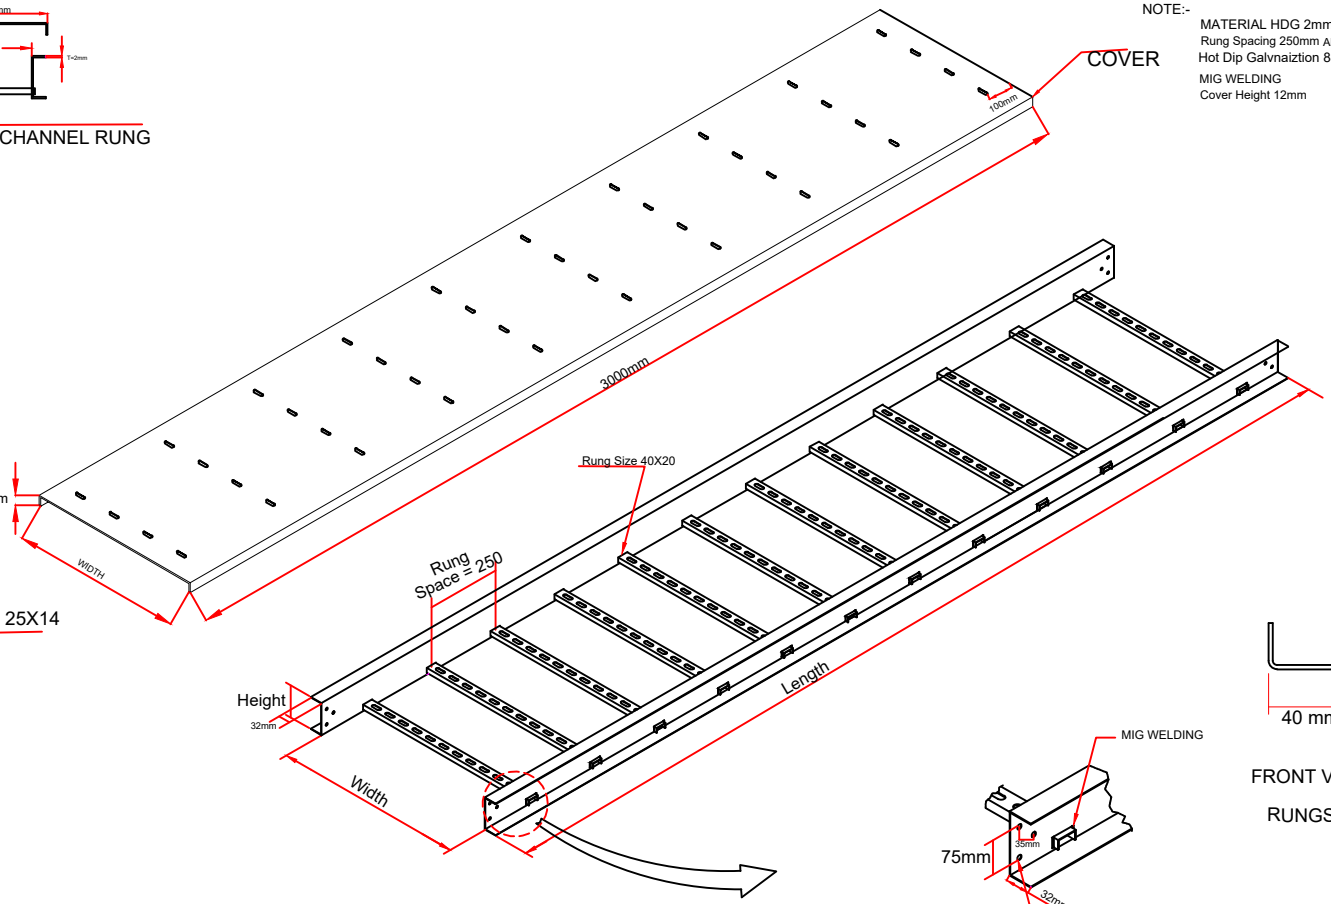

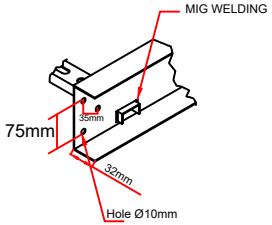

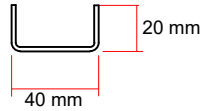

FRONT VIEW

RUNGS

CABLE LADDER STRAIGHT LENGTH W/ COVER

SN	DIMENSION TABLE	QTY
1	W=900mm, H=100mm, T=2mm & L=3000mm W/COVER	32
2	W=750mm, H=100mm, T=2mm & L=3000mm W/COVER	169
3	W=600mm, H=100mm, T=2mm & L=3000mm W/COVER	409
4	W=450mm, H=100mm, T=2mm & L=3000mm W/COVER	50
5	W=300mm, H=100mm, T=2mm & L=3000mm W/COVER	470

DRAWN BY	EZELDIN
CHECKED BY	AMIR KHAN
APPROVED BY	NASSER ANANI
DATE	22-07-2026
REF NO. :	
CONSULTANT :	

TITLE: CABLE LADDER STRAIGHT LENGTH W/ COVER

CLIENT: KENT GAD

SEC ITEM NO:

BONN METAL CONS. IND.


BONN GROUP OF COMPANIES
Cable Management Systems

DWRG. NO. :


REV. 01

SHEET NO. :

SCALE:NTS

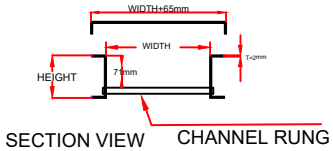


SECTION VIEW CHANNEL RUNG

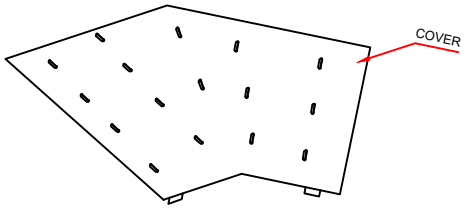


NOTE:-


MATERIAL HDG 2mm ALL flange 32 mm
Hot Dip Galvnaiztion 85 M without Epoxy
MIG WELDING
Cover Height 12mm

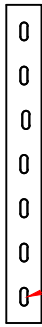

Obround 25X14

Rungs

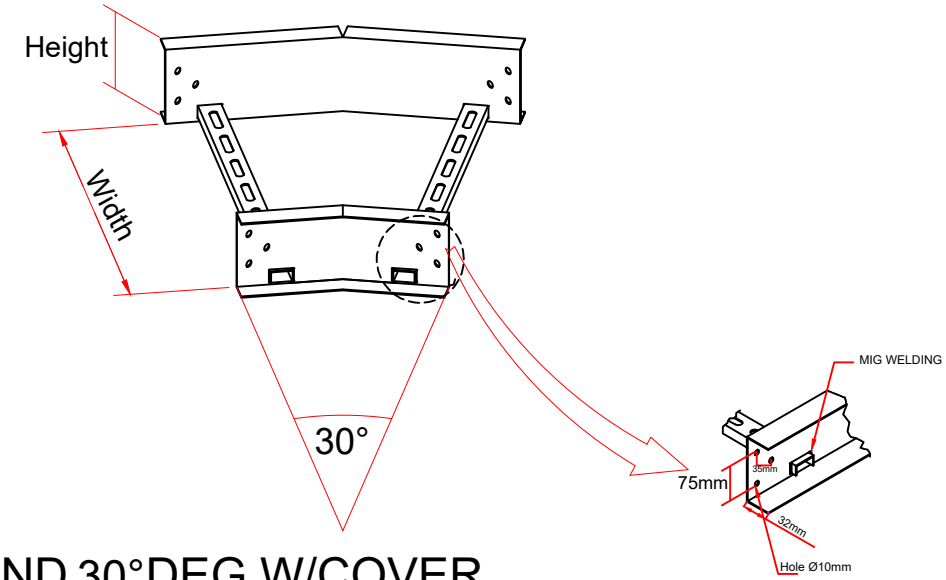

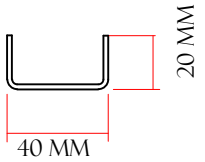

SIDE VIEW

CABLE LADDER BEND 30°DEG W/COVER

SN	DIMENSION TABLE	QTY
6	W=300mm, H =100mm , R= 300mm , T = 2mm , W/COVER	7
7	W=300mm, H =100mm , R= 600mm , T = 2mm , W/COVER	2
8	W=600mm, H =100mm , R= 600mm , T = 2mm , W/COVER	12

DRAWN BY	EZELDIN
CHECKED BY	AMIR KHAN
APPROVED BY	NASSER ANANI
DATE	22-07-2026
REF NO. :	
CONSULTANT :	

TITLE: CABLE LADDER VERTICAL 30° BEND W/COVER

CLIENT: KENT GAD

SEC ITEM NO:

BONN METAL CONS. IND.

BONN GROUP OF COMPANIES
Cable Management Systems

DWRG. NO. :


REV. 01

SHEET NO. :


SCALE:NTS


NOTE:-

MATERIAL HDG 2mm ALL flange 32 mm
Hot Dip Galvnaiztion 85 M without Epoxy
MIG WELDING
Cover Height 12mm

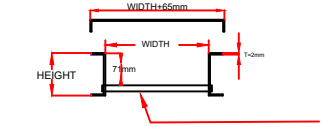


SECTION VIEW CHANNEL RUNG

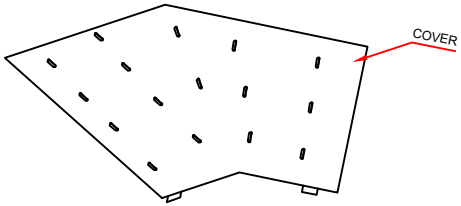


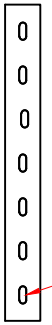


Obround 25X14

Rungs

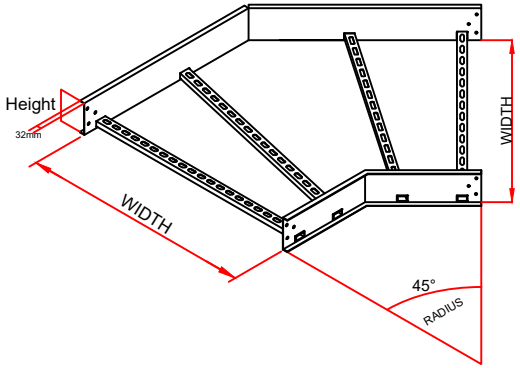

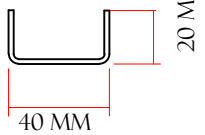

SIDE VIEW

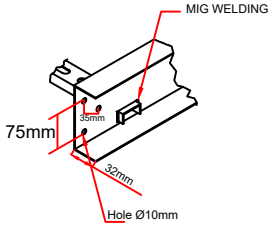

CABLE LADDER BEND 45° DEG W/COVER

SN	DIMENSION TABLE	QTY
9	W=300mm, H =100mm , R= 600mm , T = 2mm W/COVER	6
10	W=450mm, H =100mm , R= 600mm , T = 2mm ,W/COVER	2
11	W=600mm, H =100mm , R= 600mm , T = 2mm , W/COVER	12
12	W=750mm, H =100mm , R= 600mm , T = 2mm , W/COVER	12

DRAWN BY	EZELDIN
CHECKED BY	AMIR KHAN
APPROVED BY	NASSER ANANI
DATE	22-07-2026
REF NO. :	
CONSULTANT :	

TITLE: CABLE LADDER VERTICAL 45° BEND W/COVER

CLIENT: KENT GAD

SEC ITEM NO:

BONN METAL CONS. IND.


BONN GROUP OF COMPANIES
Cable Management Systems

DWRG. NO. :

REV. 01

SHEET NO. :


SCALE:NTS

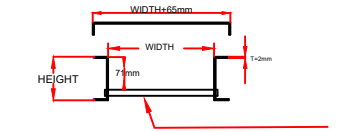


SECTION VIEW CHANNEL RUNG


NOTE:-


MATERIAL HDG 2mm ALL flange 32 mm
Hot Dip Galvnaiztion 85 M without Epoxy
MIG WELDING
Cover Height 12mm

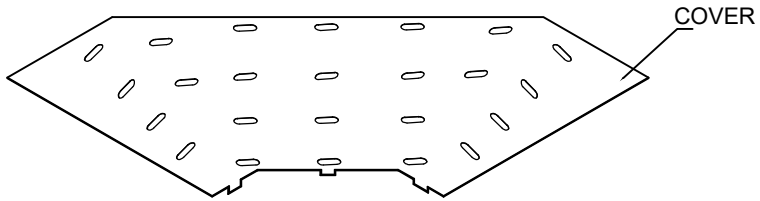

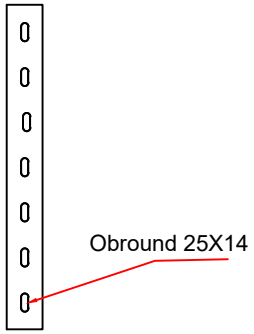


Rungs

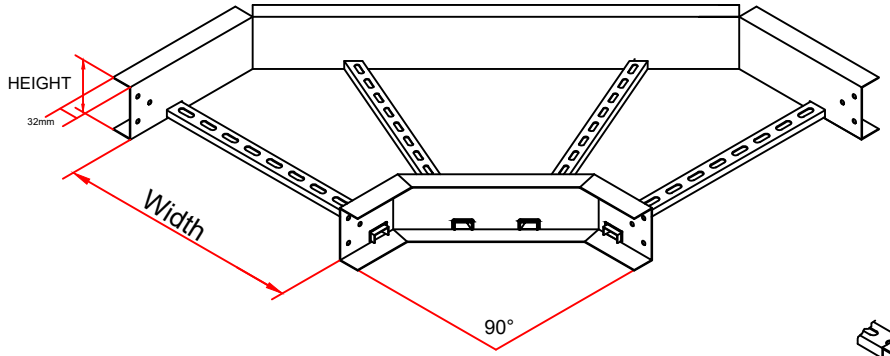

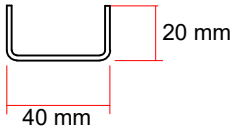

SIDE VIEW

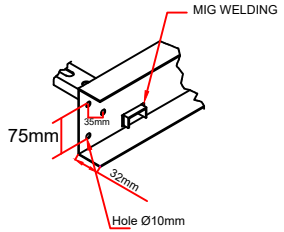

CABLE LADDER BEND 90DEG W/COVER

SN	DIMENSION TABLE	QTY
13	W=300mm, H =100mm , R= 300mm , T = 2mm W/COVER	9
14	W=300mm, H =100mm , R= 600mm , T = 2mm W/COVER	12
15	W=450mm, H =100mm , R= 600mm , T = 2mm W/COVER	3
16	W=600mm, H =100mm , R= 600mm , T = 2mm W/COVER	14
17	W=750mm, H =100mm , R= 600mm , T = 2mm W/COVER	6
18	W=900mm, H =100mm , R= 600mm , T = 2mm W/COVER	7

DRAWN BY	EZELDIN
CHECKED BY	AMIR KHAN
APPROVED BY	NASSER ANANI
DATE	22-07-2026
REF NO. :	
CONSULTANT :	

TITLE: CABLE LADDER BEND 90DEG W/COVER

CLIENT: KENT GAD

SEC ITEM NO:

BONN METAL CONS. IND.


BONN GROUP OF COMPANIES
Cable Management Systems

DWRG. NO. :

REV. 01

SHEET NO. :


SCALE:NTS

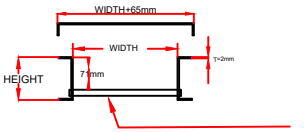


SECTION VIEW CHANNEL RUNG

NOTE:-


MATERIAL HDG 2mm ALL flange 32 mm
Hot Dip Galvnaiztion 85 M without Epoxy
MIG WELDING
Cover Height 12mm

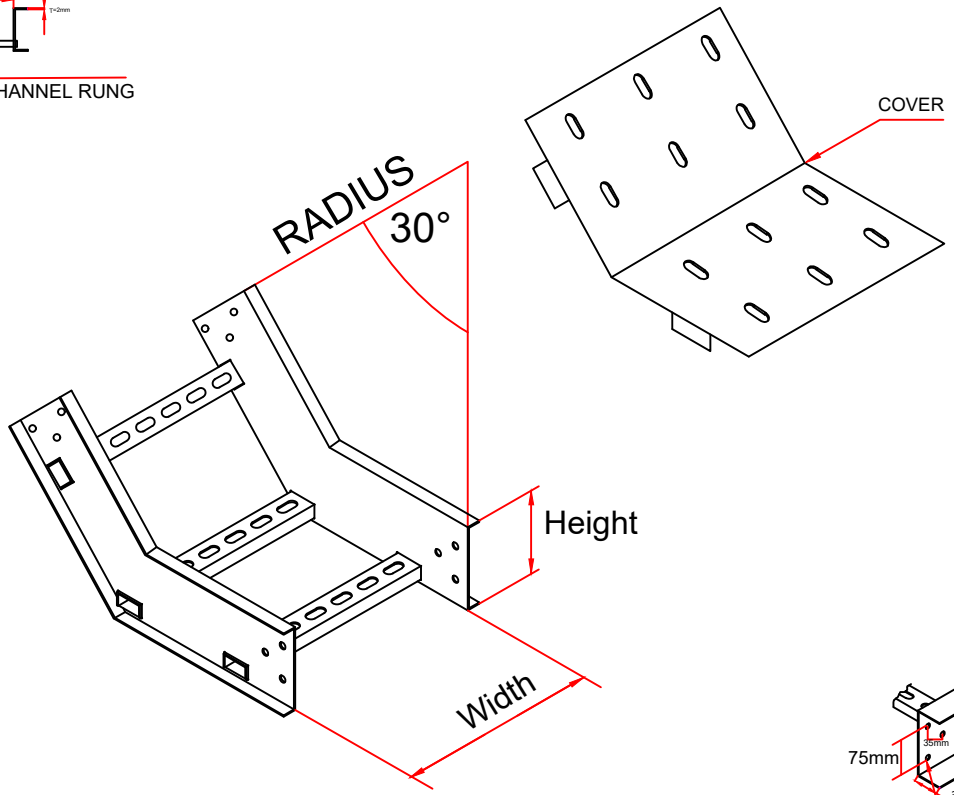


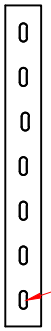

Obround 25X14

Rungs

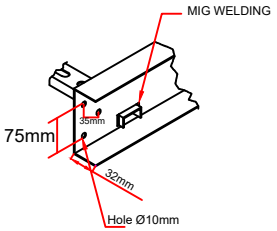

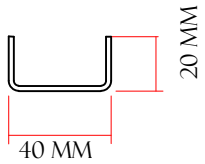

SIDE VIEW

CABLE LADDER 30° DEG INSIDE RISER

SN	DIMENSION TABLE	QTY
19	W=300mm, H =100mm , R= 300mm , T = 2mm W/COVER	12
20	W=300mm, H =100mm , R= 600mm , T = 2mm ,W/COVER	2
21	W=600mm, H =100mm , R= 600mm , T = 2mm , W/COVER	12
22	W=750mm, H =100mm , R= 600mm , T = 2mm , W/COVER	50

DRAWN BY	EZELDIN
CHECKED BY	AMIR KHAN
APPROVED BY	NASSER ANANI
DATE	22-07-2026
REF NO. :	
CONSULTANT :	

TITLE: CABLE LADDER 30° DEG INSIDE RISER

CLIENT: KENT GAD

SEC ITEM NO:

BONN METAL CONS. IND.

BONN GROUP OF COMPANIES
Cable Management Systems

DWRG. NO. :


REV. 01


SHEET NO. :


SCALE:NTS


NOTE:-


MATERIAL HDG 2mm ALL flange 32 mm
Hot Dip Galvnaiztion 85 M without Epoxy
MIG WELDING
Cover Height 12mm

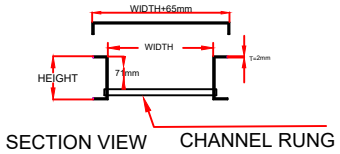


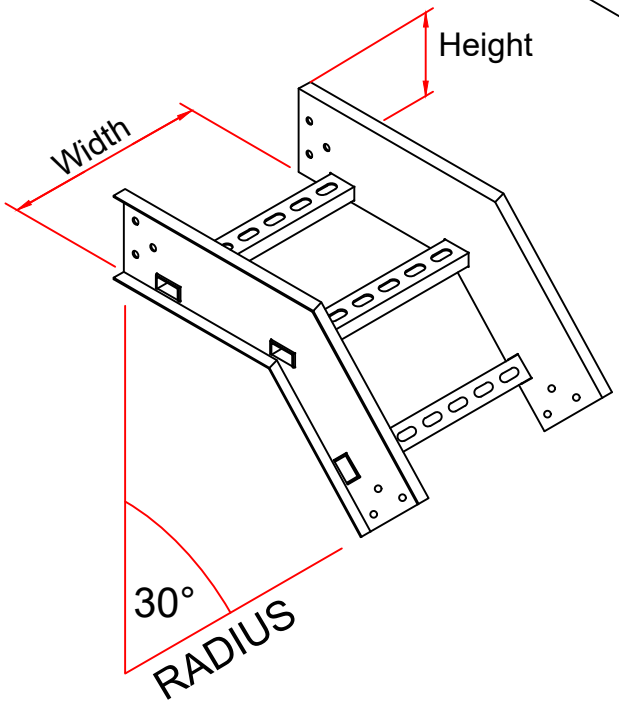

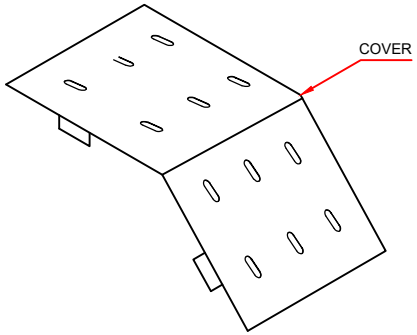

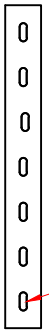

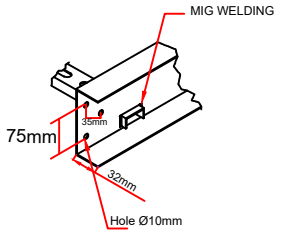

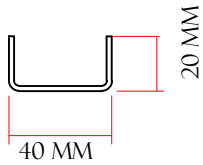

CABLE LADDER 30° DEG OUTSIDE RISER W COVER

SN	DIMENSION TABLE	QTY
23	W=300mm, H =100mm , R= 300mm , T = 2mm W/COVER	6
24	W=300mm, H =100mm , R= 600mm , T = 2mm ,W/COVER	7
25	W=600mm, H =100mm , R= 300mm , T = 2mm , W/COVER	11
26	W=600mm, H =100mm , R= 600mm , T = 2mm , W/COVER	2
27	W=750mm, H =100mm , R= 600mm , T = 2mm , W/COVER	48

DRAWN BY	EZELDIN
CHECKED BY	AMIR KHAN
APPROVED BY	NASSER ANANI
DATE	22-07-2026
REF NO. :	
CONSULTANT :	

TITLE: CABLE LADDER 30° DEG OUTSIDE RISER W COVER

CLIENT: KENT GAD

SEC ITEM NO:

BONN METAL CONS. IND.


BONN GROUP OF COMPANIES
Cable Management Systems

DWRG. NO. :

REV. 01

SHEET NO. :

SCALE:NTS

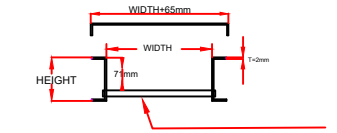



SECTION VIEW

CHANNEL RUNG


NOTE:-


MATERIAL HDG 2mm ALL flange 32 mm
Hot Dip Galvnaiztion 85 M without Epoxy
MIG WELDING
Cover Height 12mm

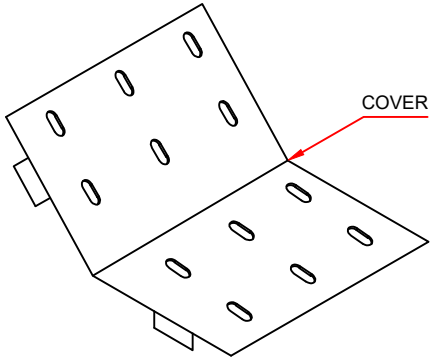


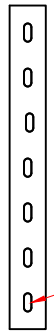

Rungs

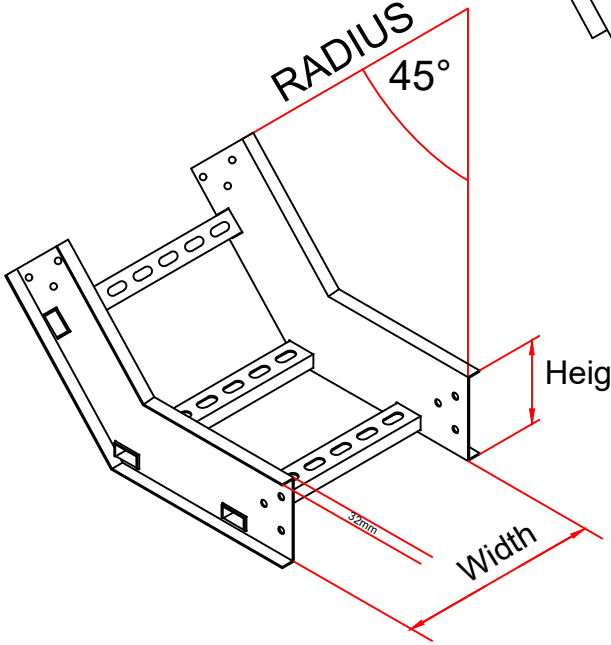

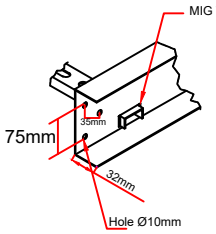

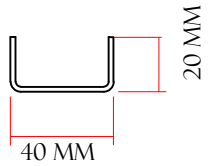

SIDE VIEW

CABLE LADDER 45° DEG (V) INSIDE RISER

SN	DIMENSION TABLE	QTY
28	W=300mm, H =100mm , R= 300mm , T = 2mm W/COVER	5
29	W=300mm, H =100mm , R= 600mm , T = 2mm ,W/COVER	2
30	W=600mm, H =100mm , R= 600mm , T = 2mm , W/COVER	4

DRAWN BY	EZELDIN
CHECKED BY	AMIR KHAN
APPROVED BY	NASSER ANANI
DATE	22-07-2026
REF NO. :	
CONSULTANT :	

TITLE: CABLE LADDER 45° DEG INSIDE RISER

CLIENT: KENT GAD

SEC ITEM NO:

BONN METAL CONS. IND.


BONN GROUP OF COMPANIES
Cable Management Systems

DWRG. NO. :

REV. 01


SHEET NO. :

SCALE:NTS

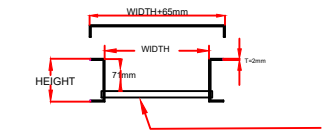


SECTION VIEW

CHANNEL RUNG

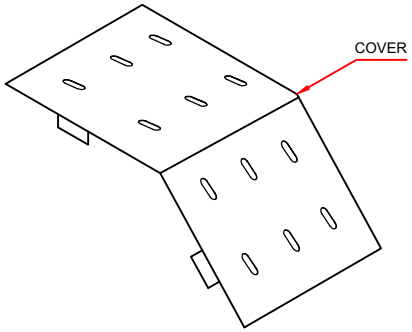


NOTE:-


MATERIAL HDG 2mm ALL flange 32 mm
Hot Dip Galvnaiztion 85 M without Epoxy
MIG WELDING
Cover Height 12mm

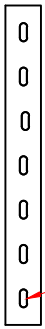


Obround 25X14

Rungs

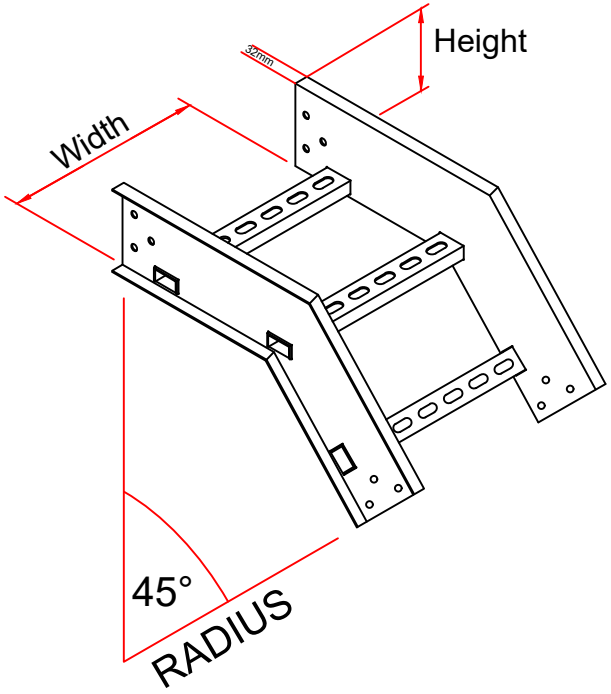

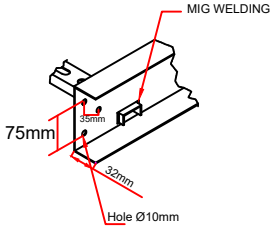

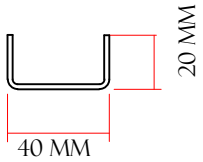

SIDE VIEW

CABLE LADDER 45° DEG (V) OUTSIDE RISER W COVER

SN	DIMENSION TABLE	QTY
31	W=300mm, H =100mm , R= 300mm , T = 2mm W/COVER	5
32	W=300mm, H =100mm , R= 600mm , T = 2mm ,W/COVER	2
33	W=600mm, H =100mm , R= 600mm , T = 2mm , W/COVER	5

DRAWN BY	EZELDIN
CHECKED BY	AMIR KHAN
APPROVED BY	NASSER ANANI
DATE	22-07-2026
REF NO. :	
CONSULTANT :	

TITLE: CABLE LADDER 45° DEG OUTSIDE RISER W COVER

CLIENT: KENT GAD

SEC ITEM NO:

BONN METAL CONS. IND.

BONN GROUP OF COMPANIES
Cable Management Systems

DWRG. NO. :


REV. 01

SHEET NO. :


SCALE:NTS


NOTE:-


MATERIAL HDG 2mm ALL flange 32 mm
Hot Dip Galvnaiztion 85 M without Epoxy
MIG WELDING
Cover Height 12mm

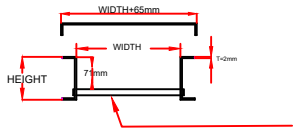

SECTION VIEW CHANNEL RUNG

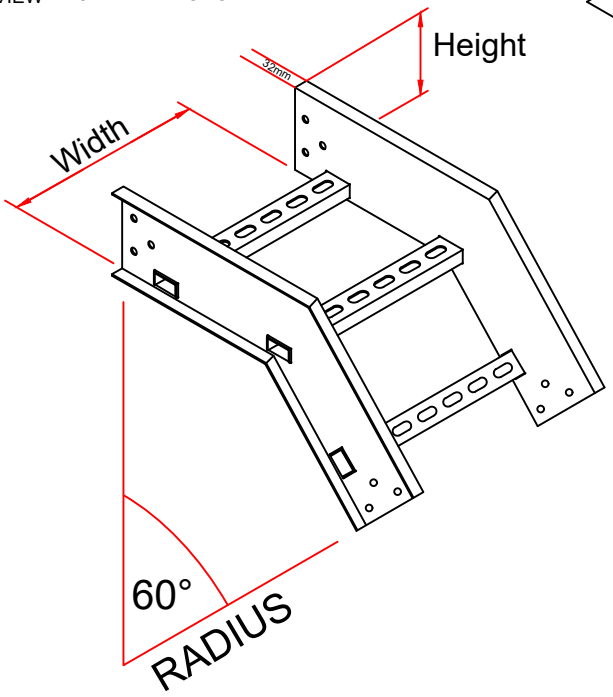


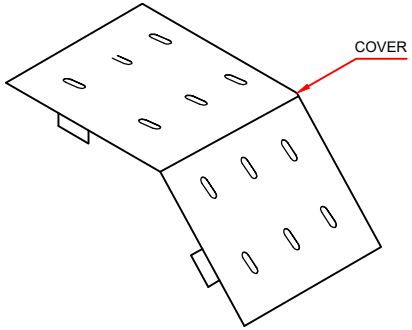

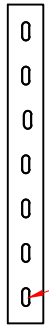


Obround 25X14

Rungs

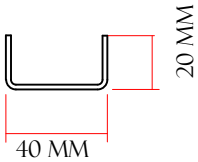

SIDE VIEW

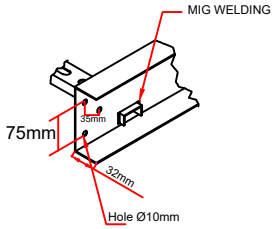

CABLE LADDER 60° DEG (V) OUTSIDE RISER W COVER

SN	DIMENSION TABLE	QTY
34	W=600mm, H =100mm , R= 600mm , T = 2mm W/COVER	14

DRAWN BY	EZELDIN
CHECKED BY	AMIR KHAN
APPROVED BY	NASSER ANANI
DATE	22-07-2026
REF NO. :	
CONSULTANT :	

TITLE: CABLE LADDER 60° DEG OUTSIDE RISER W COVER

CLIENT: KENT GAD

SEC ITEM NO:

BONN METAL CONS. IND.


BONN GROUP OF COMPANIES
Cable Management Systems

DWRG. NO. :


REV. 01

SHEET NO. :

SCALE:NTS

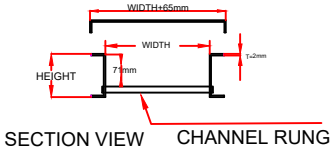


SECTION VIEW CHANNEL RUNG

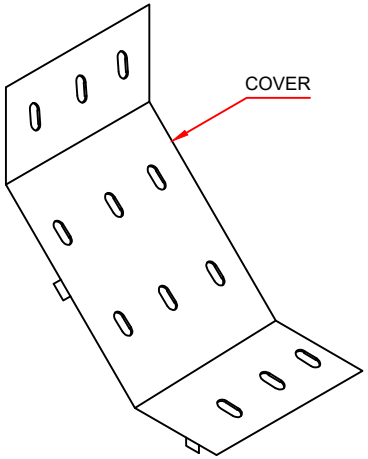


NOTE:-


MATERIAL HDG 2mm ALL flange 32 mm
Hot Dip Galvnaiztion 85 M without Epoxy
MIG WELDING
Cover Height 12mm

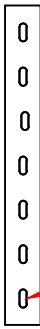


Obround 25X14

Rungs

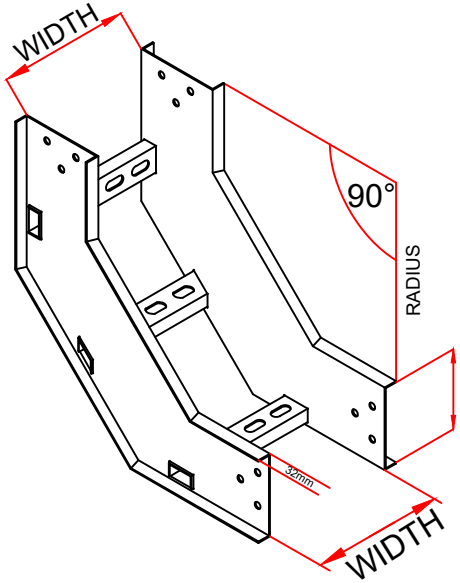

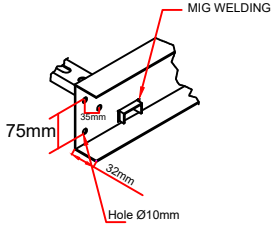

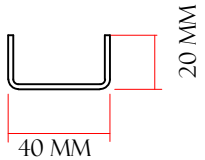

SIDE VIEW

CABLE LADDER BEND 90° INSIDE RISER W/COVER

SN	DIMENSION TABLE	QTY
35	W=300mm, H =100mm , R= 600mm , T = 2mm W/COVER	3
36	W=450mm, H =100mm , R= 600mm , T = 2mm ,W/COVER	3
37	W=600mm, H =100mm , R= 600mm , T = 2mm , W/COVER	9

DRAWN BY	EZELDIN
CHECKED BY	AMIR KHAN
APPROVED BY	NASSER ANANI
DATE	22-07-2026
REF NO. :	
CONSULTANT :	

TITLE: CABLE LADDER BEND 90° INSIDE RISER W/COVER

CLIENT: KENT GAD

SEC ITEM NO:

BONN METAL CONS. IND.


BONN GROUP OF COMPANIES
Cable Management Systems

DWRG. NO. :

REV. 01


SHEET NO. :


SCALE:NTS

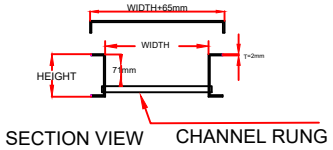



NOTE:-


MATERIAL HDG 2mm ALL flange 32 mm
Hot Dip Galvnaiztion 85 M without Epoxy
MIG WELDING
Cover Height 12mm

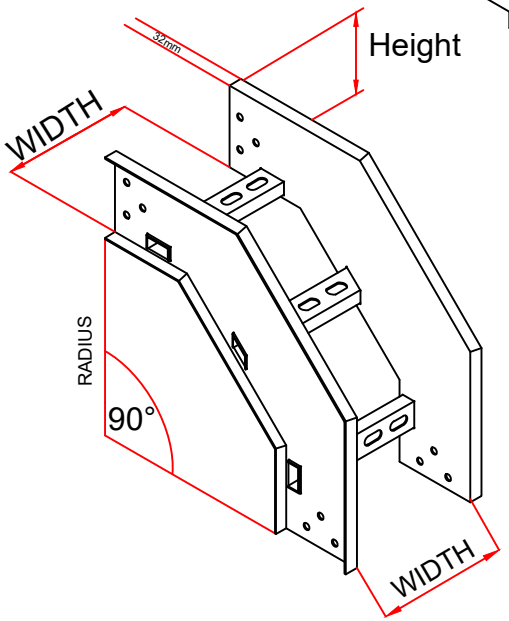

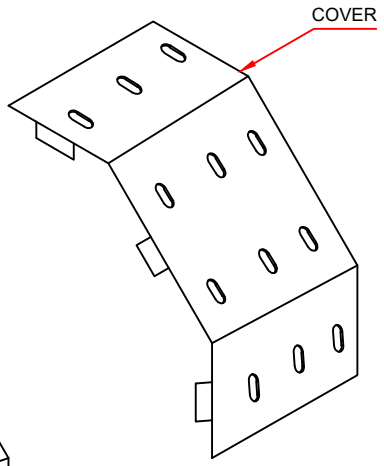

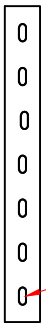

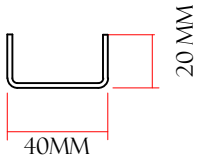

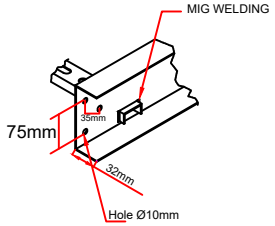

CABLE LADDER BEND 90° OUTSIDE RISER W/COVER

SN	DIMENSION TABLE	QTY
38	W=300mm, H =100mm , R= 300mm , T = 2mm W/COVER	5
39	W=300mm, H =100mm , R= 600mm , T = 2mm ,W/COVER	8
40	W=450mm, H =100mm , R= 600mm , T = 2mm , W/COVER	5
41	W=600mm, H =100mm , R= 600mm , T = 2mm , W/COVER	7

DRAWN BY	EZELDIN
CHECKED BY	AMIR KHAN
APPROVED BY	NASSER ANANI
DATE	22-07-2026
REF NO. :	
CONSULTANT :	

TITLE: CABLE LADDER BEND 90° OUTSIDE RISER W/COVER

CLIENT: KENT GAD

SEC ITEM NO:

BONN METAL CONS. IND.


BONN GROUP OF COMPANIES
Cable Management Systems


DWRG. NO. :

REV. 01

SHEET NO. :


SCALE:NTS

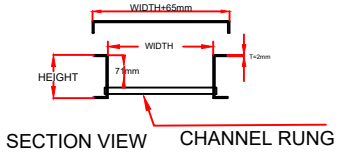

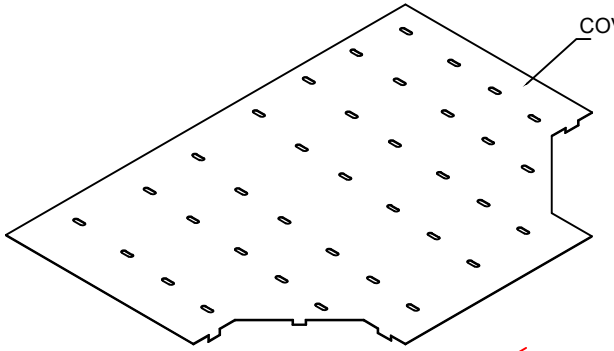


NOTE:-

MATERIAL HDG 2mm ALL flange 32 mm
Hot Dip Galvnaiztion 85 M without Epoxy
MIG WELDING
Cover Height 12mm

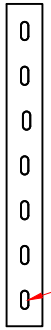



Obround 25X14

Rungs

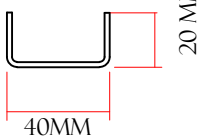

SIDE VIEW

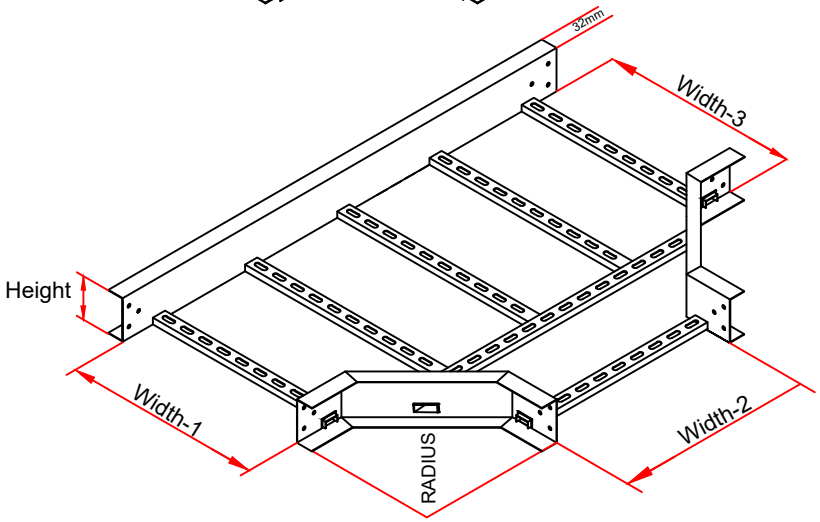

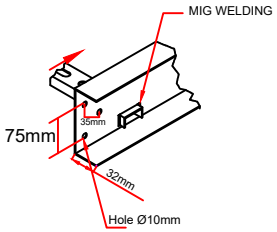

CABLE LADDER EQUAL TEE W/COVER

SN	DIMENSION TABLE	QTY
42	W=300mm, H =100mm , R= 600mm , T = 2mm W/COVER	2
43	W=750mm, H =100mm , R= 600mm , T = 2mm ,W/COVER	12
44	W=750mm, H =100mm , R= 300mm , T = 2mm , W/COVER	16

DRAWN BY	EZELDIN
CHECKED BY	AMIR KHAN
APPROVED BY	NASSER ANANI
DATE	22-07-2026
REF NO. :	
CONSULTANT :	

TITLE: CABLE LADDER EQUAL TEE W/COVER

CLIENT: KENT GAD

SEC ITEM NO:

BONN METAL CONS. IND.


BONN GROUP OF COMPANIES
Cable Management Systems


DWRG. NO. :

REV. 01

SHEET NO. :


SCALE:NTS

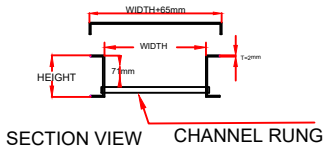

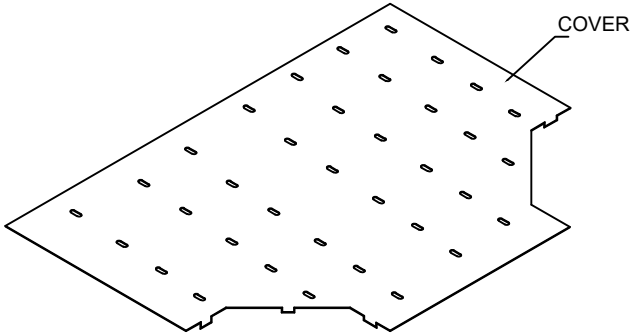


NOTE:-

MATERIAL HDG 2mm ALL flange 32 mm
Hot Dip Galvnaiztion 85 M without Epoxy
MIG WELDING
Cover Height 12mm

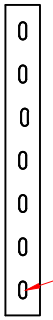



Obround 25X14

Rungs

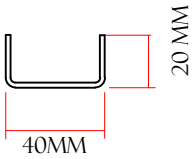

SIDE VIEW

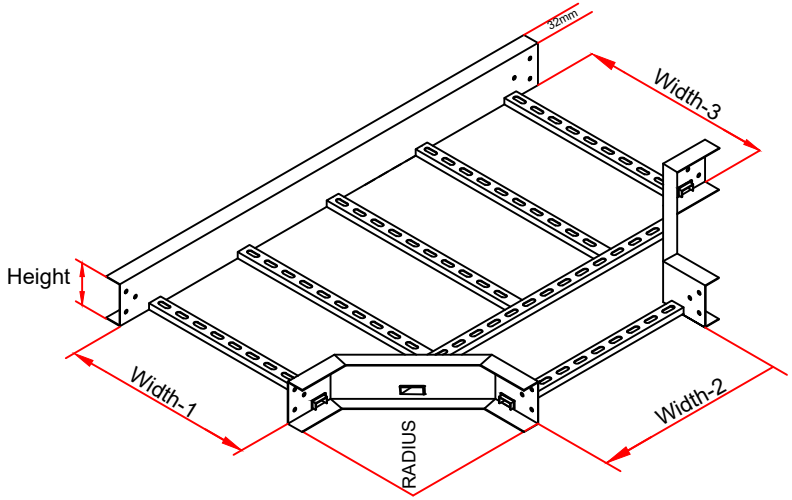

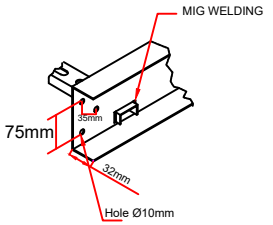

CABLE LADDER UNEQUAL TEE W/COVER

SN	DIMENSION TABLE	QTY
45	W1 =300mm, W2 =150mm,W3 =300mm,H =100mm ,R= 300mm ,T = 2mm W/COVER	3
46	W1 =450mm, W2 =150mm,W3 =450mm,H =100mm ,R= 300mm ,T = 2mm W/COVER	2

DRAWN BY	EZELDIN
CHECKED BY	AMIR KHAN
APPROVED BY	NASSER ANANI
DATE	22-07-2026
REF NO. :	
CONSULTANT :	

TITLE: CABLE LADDER EQUAL TEE W/COVER

CLIENT: KENT GAD

SEC ITEM NO:

BONN METAL CONS. IND.

BONN GROUP OF COMPANIES
Cable Management Systems

DWRG. NO. :


REV. 01

SHEET NO. :


SCALE:NTS


NOTE:-

MATERIAL HDG 2mm ALL flange 32 mm
Hot Dip Galvnaiztion 85 M without Epoxy
MIG WELDING
Cover Height 12mm

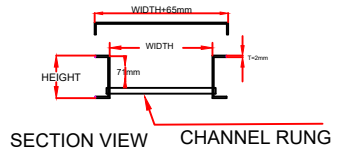


SECTION VIEW CHANNEL RUNG

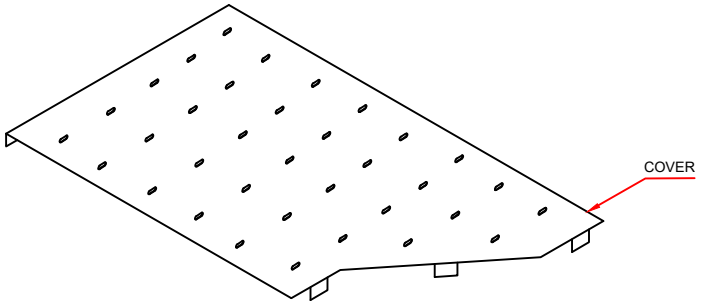


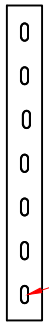


Rungs

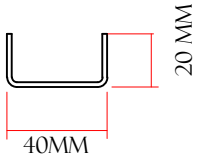

SIDE VIEW

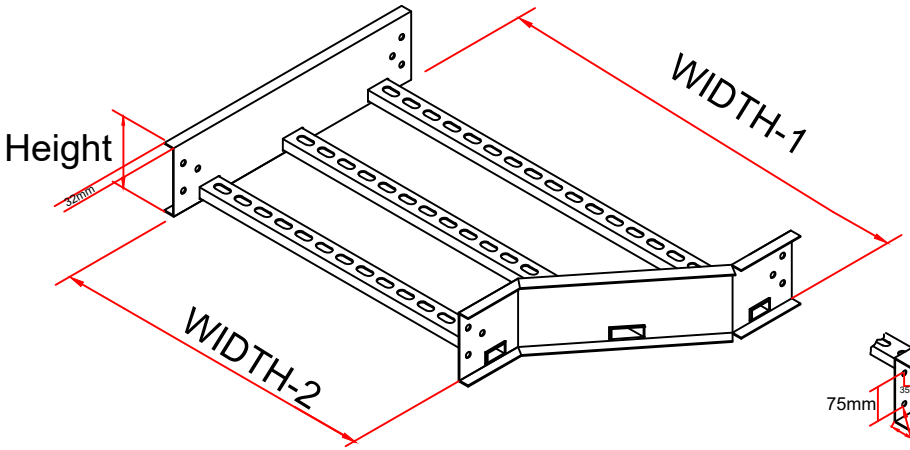


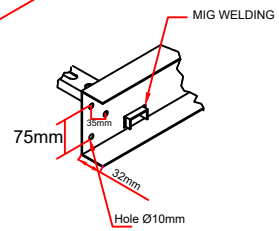


CABLE LADDER LEFT REDUCER W/COVER

SN	DIMENSION TABLE	QTY	DRAWN BY	EZELDIN	TITLE: CABLE LADDER LEFT REDUCER W/COVER	BONN METAL CONS. IND.
47	W1 =300mm, W2 =150mm , H =100mm ,T = 2mm W/COVER	4	CHECKED BY	AMIR KHAN		
			APPROVED BY	NASSER ANANI	CLIENT: KENT GAD	
			DATE	22-07-2026		
			REF NO. :		SEC ITEM NO:	DWRG. NO. :
			CONSULTANT :			SHEET NO. : / SCALE:NTS / REV. 01

BONN GROUP OF COMPANIES
Cable Management Systems

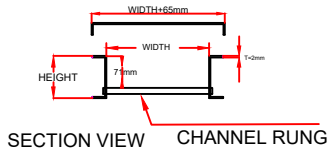


SECTION VIEW CHANNEL RUNG

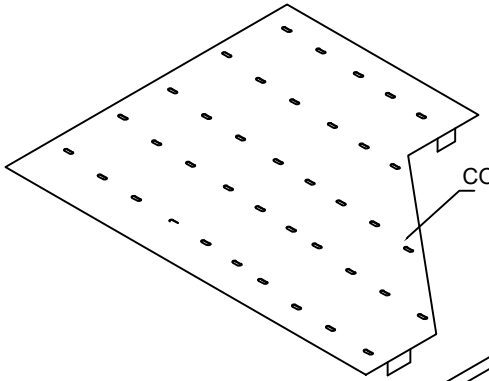


NOTE:-


MATERIAL HDG 2mm ALL flange 32 mm
Hot Dip Galvnaiztion 85 M without Epoxy
MIG WELDING
Cover Height 12mm

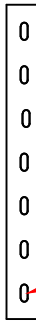


Obround 25X14

Rungs

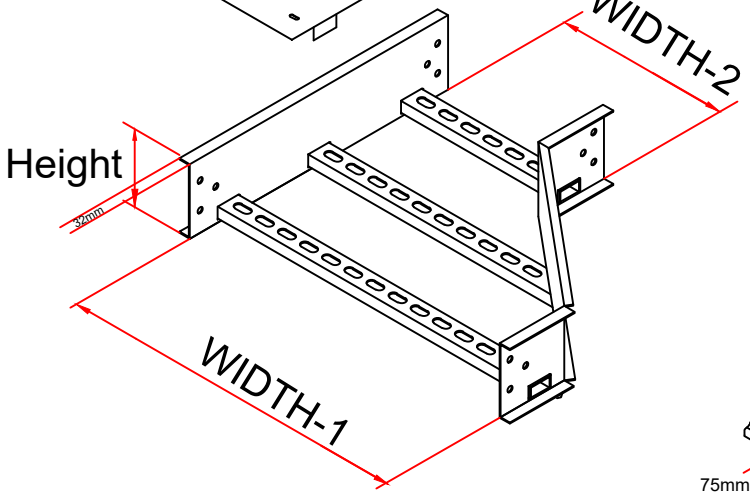

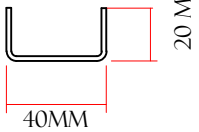

SIDE VIEW

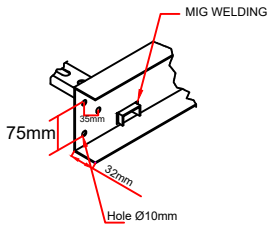

CABLE LADDER RIGHT REDUCER W/COVER

SN	DIMENSION TABLE	QTY
48	W1 =900mm, W2 =600mm , H =100mm ,T = 2mm W/COVER	2
49	W1 =600mm, W2 =300mm , H =100mm ,T = 2mm W/COVER	2
50	W1 =450mm, W2 =150mm , H =100mm ,T = 2mm W/COVER	2
51	W1 =300mm, W2 =150mm , H =100mm ,T = 2mm W/COVER	3

DRAWN BY	EZELDIN
CHECKED BY	AMIR KHAN
APPROVED BY	NASSER ANANI
DATE	22-07-2026
REF NO. :	
CONSULTANT :	

TITLE: CABLE LADDER RIGHT REDUCER W/COVER

CLIENT: KENT GAD

SEC ITEM NO:

BONN METAL CONS. IND.

BONN GROUP OF COMPANIES
Cable Management Systems

DWRG. NO. :


SHEET NO. :

SCALE:NTS


REV. 01


NOTE:-

MATERIAL HDG 2mm ALL flange 32 mm
Hot Dip Galvnaiztion 85 M without Epoxy
MIG WELDING
Cover Height 12mm

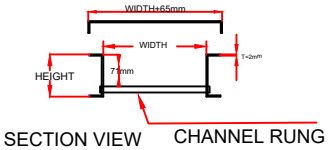


SECTION VIEW CHANNEL RUNG

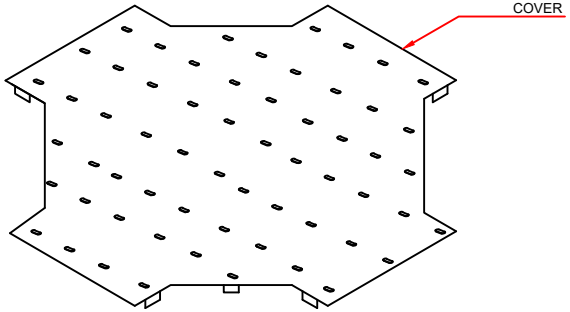

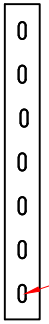



Obround 25X14

Rungs

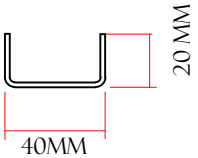

SIDE VIEW

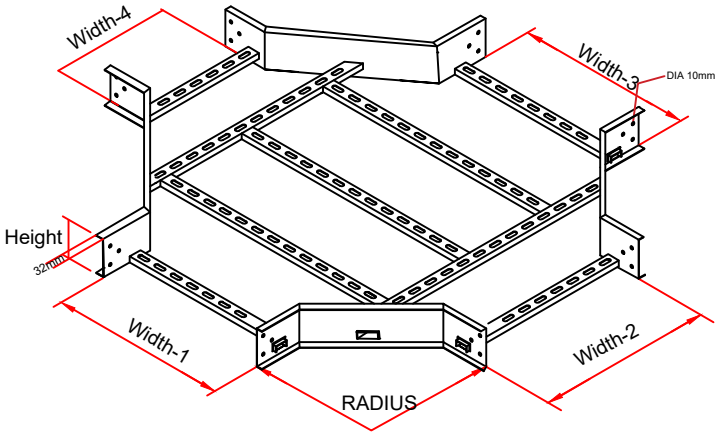

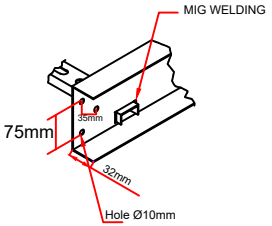

CABLE LADDER CROSS W/COVER

SN	DIMENSION TABLE	QTY
52	W = 750mm, H =100mm , R= 600mm , T = 2mm ,W/COVER	7
53	W = 600mm, H =100mm , R= 600mm , T = 2mm W/COVER	3

DRAWN BY	EZELDIN
CHECKED BY	AMIR KHAN
APPROVED BY	NASSER ANANI
DATE	22-07-2026
REF NO. :	
CONSULTANT :	

TITLE: CABLE LADDER CROSS W/COVER

CLIENT: KENT GAD

SEC ITEM NO:

BONN METAL CONS. IND.

BONN GROUP OF COMPANIES
Cable Management Systems

DWRG. NO. :

SHEET NO. :


SCALE:NTS

REV. 01

SECTION VIEW


CHANNEL RUNG


NOTE:-
MATERIAL HDG 2mm
Rung Spacing 250mm ALL flange 32 mm
Hot Dip Galvnaiztion 85 M without Epoxy
MIG WELDING
Cover Height 12mm

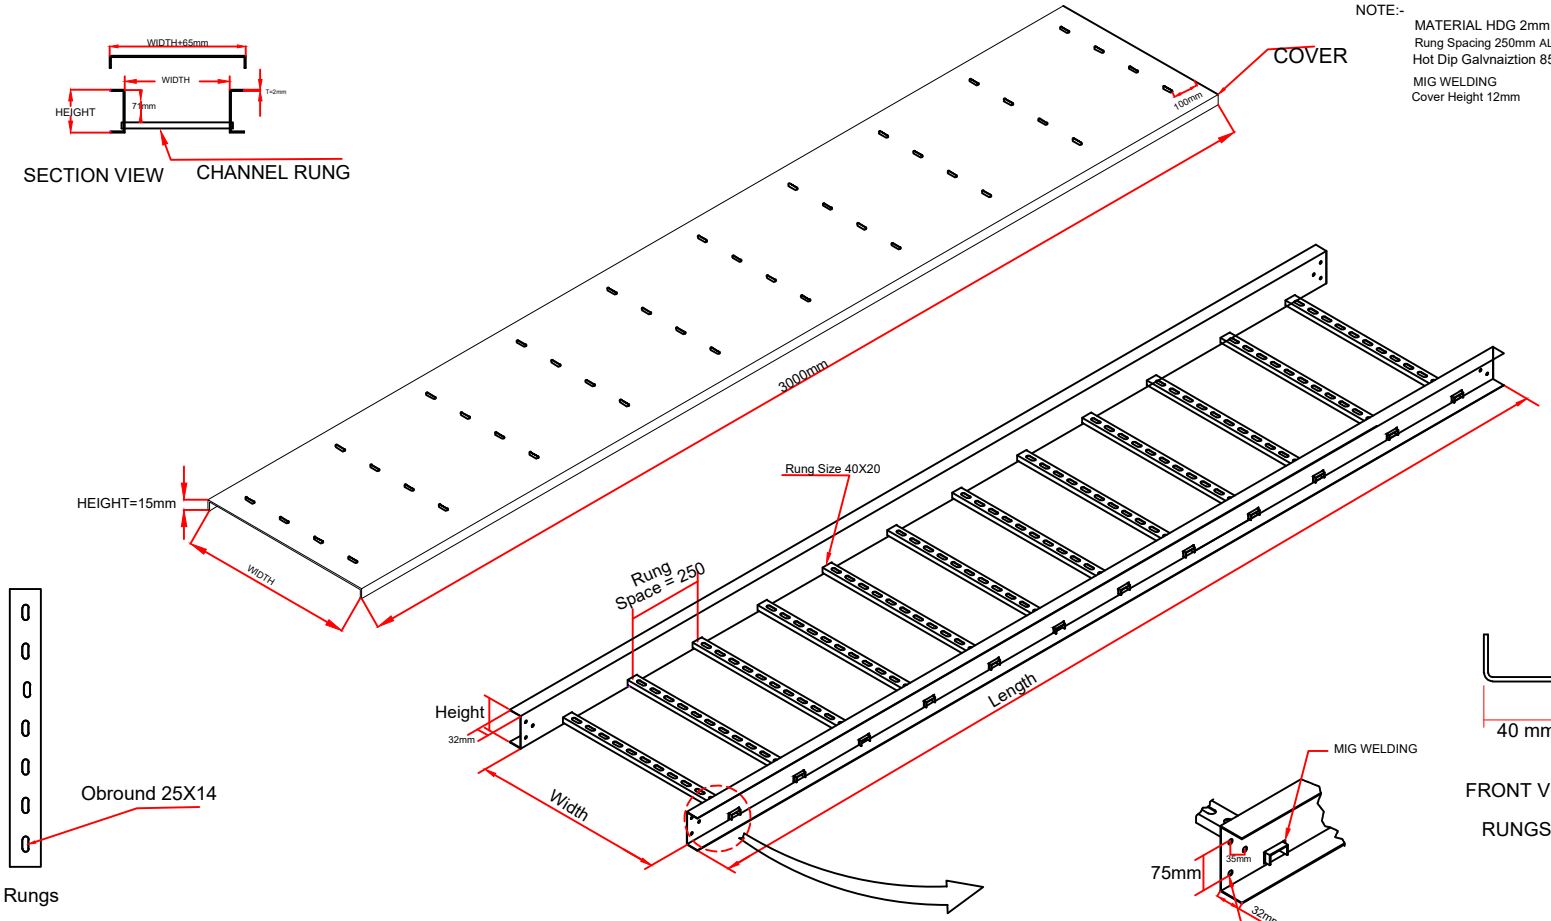

Obround 25X14

Rungs

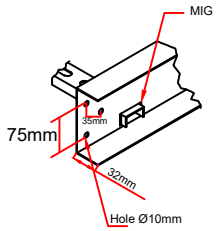

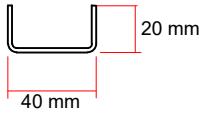

FRONT VIEW

RUNGS

CABLE LADDER STRAIGHT LENGTH W/ COVER

SN	DIMENSION TABLE	QTY
54	W=900mm, H=100mm, T=2mm & L=3000mm W/COVER	32
55	W=750mm, H=100mm, T=2mm & L=3000mm W/COVER	17
56	W=600mm, H=100mm, T=2mm & L=3000mm W/COVER	378
57	W=450mm, H=100mm, T=2mm & L=3000mm W/COVER	50
58	W=300mm, H=100mm, T=2mm & L=3000mm W/COVER	405

DRAWN BY	EZELDIN
CHECKED BY	AMIR KHAN
APPROVED BY	NASSER ANANI
DATE	22-07-2026
REF NO. :	
CONSULTANT :	

TITLE: CABLE LADDER STRAIGHT LENGTH W/ COVER

CLIENT: KENT GAD

SEC ITEM NO:

BONN METAL CONS. IND.

BONN GROUP OF COMPANIES
Cable Management Systems

DWRG. NO. :


REV. 01


SHEET NO. :


SCALE:NTS


NOTE:-


MATERIAL HDG 2mm ALL flange 32 mm
Hot Dip Galvnaiztion 85 M without Epoxy
MIG WELDING
Cover Height 12mm

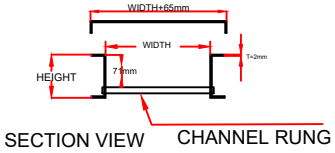

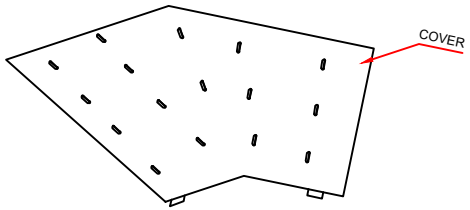

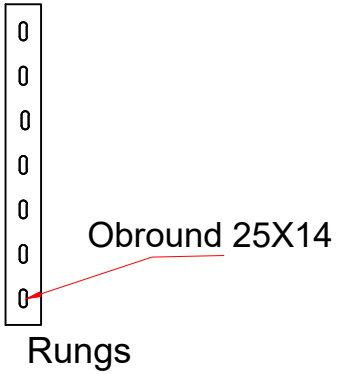

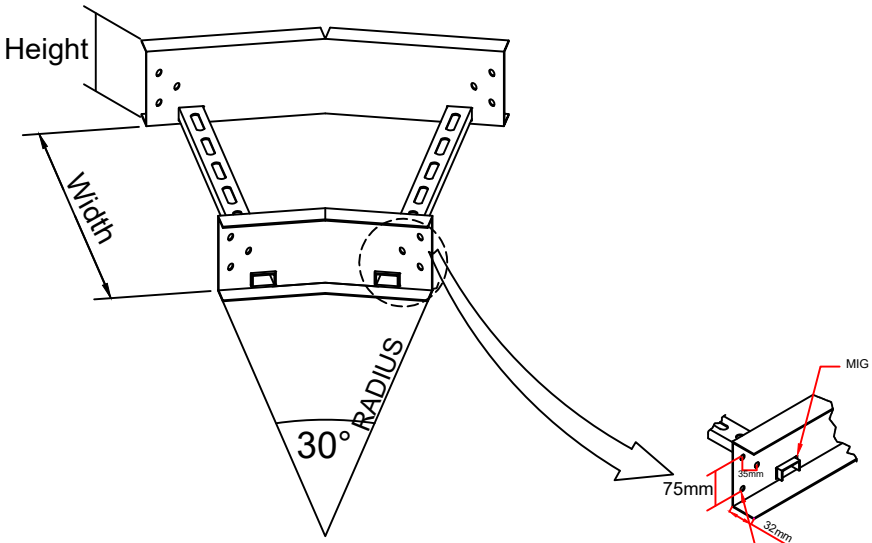

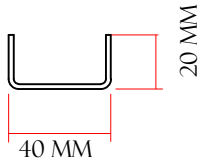

SIDE VIEW

CABLE LADDER BEND 30°DEG W/COVER

SN	DIMENSION TABLE	QTY
59	W=300mm, H =100mm , R= 300mm , T = 2mm , W/COVER	7
60	W=300mm, H =100mm , R= 600mm , T = 2mm , W/COVER	2
61	W=600mm, H =100mm , R= 600mm , T = 2mm , W/COVER	12

DRAWN BY	EZELDIN
CHECKED BY	AMIR KHAN
APPROVED BY	NASSER ANANI
DATE	22-07-2026
REF NO. :	
CONSULTANT :	

TITLE: CABLE LADDER VERTICAL 30° BEND W/COVER

CLIENT: KENT GAD

SEC ITEM NO:

BONN METAL CONS. IND.

BONN GROUP OF COMPANIES
Cable Management Systems

DWRG. NO. :


REV. 01

SHEET NO. :


SCALE:NTS


NOTE:-

MATERIAL HDG 2mm ALL flange 32 mm
Hot Dip Galvnaiztion 85 M without Epoxy
MIG WELDING
Cover Height 12mm

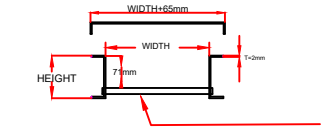


SECTION VIEW CHANNEL RUNG

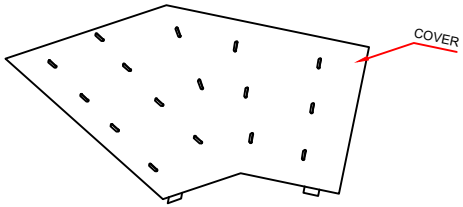


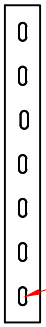


Obround 25X14

Rungs

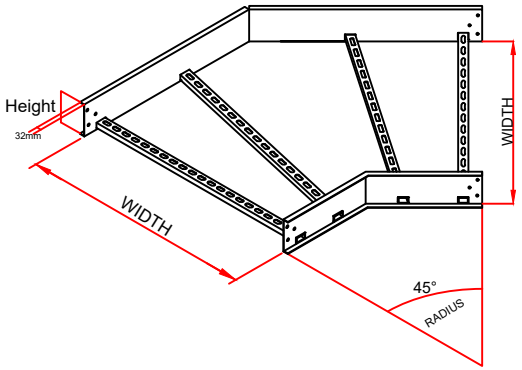

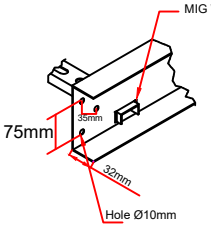

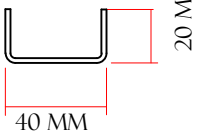

SIDE VIEW

CABLE LADDER BEND 45° DEG W/COVER

SN	DIMENSION TABLE	QTY
62	W=300mm, H =100mm , R= 600mm , T = 2mm W/COVER	6
63	W=450mm, H =100mm , R= 600mm , T = 2mm ,W/COVER	2
64	W=600mm, H =100mm , R= 600mm , T = 2mm , W/COVER	12
65	W=750mm, H =100mm , R= 600mm , T = 2mm , W/COVER	7

DRAWN BY	EZELDIN
CHECKED BY	AMIR KHAN
APPROVED BY	NASSER ANANI
DATE	22-07-2026
REF NO. :	
CONSULTANT :	

TITLE: CABLE LADDER VERTICAL 45° BEND W/COVER

CLIENT: KENT GAD

SEC ITEM NO:

BONN METAL CONS. IND.

BONN GROUP OF COMPANIES
Cable Management Systems

DWRG. NO. :

REV. 01

SHEET NO. :


SCALE:NTS

Project: 04108 EPC FOR SE AiP5 PROJECT (ON PLOT) – ASAB/SAHIL (PACKAGE 1)


ELECTRICAL CABLE TRAY AND ACCESSORIES - SAHIL -WITHOUT EPOXY


NOTE:-

MATERIAL HDG 3mm
Hot Dip Galvnaiztion 85 M without Epoxy
MATERIAL HDG 2mm FOR COVER
Cover Height 12mm

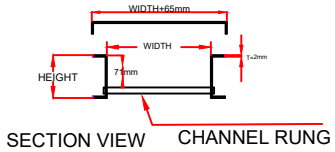



SECTION VIEW CHANNEL RUNG

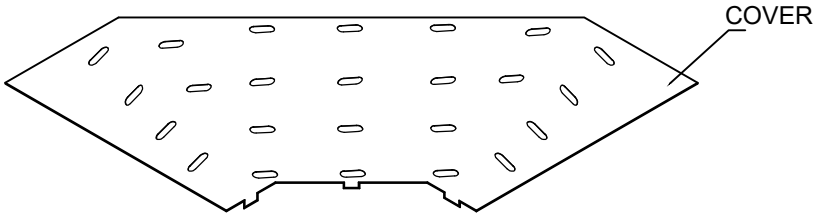

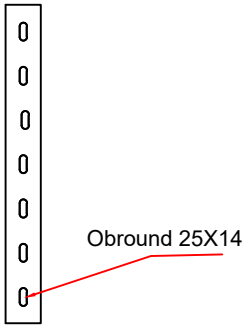


Rungs

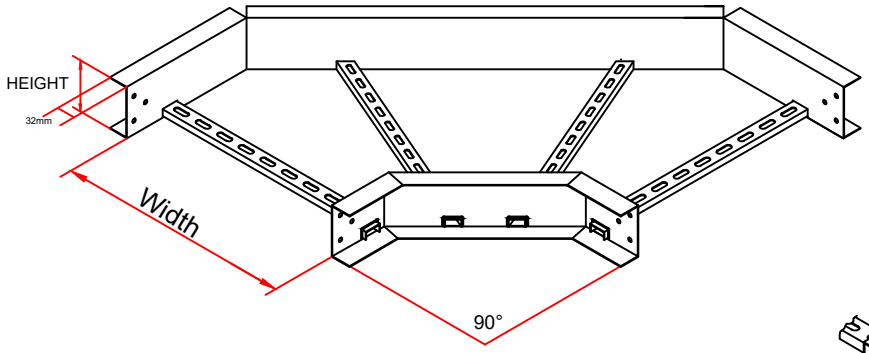

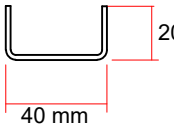

SIDE VIEW

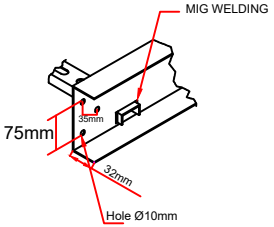

CABLE LADDER BEND 90DEG W/COVER

SN	DIMENSION TABLE	QTY
66	W=300mm, H =100mm , R= 300mm , T = 2mm W/COVER	9
67	W=300mm, H =100mm , R= 600mm , T = 2mm W/COVER	12
68	W=450mm, H =100mm , R= 600mm , T = 2mm W/COVER	3
69	W=600mm, H =100mm , R= 600mm , T = 2mm W/COVER	14
70	W=900mm, H =100mm , R= 600mm , T = 2mm W/COVER	7

DRAWN BY	EZELDIN
CHECKED BY	AMIR KHAN
APPROVED BY	NASSER ANANI
DATE	22-07-2026
REF NO. :	
CONSULTANT :	

TITLE: CABLE LADDER BEND 90DEG W/COVER

CLIENT: KENT GAD

SEC ITEM NO:

BONN METAL CONS. IND.

BONN GROUP OF COMPANIES
Cable Management Systems

DWRG. NO. :


REV. 01

SHEET NO. :


SCALE:NTS


NOTE:-

MATERIAL HDG 2mm ALL flange 32 mm
Hot Dip Galvnaiztion 85 M without Epoxy
MIG WELDING
Cover Height 12mm

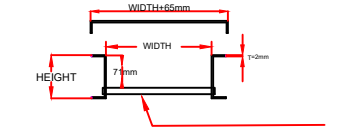


SECTION VIEW CHANNEL RUNG

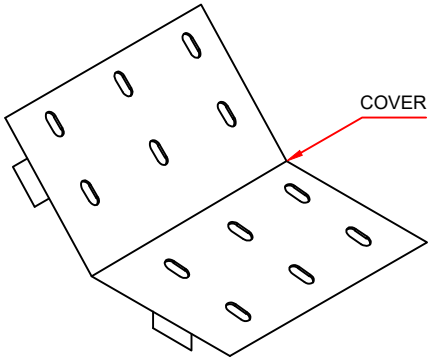


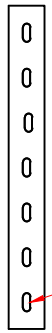


Obround 25X14

Rungs

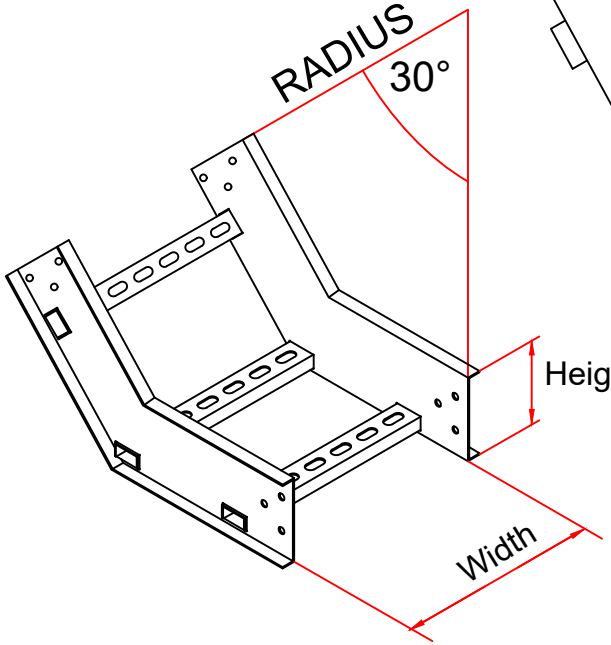

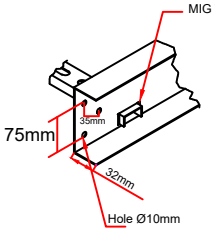

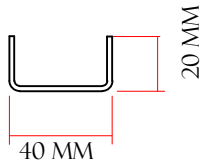

SIDE VIEW

CABLE LADDER 30° DEG INSIDE RISER

SN	DIMENSION TABLE	QTY
71	W=300mm, H =100mm , R= 300mm , T = 2mm W/COVER	6
72	W=300mm, H =100mm , R= 600mm , T = 2mm ,W/COVER	3
73	W=600mm, H =100mm , R= 600mm , T = 2mm , W/COVER	12

DRAWN BY	EZELDIN
CHECKED BY	AMIR KHAN
APPROVED BY	NASSER ANANI
DATE	22-07-2026
REF NO. :	
CONSULTANT :	

TITLE: CABLE LADDER 30° DEG INSIDE RISER

CLIENT: KENT GAD

SEC ITEM NO:

BONN METAL CONS. IND.


BONN GROUP OF COMPANIES
Cable Management Systems

DWRG. NO. :

REV. 01


SHEET NO. :


SCALE:NTS

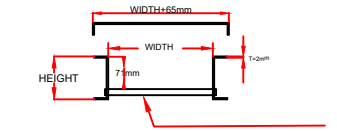

SECTION VIEW


CHANNEL RUNG

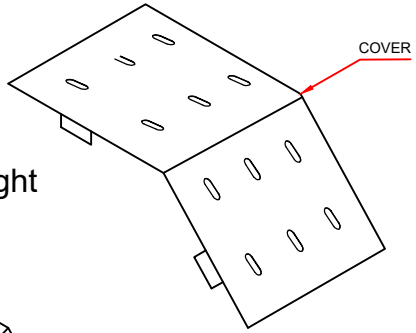

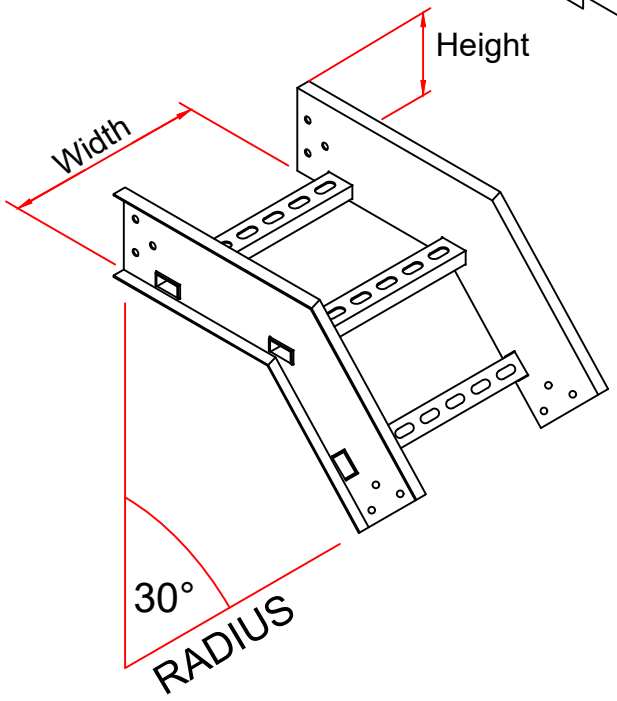


NOTE:-


MATERIAL HDG 2mm ALL flange 32 mm
Hot Dip Galvnaiztion 85 M without Epoxy
MIG WELDING
Cover Height 12mm

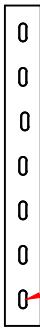

Obround 25X14

Rungs

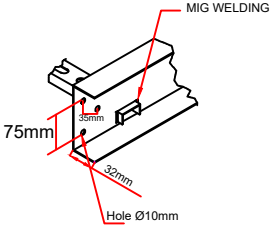

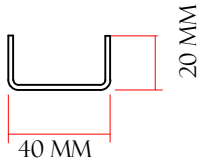

SIDE VIEW

CABLE LADDER 30° DEG OUTSIDE RISER W COVER

SN	DIMENSION TABLE	QTY
74	W=300mm, H =100mm , R= 300mm , T = 2mm W/COVER	6
75	W=300mm, H =100mm , R= 600mm , T = 2mm ,W/COVER	3
76	W=600mm, H =100mm , R= 300mm , T = 2mm , W/COVER	11
77	W=600mm, H =100mm , R= 600mm , T = 2mm , W/COVER	2

DRAWN BY	EZELDIN
CHECKED BY	AMIR KHAN
APPROVED BY	NASSER ANANI
DATE	22-07-2026
REF NO. :	
CONSULTANT :	

TITLE: CABLE LADDER 30° DEG OUTSIDE RISER W COVER

CLIENT: KENT GAD

SEC ITEM NO:

BONN METAL CONS. IND.

BONN GROUP OF COMPANIES
Cable Management Systems

DWRG. NO. :


REV. 01

SHEET NO. :


SCALE:NTS


NOTE:-

MATERIAL HDG 2mm ALL flange 32 mm
Hot Dip Galvnaiztion 85 M without Epoxy
MIG WELDING
Cover Height 12mm

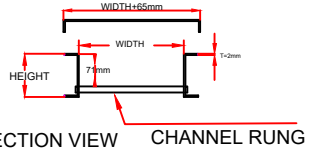


SECTION VIEW CHANNEL RUNG

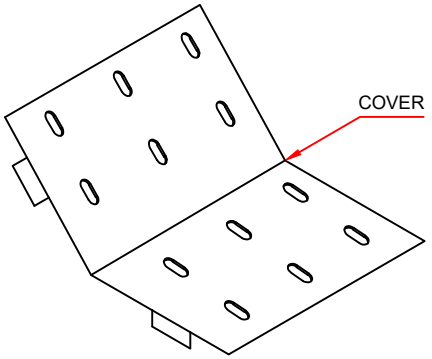


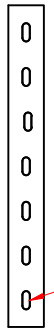


Obround 25X14

Rungs

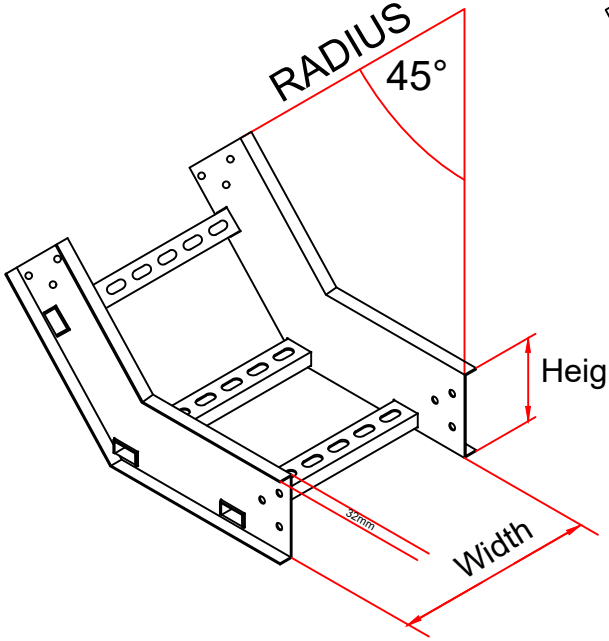

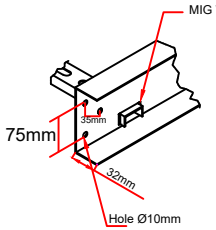

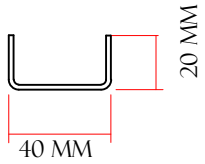

SIDE VIEW

CABLE LADDER 45° DEG (V) INSIDE RISER

SN	DIMENSION TABLE	QTY
78	W=300mm, H =100mm , R= 300mm , T = 2mm W/COVER	5
79	W=300mm, H =100mm , R= 600mm , T = 2mm ,W/COVER	2
80	W=600mm, H =100mm , R= 600mm , T = 2mm , W/COVER	4

DRAWN BY	EZELDIN
CHECKED BY	AMIR KHAN
APPROVED BY	NASSER ANANI
DATE	22-07-2026
REF NO. :	
CONSULTANT :	

TITLE: CABLE LADDER 45° DEG INSIDE RISER

CLIENT: KENT GAD

SEC ITEM NO:

BONN METAL CONS. IND.

BONN GROUP OF COMPANIES
Cable Management Systems

DWRG. NO. :


REV. 01


SHEET NO. :


SCALE:NTS


NOTE:-


MATERIAL HDG 2mm ALL flange 32 mm
Hot Dip Galvnaiztion 85 M without Epoxy
MIG WELDING
Cover Height 12mm

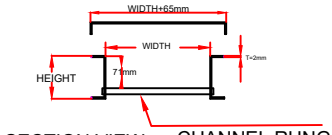


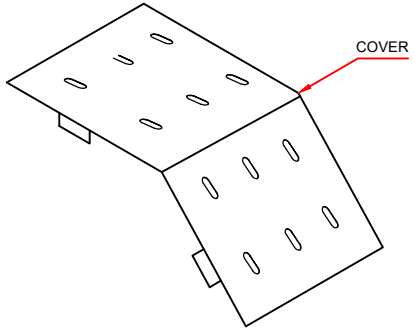

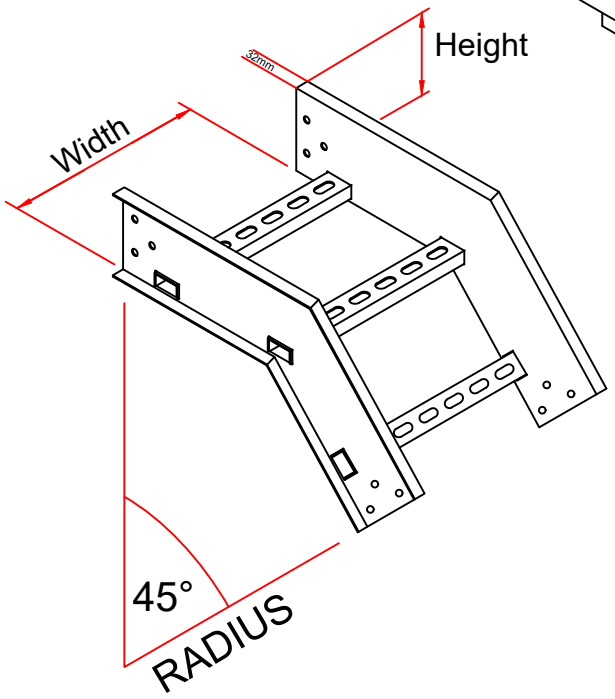

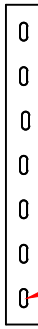

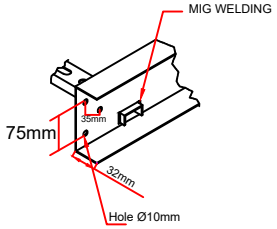

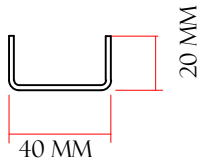

CABLE LADDER 45° DEG (V) OUTSIDE RISER W COVER

SN	DIMENSION TABLE	QTY
81	W=300mm, H =100mm , R= 300mm , T = 2mm W/COVER	5
82	W=300mm, H =100mm , R= 600mm , T = 2mm ,W/COVER	2
83	W=600mm, H =100mm , R= 600mm , T = 2mm , W/COVER	5

DRAWN BY	EZELDIN
CHECKED BY	AMIR KHAN
APPROVED BY	NASSER ANANI
DATE	22-07-2026
REF NO. :	
CONSULTANT :	

TITLE: CABLE LADDER 45° DEG OUTSIDE RISER W COVER

CLIENT: KENT GAD

SEC ITEM NO:

BONN METAL CONS. IND.

BONN GROUP OF COMPANIES
Cable Management Systems

DWRG. NO. :


REV. 01

SHEET NO. :


SCALE:NTS


NOTE:-


MATERIAL HDG 2mm ALL flange 32 mm
Hot Dip Galvnaiztion 85 M without Epoxy
MIG WELDING
Cover Height 12mm

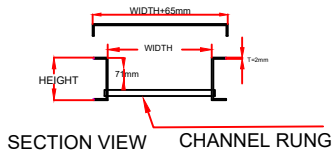

SECTION VIEW CHANNEL RUNG

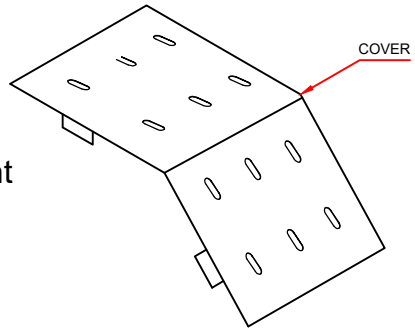


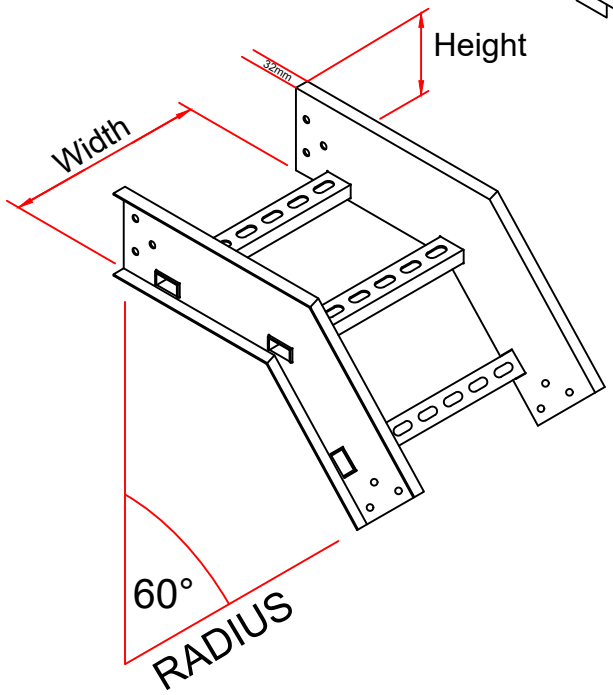


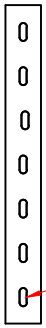

Obround 25X14

Rungs

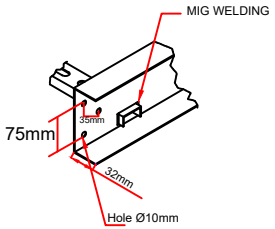

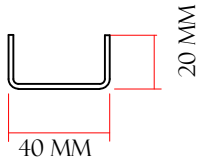

SIDE VIEW


CABLE LADDER 60° DEG (V) OUTSIDE RISER W COVER

SN	DIMENSION TABLE	QTY	DRAWN BY	EZELDIN	TITLE: CABLE LADDER 60° DEG OUTSIDE RISER W COVER	BONN METAL CONS. IND.
84	W=600mm, H =100mm , R= 600mm , T = 2mm W/COVER	14	CHECKED BY	AMIR KHAN		
			APPROVED BY	NASSER ANANI	CLIENT: KENT GAD	
			DATE	22-07-2026		
			REF NO. :		SEC ITEM NO:	DWRG. NO. : REV. 01
			CONSULTANT :			SHEET NO. : SCALE:NTS


BONN GROUP OF COMPANIES
Cable Management Systems


NOTE:-

MATERIAL HDG 2mm ALL flange 32 mm
Hot Dip Galvnaiztion 85 M without Epoxy
MIG WELDING
Cover Height 12mm

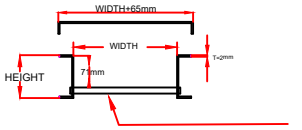


SECTION VIEW CHANNEL RUNG

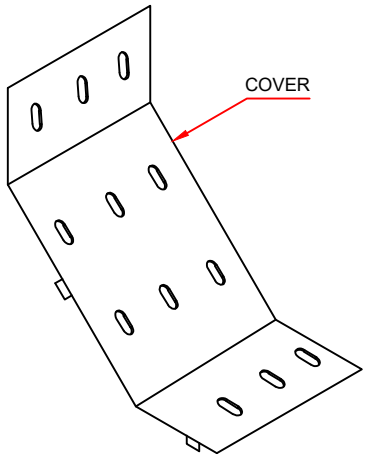


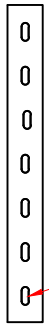


Obround 25X14

Rungs

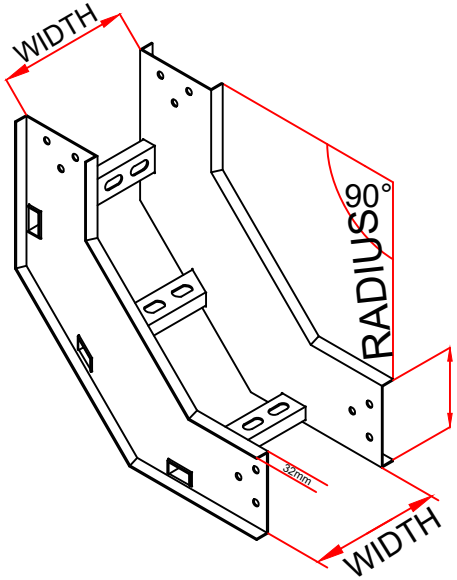

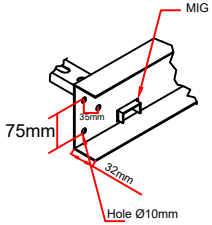

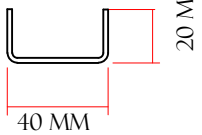

SIDE VIEW

CABLE LADDER BEND 90° INSIDE RISER W/COVER

SN	DIMENSION TABLE	QTY
85	W=300mm, H =100mm , R= 600mm , T = 2mm W/COVER	3
86	W=450mm, H =100mm , R= 600mm , T = 2mm ,W/COVER	3
87	W=600mm, H =100mm , R= 600mm , T = 2mm , W/COVER	9

DRAWN BY	EZELDIN
CHECKED BY	AMIR KHAN
APPROVED BY	NASSER ANANI
DATE	22-07-2026
REF NO. :	
CONSULTANT :	

TITLE: CABLE LADDER BEND 90° INSIDE RISER W/COVER

CLIENT: KENT GAD

SEC ITEM NO:

BONN METAL CONS. IND.


BONN GROUP OF COMPANIES
Cable Management Systems

DWRG. NO. :

REV. 01

SHEET NO. :


SCALE:NTS

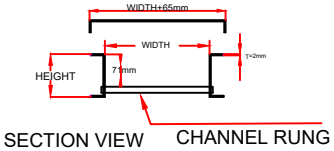



SECTION VIEW CHANNEL RUNG


NOTE:-


MATERIAL HDG 2mm ALL flange 32 mm
Hot Dip Galvnaiztion 85 M without Epoxy
MIG WELDING
Cover Height 12mm

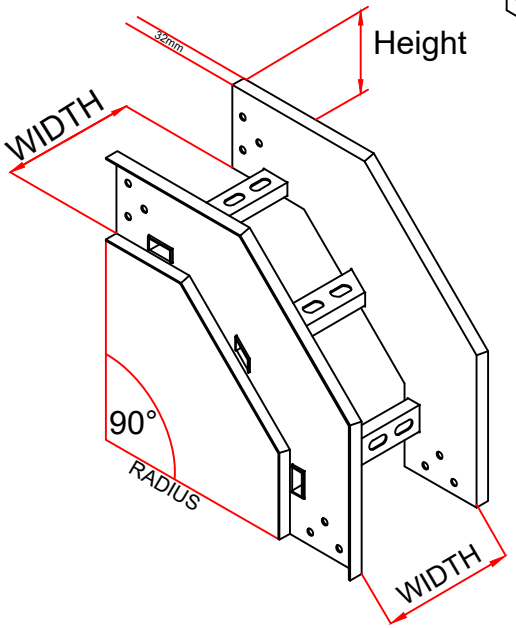

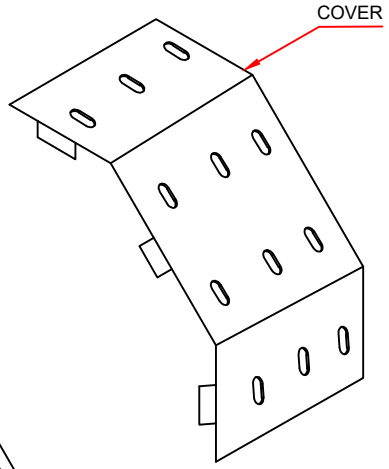

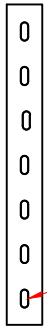

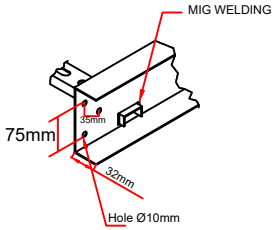

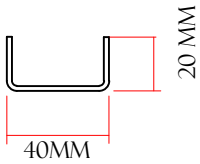

SIDE VIEW

CABLE LADDER BEND 90° OUTSIDE RISER W/COVER

SN	DIMENSION TABLE	QTY
88	W=300mm, H =100mm , R= 300mm , T = 2mm W/COVER	5
89	W=300mm, H =100mm , R= 600mm , T = 2mm ,W/COVER	7
90	W=450mm, H =100mm , R= 600mm , T = 2mm , W/COVER	5
91	W=600mm, H =100mm , R= 600mm , T = 2mm , W/COVER	7

DRAWN BY	EZELDIN
CHECKED BY	AMIR KHAN
APPROVED BY	NASSER ANANI
DATE	22-07-2026
REF NO. :	
CONSULTANT :	

TITLE: CABLE LADDER BEND 90° OUTSIDE RISER W/COVER

CLIENT: KENT GAD

SEC ITEM NO:

BONN METAL CONS. IND.


BONN GROUP OF COMPANIES
Cable Management Systems

DWRG. NO. :


REV. 01

SHEET NO. :

SCALE:NTS

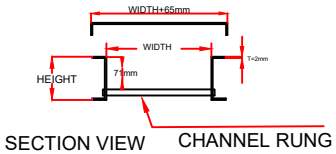


SECTION VIEW CHANNEL RUNG

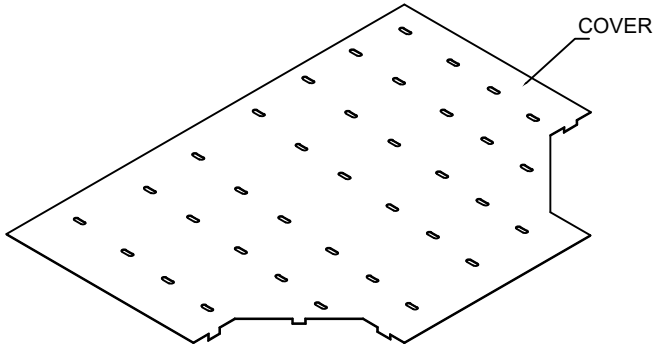


NOTE:-


MATERIAL HDG 2mm ALL flange 32 mm
Hot Dip Galvnaiztion 85 M without Epoxy
MIG WELDING
Cover Height 12mm

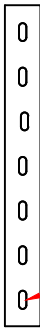


Obround 25X14

Rungs

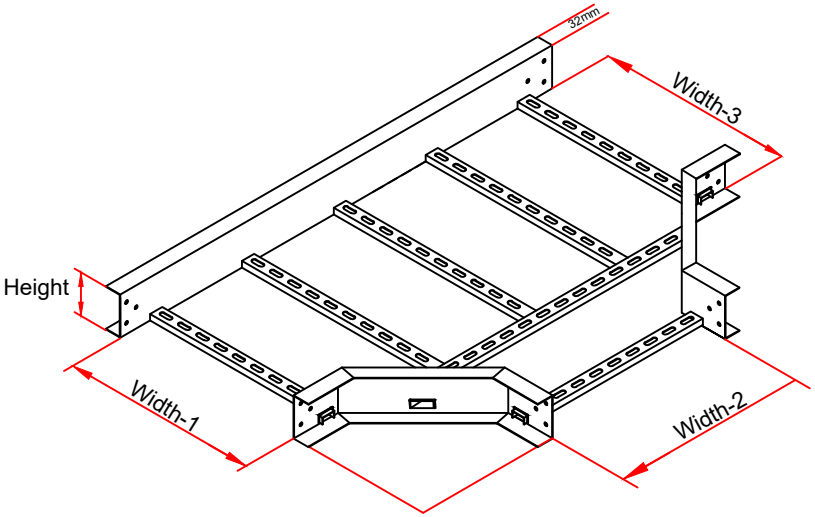

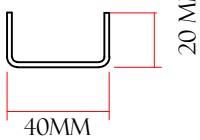

SIDE VIEW

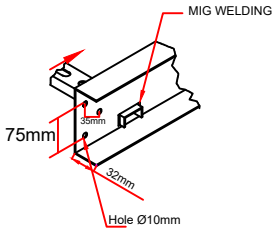

CABLE LADDER EQUAL TEE W/COVER

SN	DIMENSION TABLE	QTY
92	W=750mm, H =100mm , R= 600mm , T = 2mm W/COVER	2
93	W=750mm, H =100mm , R= 300mm , T = 2mm ,W/COVER	3

DRAWN BY	EZELDIN
CHECKED BY	AMIR KHAN
APPROVED BY	NASSER ANANI
DATE	22-07-2026
REF NO. :	
CONSULTANT :	

TITLE: CABLE LADDER EQUAL TEE W/COVER

CLIENT: KENT GAD

SEC ITEM NO:

BONN METAL CONS. IND.


BONN GROUP OF COMPANIES
Cable Management Systems

DWRG. NO. :


REV. 01

SHEET NO. :

SCALE:NTS

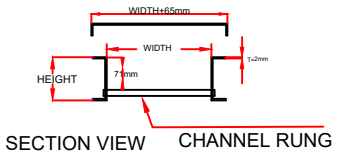


SECTION VIEW CHANNEL RUNG

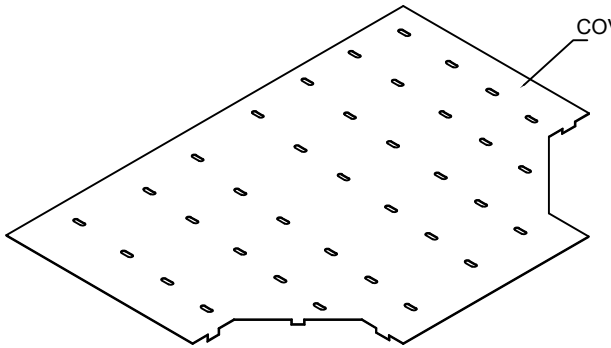


NOTE:-

MATERIAL HDG 2mm ALL flange 32 mm
Hot Dip Galvnaiztion 85 M without Epoxy
MIG WELDING
Cover Height 12mm

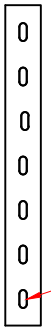



Obround 25X14

Rungs

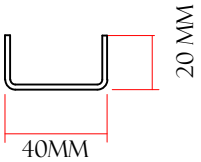

SIDE VIEW

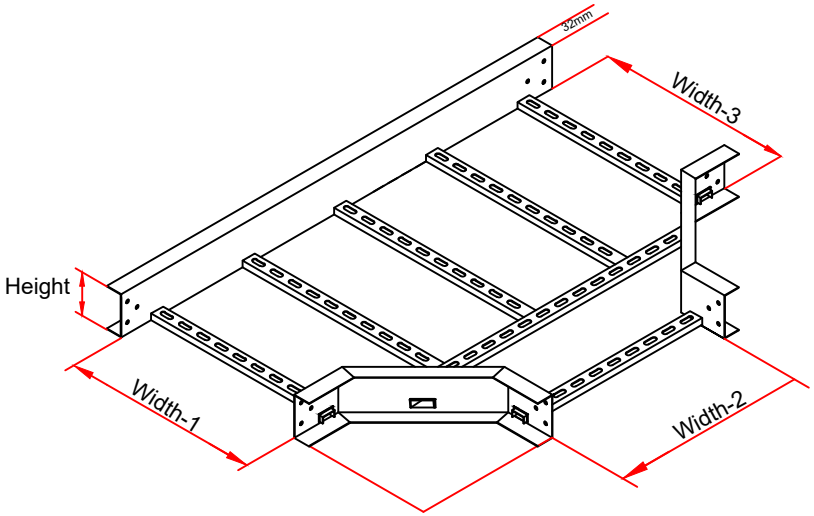

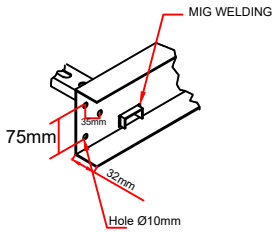

CABLE LADDER UNEQUAL TEE W/COVER

SN	DIMENSION TABLE	QTY
94	W1 =300mm, W2 =150mm,W3 =300mm,H =100mm ,R= 300mm ,T = 2mm W/COVER	3
95	W1 =450mm, W2 =150mm,W3 =450mm,H =100mm ,R= 300mm ,T = 2mm W/COVER	2

DRAWN BY	EZELDIN
CHECKED BY	AMIR KHAN
APPROVED BY	NASSER ANANI
DATE	22-07-2026
REF NO. :	
CONSULTANT :	

TITLE: CABLE LADDER EQUAL TEE W/COVER

CLIENT: KENT GAD

SEC ITEM NO:

BONN METAL CONS. IND.

BONN GROUP OF COMPANIES
Cable Management Systems

DWRG. NO. :


REV. 01

SHEET NO. :


SCALE:NTS


NOTE:-

MATERIAL HDG 2mm ALL flange 32 mm
Hot Dip Galvnaiztion 85 M without Epoxy
MIG WELDING
Cover Height 12mm

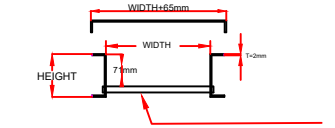


SECTION VIEW CHANNEL RUNG

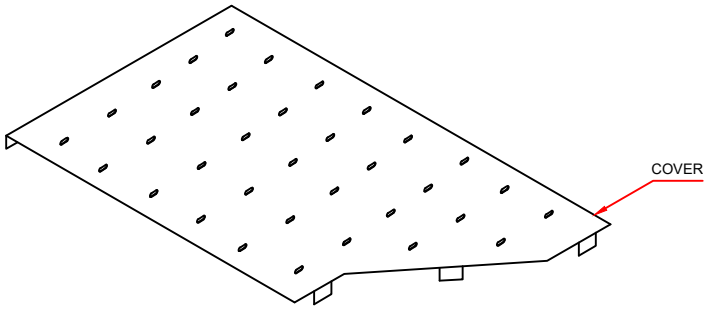

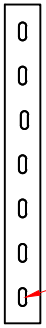



Obround 25X14

Rungs

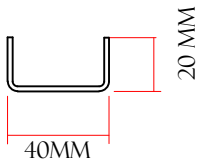

SIDE VIEW

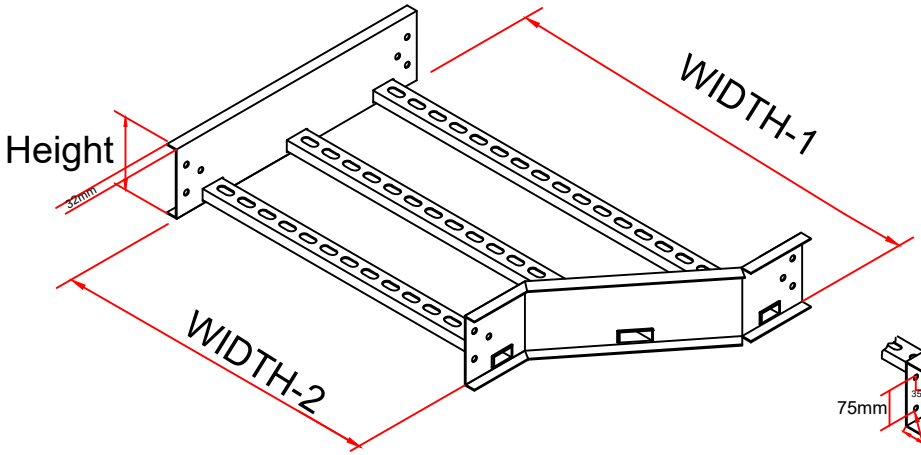

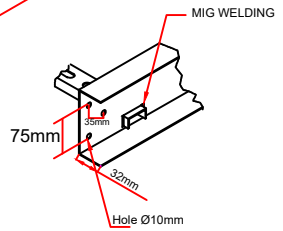


CABLE LADDER LEFT REDUCER W/COVER


SN	DIMENSION TABLE	QTY			
96	W1 =300mm, W2 =150mm , H =100mm ,T = 2mm W/COVER	4			

DRAWN BY	EZELDIN	TITLE: CABLE LADDER LEFT REDUCER W/COVER	BONN METAL CONS. IND.
CHECKED BY	AMIR KHAN		
APPROVED BY	NASSER ANANI	CLIENT: KENT GAD	
DATE	22-07-2026		
REF NO. :		SEC ITEM NO:	DWRG. NO. : / REV. 01
CONSULTANT :			SHEET NO. : / SCALE:NTS

BONN GROUP OF COMPANIES
Cable Management Systems

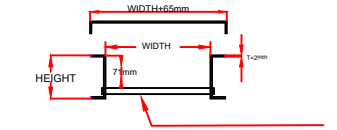


SECTION VIEW CHANNEL RUNG

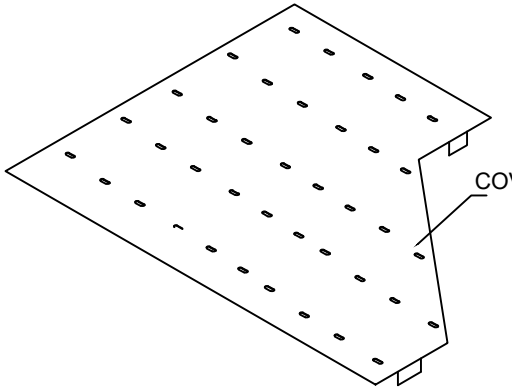


NOTE:-


MATERIAL HDG 2mm ALL flange 32 mm
Hot Dip Galvnaiztion 85 M without Epoxy
MIG WELDING
Cover Height 12mm

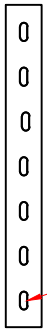


Obround 25X14

Rungs

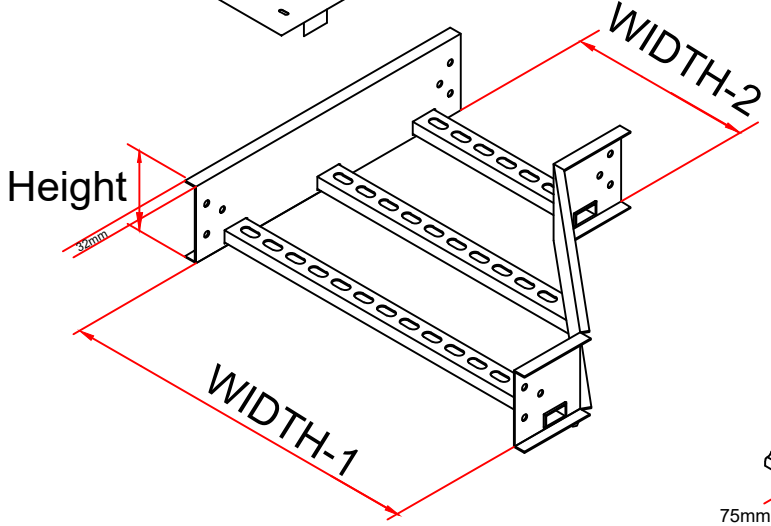

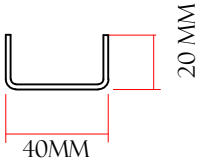

SIDE VIEW

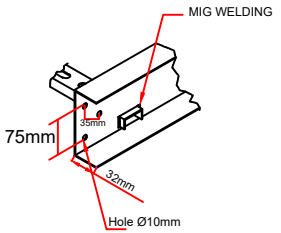

CABLE LADDER RIGHT REDUCER W/COVER

SN	DIMENSION TABLE	QTY
97	W1 =900mm, W2 =600mm , H =100mm ,T = 2mm W/COVER	2
98	W1 =600mm, W2 =300mm , H =100mm ,T = 2mm W/COVER	2
99	W1 =450mm, W2 =300mm , H =100mm ,T = 2mm W/COVER	2
100	W1 =300mm, W2 =150mm , H =100mm ,T = 2mm W/COVER	3

DRAWN BY	EZELDIN
CHECKED BY	AMIR KHAN
APPROVED BY	NASSER ANANI
DATE	22-07-2026
REF NO. :	
CONSULTANT :	

TITLE: CABLE LADDER RIGHT REDUCER W/COVER

CLIENT: KENT GAD

SEC ITEM NO:

BONN METAL CONS. IND.


BONN GROUP OF COMPANIES
Cable Management Systems

DWRG. NO. :

REV. 01


SHEET NO. :


SCALE:NTS

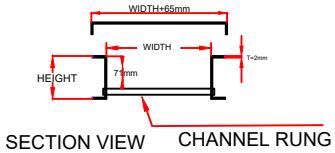



NOTE:-


MATERIAL HDG 2mm ALL flange 32 mm
Hot Dip Galvnaiztion 85 M without Epoxy
MIG WELDING
Cover Height 12mm

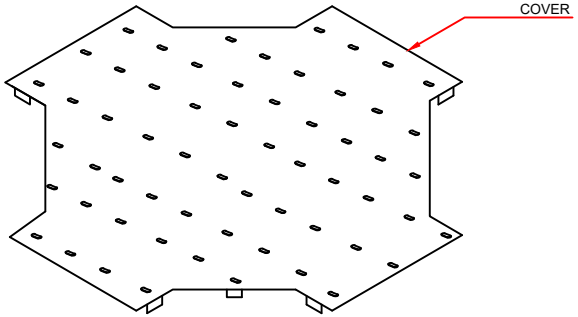

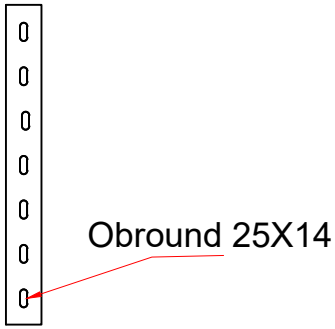

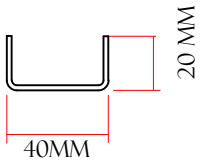

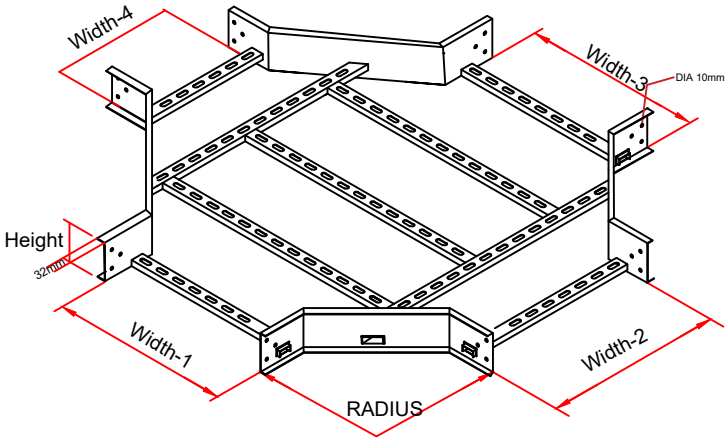


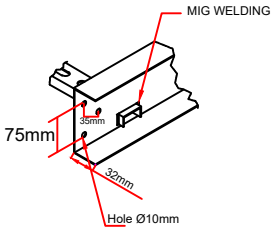

CABLE LADDER CROSS W/COVER


SN	DIMENSION TABLE	QTY	DRAWN BY	EZELDIN	TITLE: CABLE LADDER CROSS W/COVER	BONN METAL CONS. IND.
101	W = 600mm, H =100mm , R= 600mm , T = 2mm W/COVER	3	CHECKED BY	AMIR KHAN		
			APPROVED BY	NASSER ANANI	CLIENT: KENT GAD	
			DATE	22-07-2026		
			REF NO. :		SEC ITEM NO:	DWRG. NO. : / REV. 01
			CONSULTANT :			SHEET NO. : / SCALE:NTS

BONN GROUP OF COMPANIES
Cable Management Systems

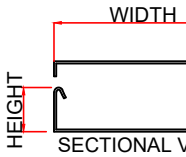

NOTE:-

MATERIAL HDG 2mm ALL flange inside 15 mm
Hot Dip Galvnaiztion 85 M without Epoxy
Cover Height 12mm

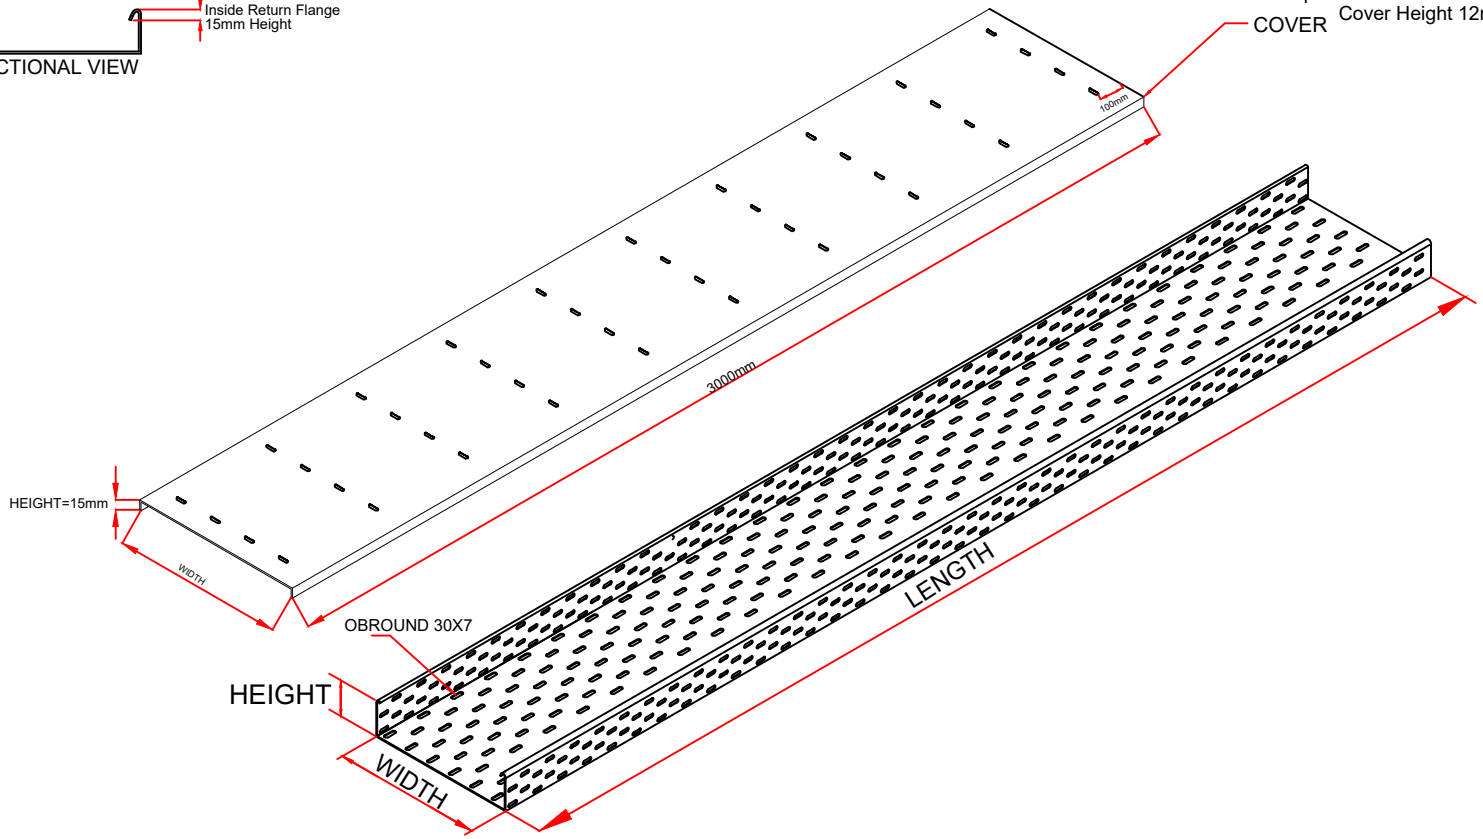

CABLE TRAY STRAIGHT LENGTH W/COVER

SN	DIMENSION TABLE	QTY
102	W=150mm, H =100mm , T = 2mm , W/COVER	1200
103	W=100mm, H =100mm , T = 2mm , W/COVER	345
104	W=50mm, H =50mm , T = 2mm , W/COVER	187

DRAWN BY	EZELDIN
CHECKED BY	AMIR KHAN
APPROVED BY	NASSER ANANI
DATE	22-07-2026
REF NO. :	
CONSULTANT :	

TITLE: CABLE TRAY STRAIGHT LENGTH W/COVER

CLIENT: KENT GAD

SEC ITEM NO:

BONN METAL CONS. IND.


BONN GROUP OF COMPANIES
Cable Management Systems

DWRG. NO. :

REV. 01


SHEET NO. :


SCALE:NTS

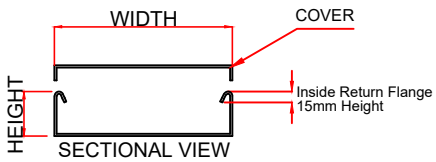

NOTE:-

MATERIAL HDG 2mm ALL flange inside 15 mm
Hot Dip Galvnaiztion 85 M without Epoxy
Cover Height 12mm

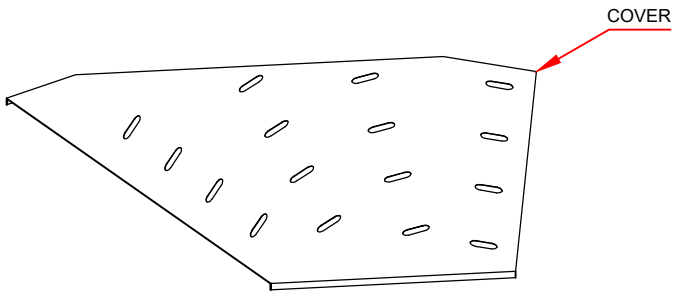

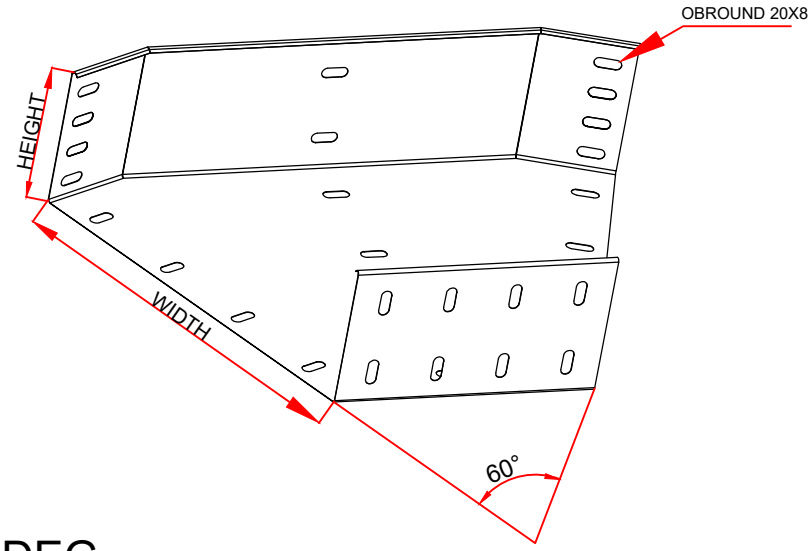

CABLE TRAY BEND 60DEG

SN	DIMENSION TABLE	QTY
105	W=150mm, H =100mm , R= 300mm , T = 2mm W/COVER	4

DRAWN BY	EZELDIN
CHECKED BY	AMIR KHAN
APPROVED BY	NASSER ANANI
DATE	22-07-2026
REF NO. :	
CONSULTANT :	

TITLE: CABLE TRAY BEND 60DEG

CLIENT: KENT GAD

SEC ITEM NO:

BONN METAL CONS. IND.


BONN GROUP OF COMPANIES
Cable Management Systems

DWRG. NO. :

REV. 01


SHEET NO. :

SCALE:NTS

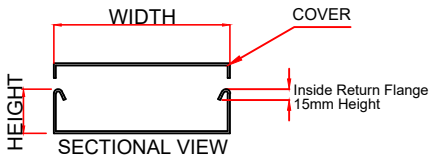

NOTE:-

MATERIAL HDG 2mm ALL flange inside 15 mm
Hot Dip Galvnaiztion 85 M without Epoxy
Cover Height 12mm

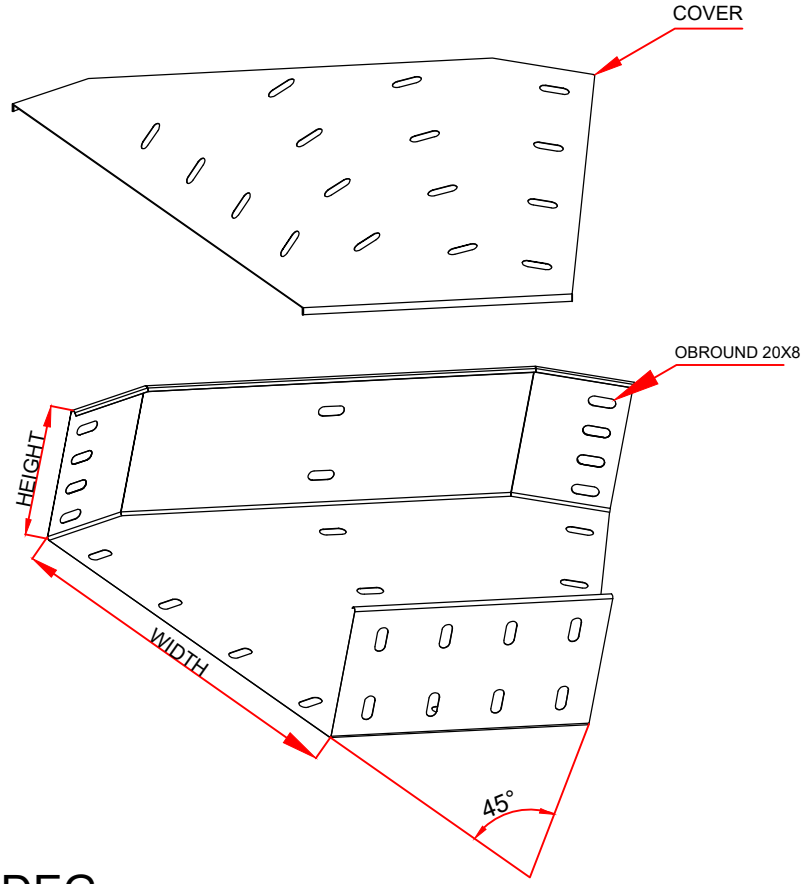

CABLE TRAY BEND 45DEG

SN	DIMENSION TABLE	QTY
106	W=150mm, H =100mm , R= 300mm , T = 2mm W/COVER	21

DRAWN BY	EZELDIN
CHECKED BY	AMIR KHAN
APPROVED BY	NASSER ANANI
DATE	22-07-2026
REF NO. :	
CONSULTANT :	

TITLE: CABLE TRAY BEND 45DEG

CLIENT: KENT GAD

SEC ITEM NO:

BONN METAL CONS. IND.


BONN GROUP OF COMPANIES
Cable Management Systems

DWRG. NO. :

REV. 01


SHEET NO. :


SCALE:NTS

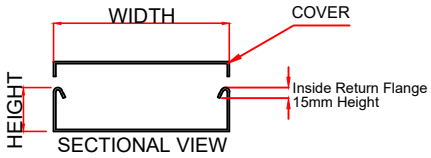

NOTE:-

MATERIAL HDG 2mm ALL flange inside 15 mm
Hot Dip Galvnaiztion 85 M without Epoxy
Cover Height 12mm

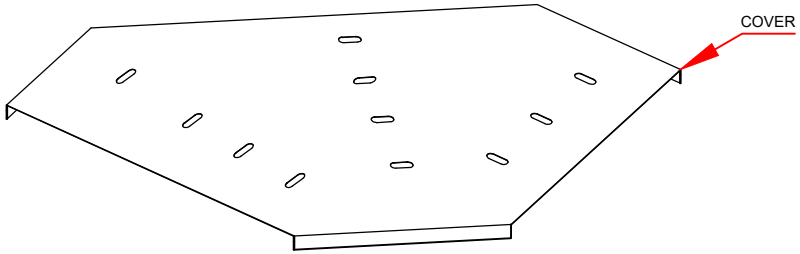

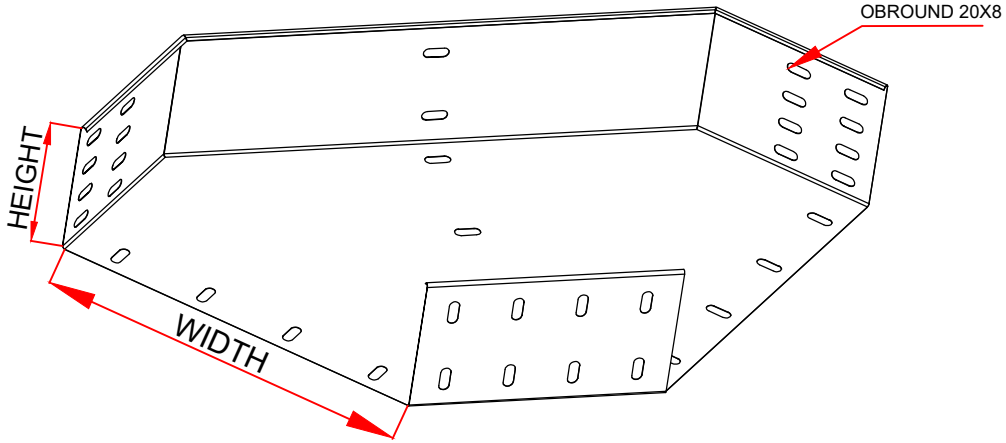

CABLE TRAY BEND 90DEG W/COVER

SN	DIMENSION TABLE	QTY
107	W=150mm, H =100mm , R= 300mm , T = 2mm W/COVER	135
108	W=100mm, H =100mm , R= 300mm , T = 2mm W/COVER	33

DRAWN BY	EZELDIN
CHECKED BY	AMIR KHAN
APPROVED BY	NASSER ANANI
DATE	22-07-2026
REF NO. :	
CONSULTANT :	

TITLE: CABLE TRAY BEND 90DEG W/COVER

CLIENT: KENT GAD

SEC ITEM NO:

BONN METAL CONS. IND.


BONN GROUP OF COMPANIES
Cable Management Systems

DWRG. NO. :

REV. 01


SHEET NO. :


SCALE:NTS

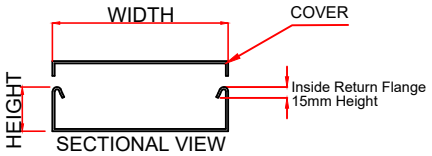

NOTE:-

MATERIAL HDG 2mm ALL flange inside 15 mm
Hot Dip Galvnaiztion 85 M without Epoxy
Cover Height 12mm

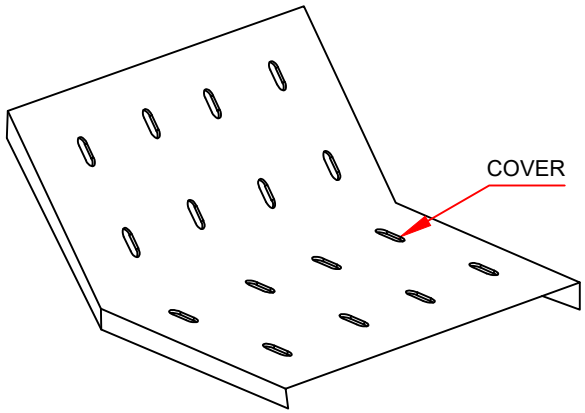

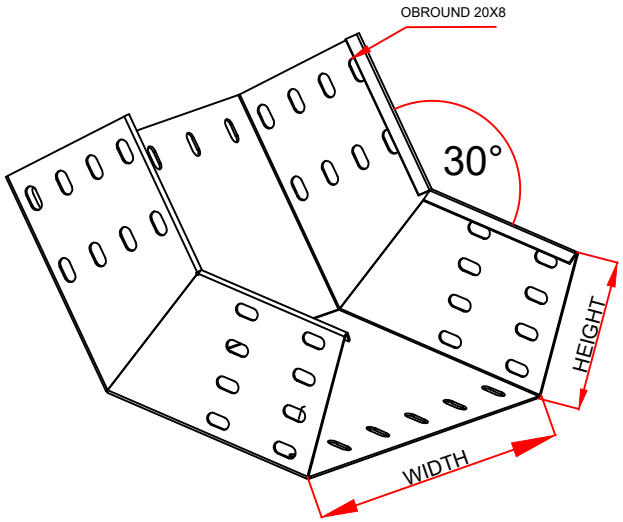

CABLE TRAY INSIDE RISER 30 DEG W/COVER

SN	DIMENSION TABLE	QTY
109	W=150mm, H =100mm , R= 300mm , T = 2mm W/COVER	4

DRAWN BY	EZELDIN
CHECKED BY	AMIR KHAN
APPROVED BY	NASSER ANANI
DATE	22-07-2026
REF NO. :	
CONSULTANT :	

TITLE: CABLE TRAY INSIDE RISER 30DEG W/COVER

CLIENT: KENT GAD

SEC ITEM NO:

BONN METAL CONS. IND.


BONN GROUP OF COMPANIES
Cable Management Systems

DWRG. NO. :

REV. 01


SHEET NO. :

SCALE:NTS

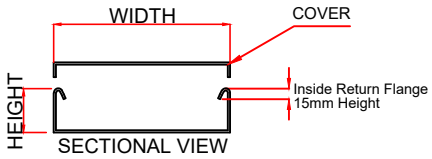

NOTE:-


MATERIAL HDG 2mm ALL flange inside 15 mm
Hot Dip Galvnaiztion 85 M without Epoxy
Cover Height 12mm

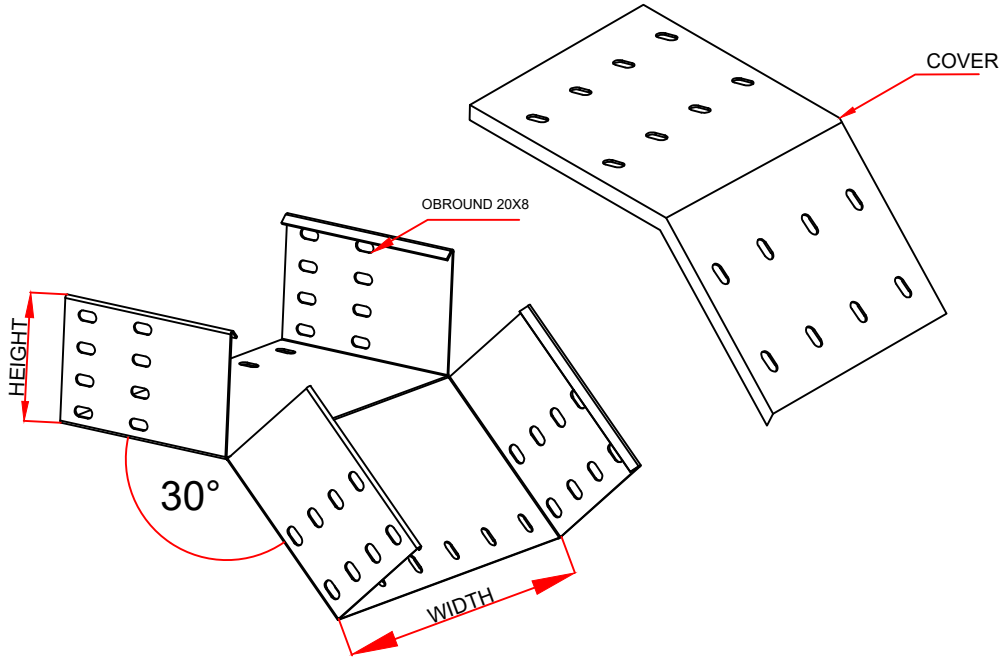

CABLE TRAY OUTSIDE RISER 30 DEG W/COVER


SN	DIMENSION TABLE	QTY	DRAWN BY	EZELDIN	TITLE: CABLE TRAY OUTSIDE RISER 30DEG W/COVER	BONN METAL CONS. IND.
110	W=150mm, H =100mm , R= 300mm , T = 2mm W/COVER	4	CHECKED BY	AMIR KHAN		
			APPROVED BY	NASSER ANANI	CLIENT: KENT GAD	
			DATE	22-07-2026		
			REF NO. :		SEC ITEM NO:	DWRG. NO. : REV. 01
			CONSULTANT :			SHEET NO. : SCALE:NTS


BONN GROUP OF COMPANIES
Cable Management Systems

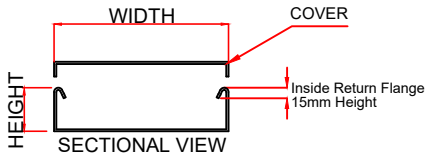

NOTE:-

MATERIAL HDG 2mm ALL flange inside 15 mm
Hot Dip Galvnaiztion 85 M without Epoxy
Cover Height 12mm

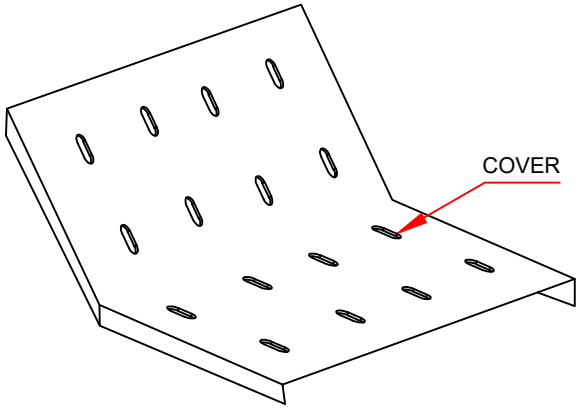

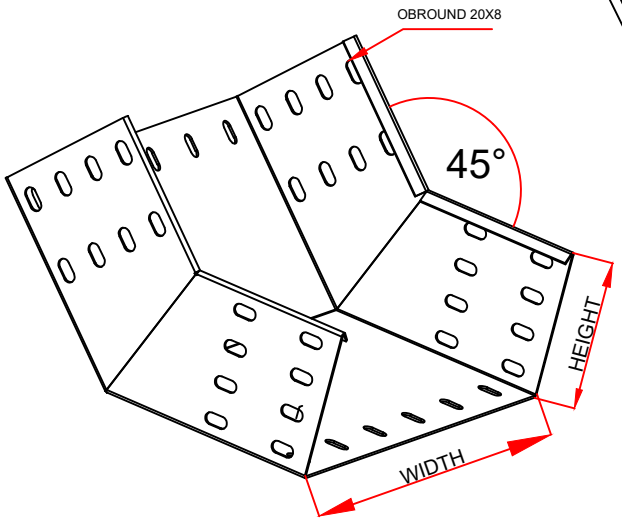

CABLE TRAY INSIDE RISER 45 DEG W/COVER

SN	DIMENSION TABLE	QTY
111	W=150mm, H =150mm , R= 300mm , T = 2mm W/COVER	25
112	W=150mm, H =100mm , R= 300mm , T = 2mm W/COVER	4

DRAWN BY	EZELDIN
CHECKED BY	AMIR KHAN
APPROVED BY	NASSER ANANI
DATE	22-07-2026
REF NO. :	
CONSULTANT :	

TITLE: CABLE TRAY INSIDE RISER 30DEG W/COVER

CLIENT: KENT GAD

SEC ITEM NO:

BONN METAL CONS. IND.


BONN GROUP OF COMPANIES
Cable Management Systems

DWRG. NO. :

REV. 01


SHEET NO. :

SCALE:NTS

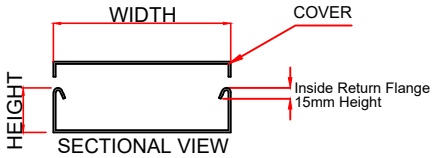

NOTE:-

MATERIAL HDG 2mm ALL flange inside 15 mm
Hot Dip Galvnaiztion 85 M without Epoxy
Cover Height 12mm

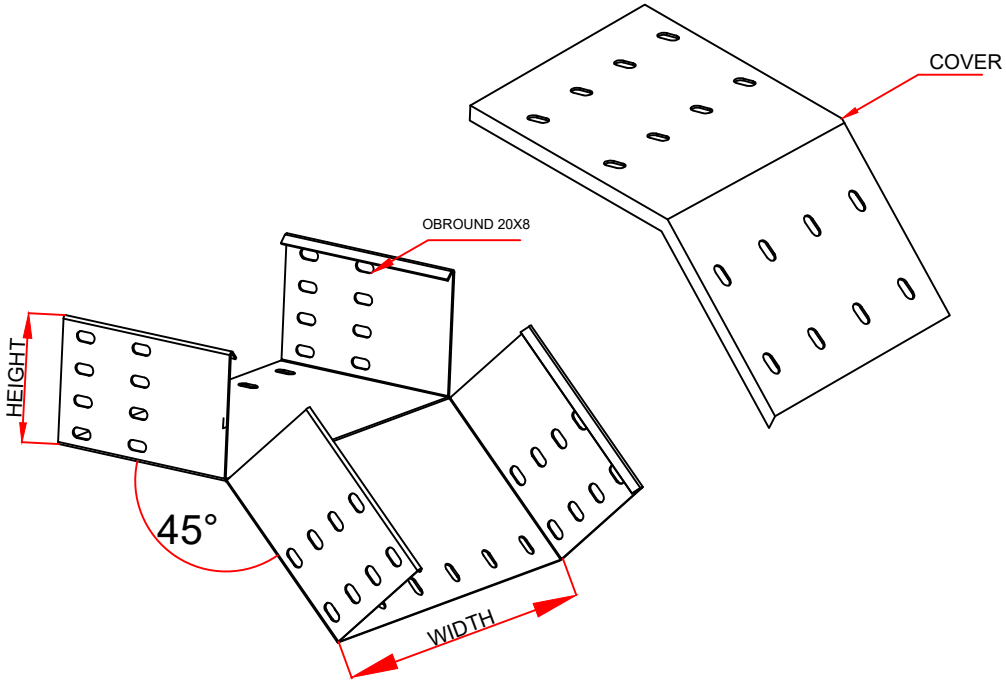

CABLE TRAY OUTSIDE RISER 30 DEG W/COVER


SN	DIMENSION TABLE	QTY
113	W=150mm, H =100mm , R= 300mm , T = 2mm W/COVER	25
114	W=100mm, H =100mm , R= 300mm , T = 2mm W/COVER	4

DRAWN BY	EZELDIN	TITLE: CABLE TRAY OUTSIDE RISER 30DEG W/COVER
CHECKED BY	AMIR KHAN	
APPROVED BY	NASSER ANANI	CLIENT: KENT GAD
DATE	22-07-2026	
REF NO. :		SEC ITEM NO:
CONSULTANT :		

BONN METAL CONS. IND.


BONN GROUP OF COMPANIES
Cable Management Systems


DWRG. NO. :		REV. 01
SHEET NO. :	SCALE:NTS	

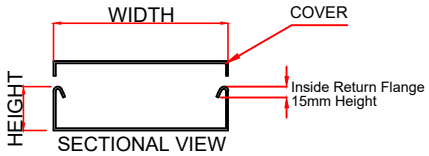

NOTE:-

MATERIAL HDG 2mm ALL flange inside 15 mm
Hot Dip Galvnaiztion 85 M without Epoxy
Cover Height 12mm

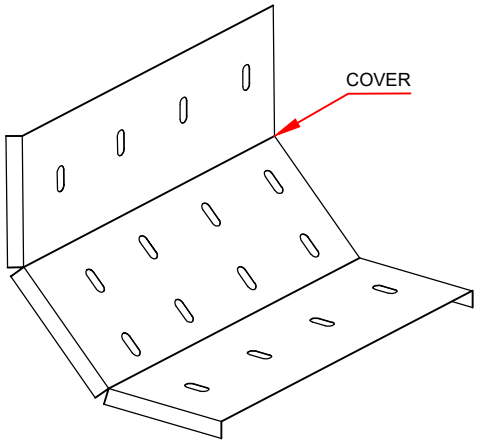

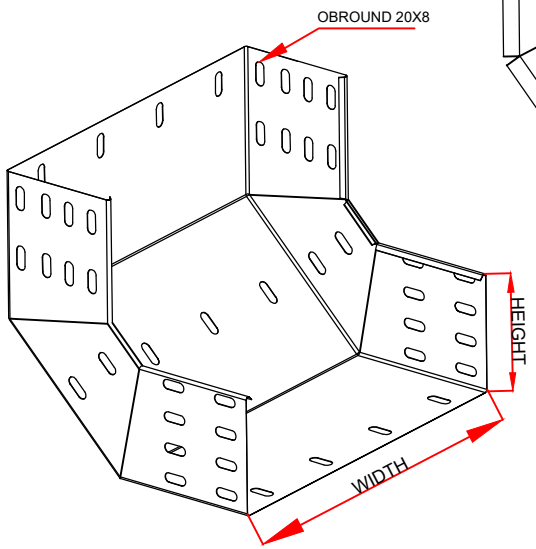

CABLE TRAY INSIDE RISER 90DEG

SN	DIMENSION TABLE	QTY
115	W=150mm, H =100mm , R= 300mm , T = 2mm W/COVER	32
116	W=100mm, H =100mm , R= 300mm , T = 2mm W/COVER	2

DRAWN BY	EZELDIN
CHECKED BY	AMIR KHAN
APPROVED BY	NASSER ANANI
DATE	22-07-2026
REF NO. :	
CONSULTANT :	

TITLE: CABLE TRAY INSIDE RISER 90DEG


CLIENT: KENT GAD


SEC ITEM NO:


BONN METAL CONS. IND.

BONN GROUP OF COMPANIES
Cable Management Systems

DWRG. NO. :		REV. 01
SHEET NO. :	SCALE:NTS	

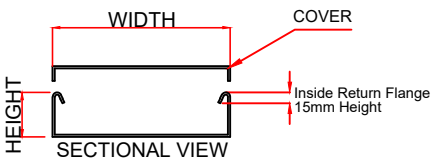

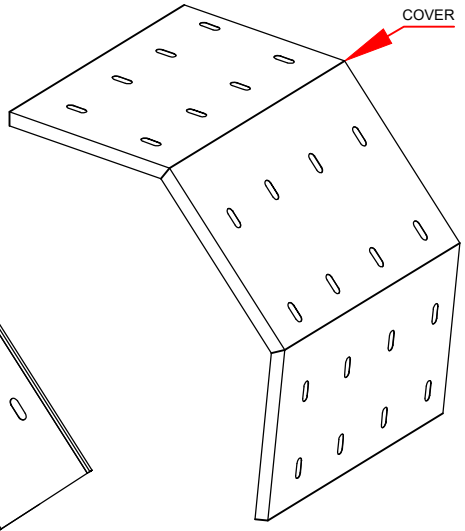

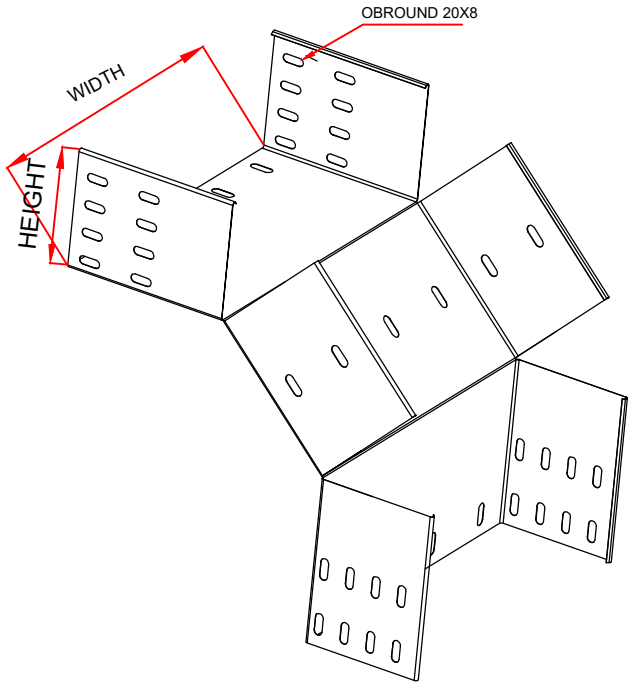

NOTE:-

MATERIAL HDG 2mm ALL flange inside 15 mm
Hot Dip Galvnaiztion 85 M without Epoxy
Cover Height 12mm

CABLE TRAY OUTSIDE RISER 90DEG

SN	DIMENSION TABLE	QTY
117	W=150mm, H =100mm , T = 2mm , W/COVER	45
118	W=100mm, H =100mm , T = 2mm , W/COVER	18

DRAWN BY	EZELDIN
CHECKED BY	AMIR KHAN
APPROVED BY	NASSER ANANI
DATE	22-07-2026
REF NO. :	
CONSULTANT :	

TITLE: CABLE TRAY OUTSIDE RISER 90DEG


CLIENT: KENT GAD

SEC ITEM NO:

BONN METAL CONS. IND.


BONN GROUP OF COMPANIES
Cable Management Systems


DWRG. NO. :		REV.
SHEET NO. :	SCALE:NTS	01

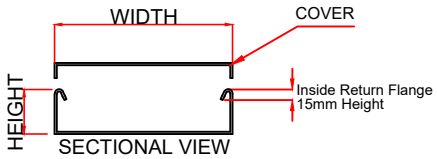

NOTE:-

MATERIAL HDG 2mm ALL flange inside 15 mm
Hot Dip Galvnaiztion 85 M without Epoxy
Cover Height 12mm

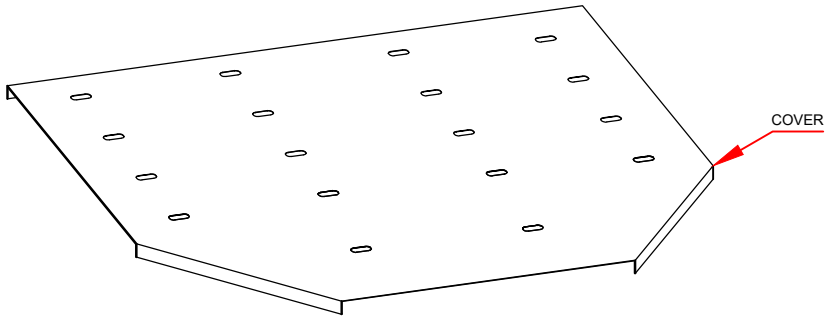

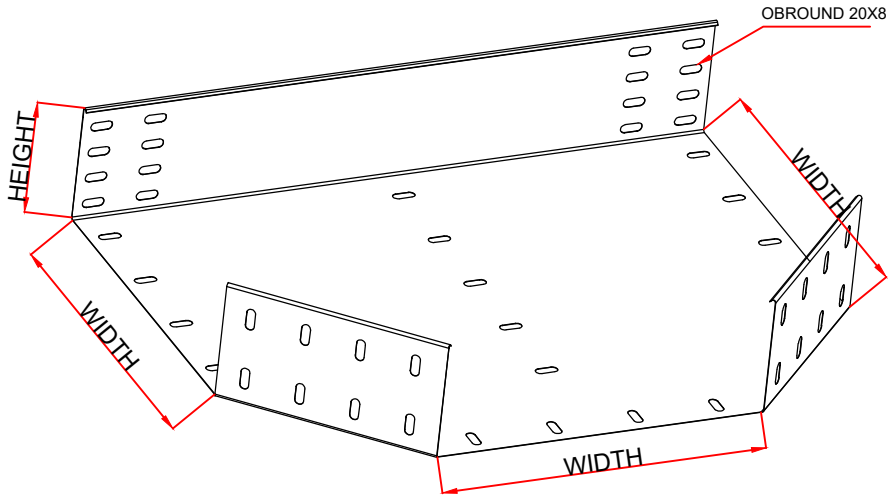

CABLE TRAY EQUAL TEE W/COVER

SN	DIMENSION TABLE	QTY
119	W=150mm, H =100mm , R= 300mm , T = 2mm W/COVER	1

DRAWN BY	EZELDIN
CHECKED BY	AMIR KHAN
APPROVED BY	NASSER ANANI
DATE	22-07-2026
REF NO. :	
CONSULTANT :	

TITLE: CABLE TRAY EQUAL TEE W/COVER

CLIENT: KENT GAD

SEC ITEM NO:

BONN METAL CONS. IND.


BONN GROUP OF COMPANIES
Cable Management Systems

DWRG. NO. :

REV. 01


SHEET NO. :

SCALE:NTS

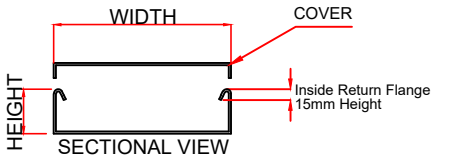

NOTE:-

MATERIAL HDG 2mm ALL flange inside 15 mm
Hot Dip Galvnaiztion 85 M without Epoxy
Cover Height 12mm

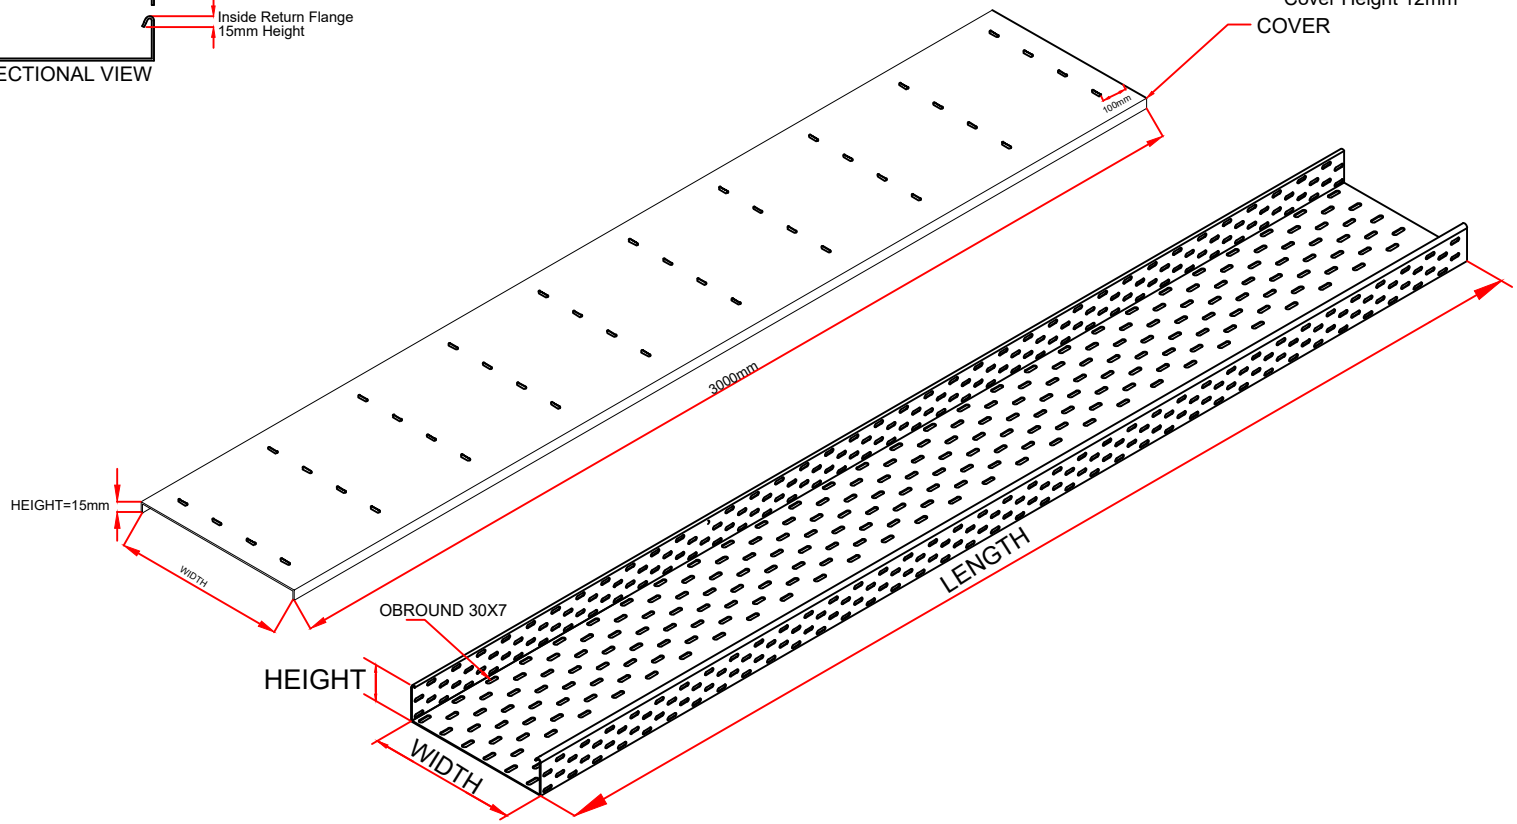

CABLE TRAY STRAIGHT LENGTH W/COVER

SN	DIMENSION TABLE	QTY
120	W=150mm, H =100mm , T = 2mm , W/COVER	960
121	W=100mm, H =100mm , T = 2mm , W/COVER	276
122	W=50mm, H =50mm , T = 2mm , W/COVER	150

DRAWN BY	EZELDIN
CHECKED BY	AMIR KHAN
APPROVED BY	NASSER ANANI
DATE	22-07-2026
REF NO. :	
CONSULTANT :	

TITLE: CABLE TRAY STRAIGHT LENGTH W/COVER

CLIENT: KENT GAD

SEC ITEM NO:

BONN METAL CONS. IND.


BONN GROUP OF COMPANIES
Cable Management Systems

DWRG. NO. :

REV. 01


SHEET NO. :

SCALE:NTS

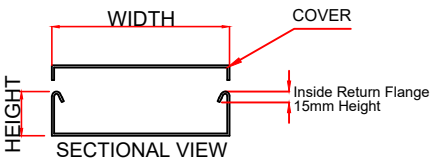

NOTE:-

MATERIAL HDG 2mm ALL flange inside 15 mm
Hot Dip Galvnaiztion 85 M without Epoxy
Cover Height 12mm

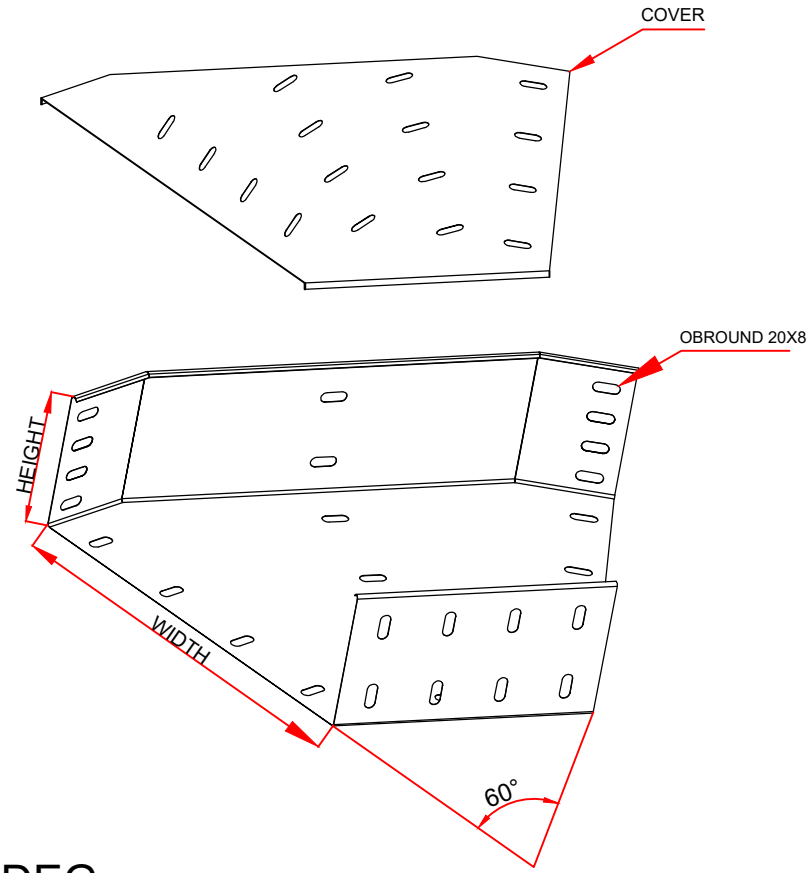

CABLE TRAY BEND 60DEG

SN	DIMENSION TABLE	QTY
123	W=150mm, H =100mm , R= 300mm , T = 2mm W/COVER	4

DRAWN BY	EZELDIN
CHECKED BY	AMIR KHAN
APPROVED BY	NASSER ANANI
DATE	22-07-2026
REF NO. :	
CONSULTANT :	

TITLE: CABLE TRAY BEND 60DEG

CLIENT: KENT GAD

SEC ITEM NO:

BONN METAL CONS. IND.


BONN GROUP OF COMPANIES
Cable Management Systems

DWRG. NO. :

REV. 01


SHEET NO. :


SCALE:NTS

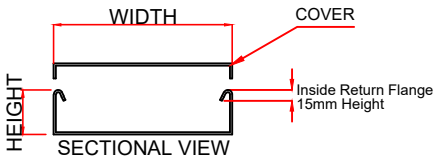

NOTE:-

MATERIAL HDG 2mm ALL flange inside 15 mm
Hot Dip Galvnaiztion 85 M without Epoxy
Cover Height 12mm

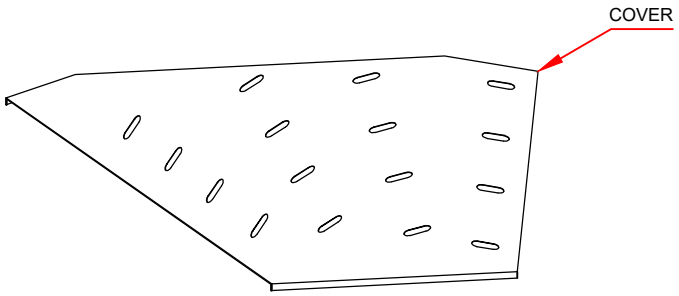

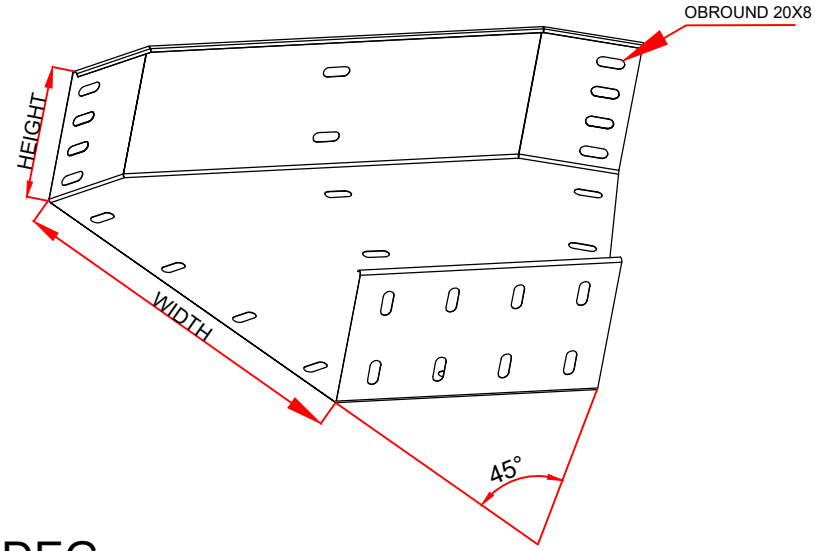

CABLE TRAY BEND 45DEG

SN	DIMENSION TABLE	QTY
124	W=150mm, H =100mm , R= 300mm , T = 2mm W/COVER	21

DRAWN BY	EZELDIN
CHECKED BY	AMIR KHAN
APPROVED BY	NASSER ANANI
DATE	22-07-2026
REF NO. :	
CONSULTANT :	

TITLE: CABLE TRAY BEND 45DEG

CLIENT: KENT GAD

SEC ITEM NO:

BONN METAL CONS. IND.


BONN GROUP OF COMPANIES
Cable Management Systems

DWRG. NO. :

REV. 01


SHEET NO. :


SCALE:NTS

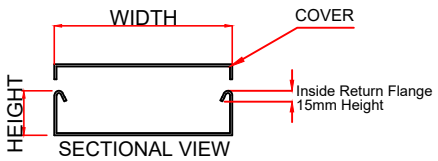

NOTE:-

MATERIAL HDG 2mm ALL flange inside 15 mm
Hot Dip Galvnaiztion 85 M without Epoxy
Cover Height 12mm

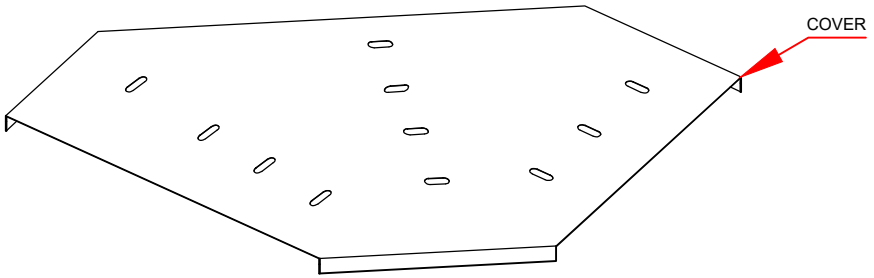

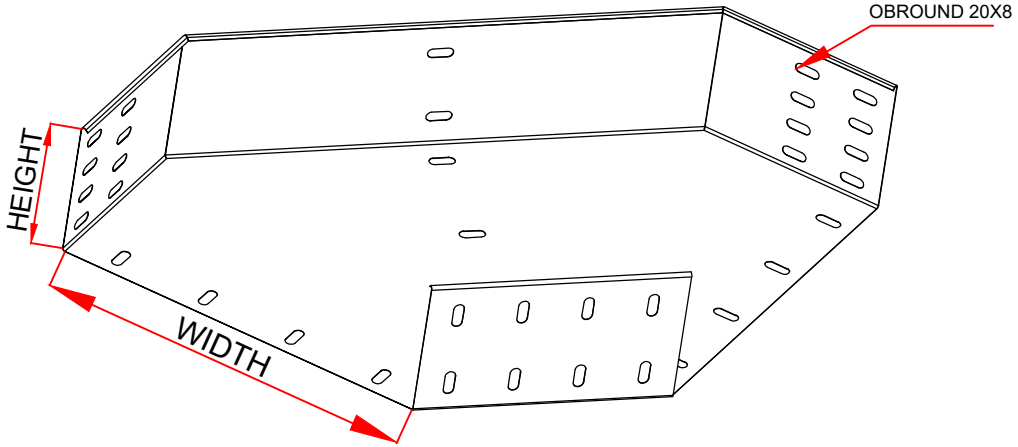

CABLE TRAY BEND 90DEG W/COVER

SN	DIMENSION TABLE	QTY
125	W=150mm, H =100mm , R= 300mm , T = 2mm W/COVER	135
126	W=100mm, H =100mm , R= 300mm , T = 2mm W/COVER	33

DRAWN BY	EZELDIN
CHECKED BY	AMIR KHAN
APPROVED BY	NASSER ANANI
DATE	22-07-2026
REF NO. :	
CONSULTANT :	

TITLE: CABLE TRAY BEND 90DEG W/COVER

CLIENT: KENT GAD

SEC ITEM NO:

BONN METAL CONS. IND.


BONN GROUP OF COMPANIES
Cable Management Systems

DWRG. NO. :

REV. 01


SHEET NO. :

SCALE:NTS

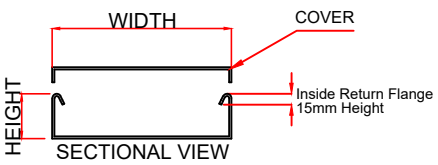

NOTE:-


MATERIAL HDG 2mm ALL flange inside 15 mm
Hot Dip Galvnaiztion 85 M without Epoxy
Cover Height 12mm

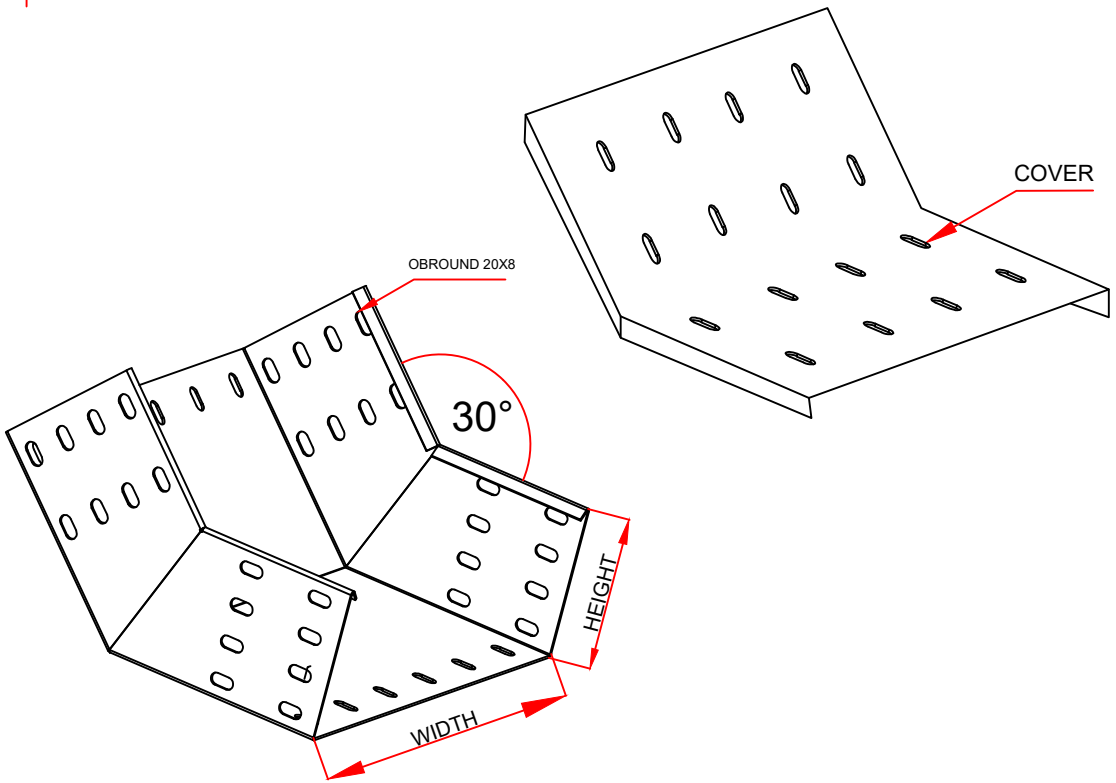

CABLE TRAY INSIDE RISER 30 DEG W/COVER


SN	DIMENSION TABLE	QTY	DRAWN BY	EZELDIN	TITLE: CABLE TRAY INSIDE RISER 30DEG W/COVER	BONN METAL CONS. IND.
127	W=150mm, H =100mm , R= 300mm , T = 2mm W/COVER	4	CHECKED BY	AMIR KHAN		
			APPROVED BY	NASSER ANANI	CLIENT: KENT GAD	
			DATE	22-07-2026		
			REF NO. :		SEC ITEM NO:	DWRG. NO. : / REV. 01
			CONSULTANT :			SHEET NO. : / SCALE:NTS


BONN GROUP OF COMPANIES
Cable Management Systems

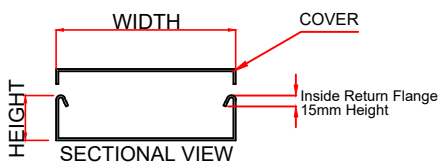

NOTE:-

MATERIAL HDG 2mm ALL flange inside 15 mm
Hot Dip Galvnaiztion 85 M without Epoxy
Cover Height 12mm

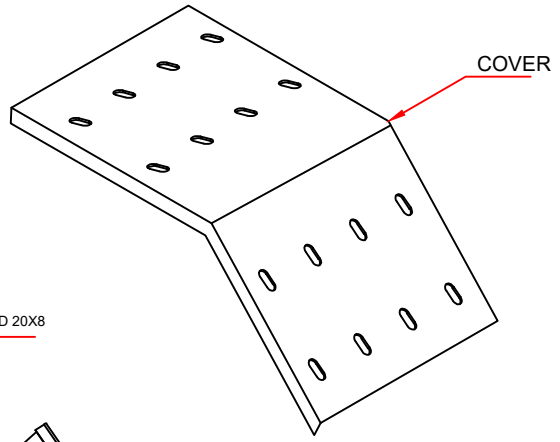


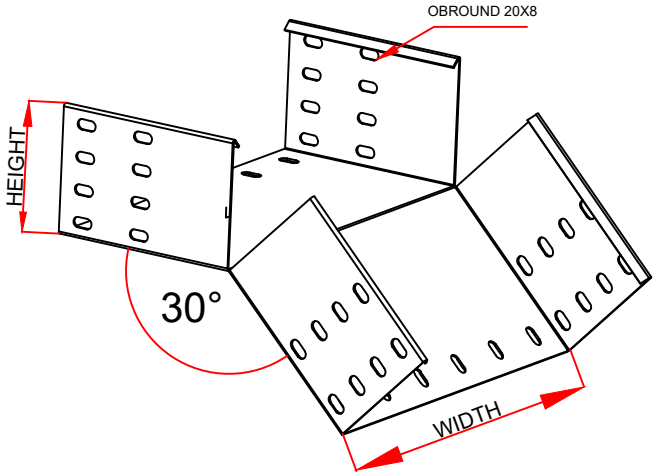

CABLE TRAY OUTSIDE RISER 30 DEG W/COVER


SN	DIMENSION TABLE	QTY	DRAWN BY	EZELDIN	TITLE: CABLE TRAY OUTSIDE RISER 30DEG W/COVER	BONN METAL CONS. IND.
128	W=150mm, H =100mm , R= 300mm , T = 2mm W/COVER	4	CHECKED BY	AMIR KHAN		
			APPROVED BY	NASSER ANANI	CLIENT: KENT GAD	
			DATE	22-07-2026		
			REF NO. :		SEC ITEM NO:	DWRG. NO. : REV. 01
			CONSULTANT :			SHEET NO. : SCALE:NTS


BONN GROUP OF COMPANIES
Cable Management Systems

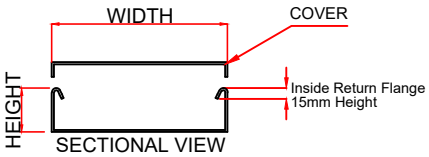

NOTE:-

MATERIAL HDG 2mm ALL flange inside 15 mm
Hot Dip Galvnaiztion 85 M without Epoxy
Cover Height 12mm

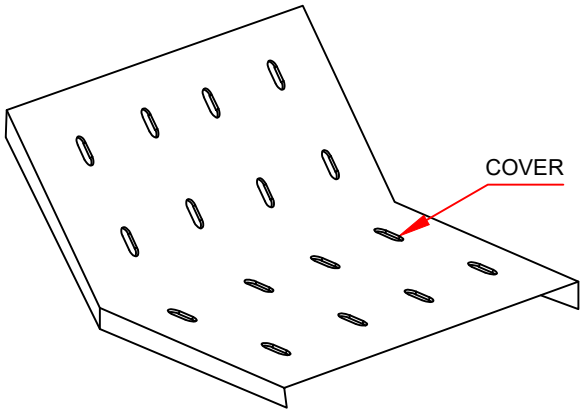

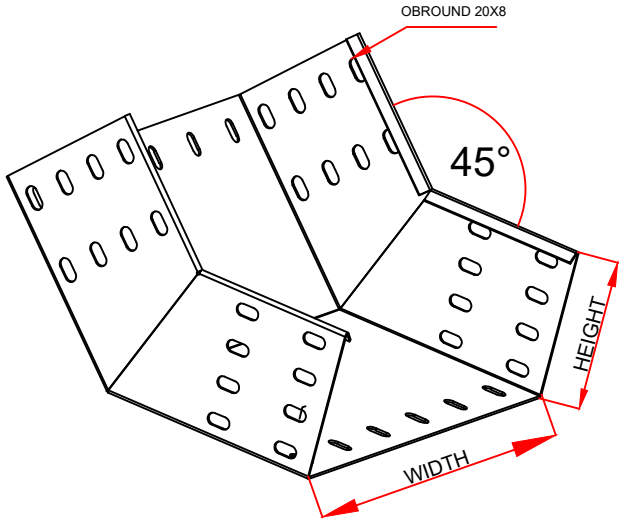

CABLE TRAY INSIDE RISER 45 DEG W/COVER

SN	DIMENSION TABLE	QTY
129	W=150mm, H =150mm , R= 300mm , T = 2mm W/COVER	25
130	W=150mm, H =100mm , R= 300mm , T = 2mm W/COVER	4

DRAWN BY	EZELDIN
CHECKED BY	AMIR KHAN
APPROVED BY	NASSER ANANI
DATE	22-07-2026
REF NO. :	
CONSULTANT :	

TITLE: CABLE TRAY INSIDE RISER 30DEG W/COVER

CLIENT: KENT GAD

SEC ITEM NO:

BONN METAL CONS. IND.


BONN GROUP OF COMPANIES
Cable Management Systems

DWRG. NO. :

REV. 01


SHEET NO. :

SCALE:NTS

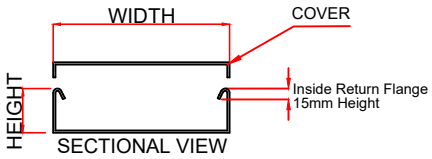

NOTE:-

MATERIAL HDG 2mm ALL flange inside 15 mm
Hot Dip Galvnaiztion 85 M without Epoxy
Cover Height 12mm

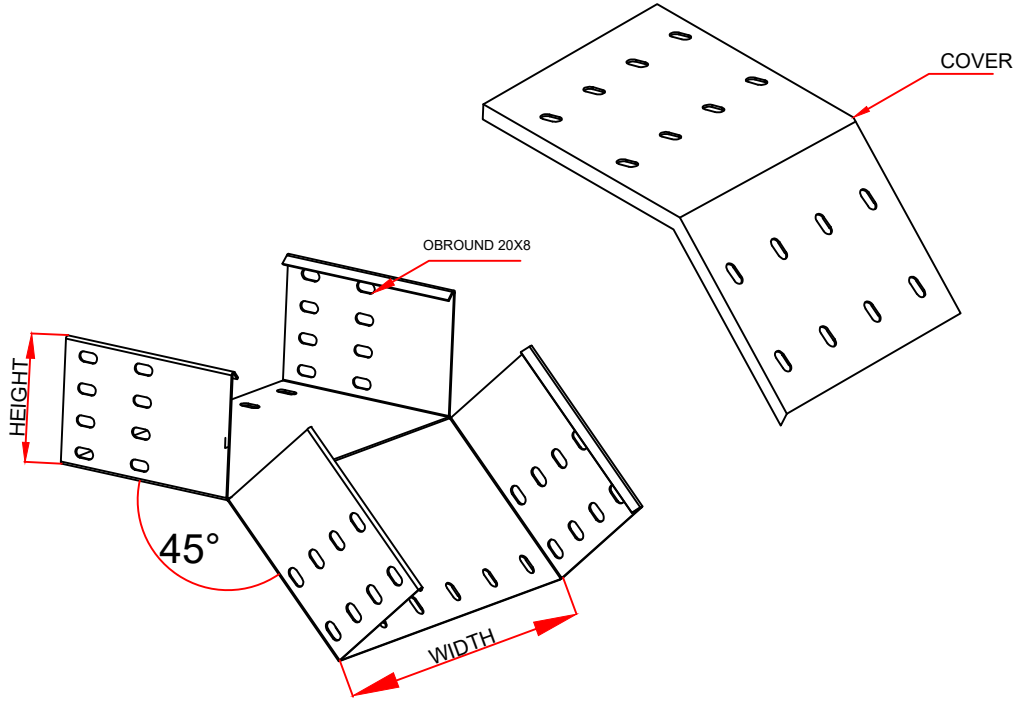

CABLE TRAY OUTSIDE RISER 30 DEG W/COVER

SN	DIMENSION TABLE	QTY
131	W=150mm, H =100mm , R= 300mm , T = 2mm W/COVER	25
132	W=100mm, H =100mm , R= 300mm , T = 2mm W/COVER	4

DRAWN BY	EZELDIN
CHECKED BY	AMIR KHAN
APPROVED BY	NASSER ANANI
DATE	22-07-2026
REF NO. :	
CONSULTANT :	

TITLE: CABLE TRAY OUTSIDE RISER 30DEG W/COVER

CLIENT: KENT GAD

SEC ITEM NO:

BONN METAL CONS. IND.


BONN GROUP OF COMPANIES
Cable Management Systems

DWRG. NO. :

REV. 01


SHEET NO. :


SCALE:NTS

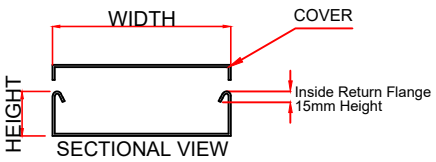

NOTE:-

MATERIAL HDG 2mm ALL flange inside 15 mm
Hot Dip Galvnaiztion 85 M without Epoxy
Cover Height 12mm

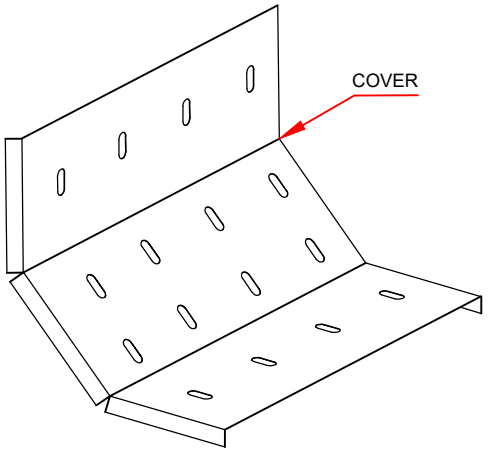

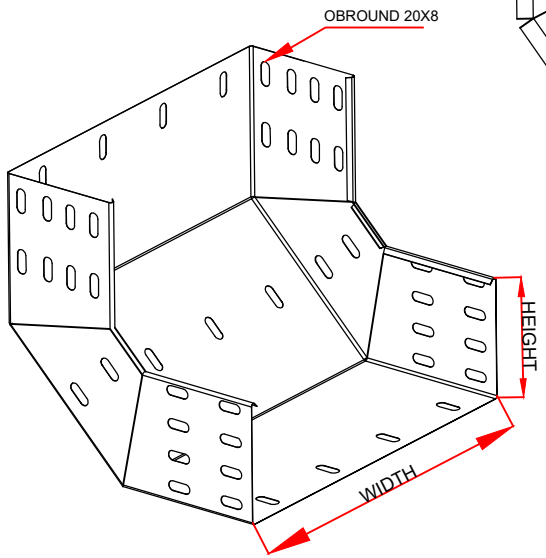

CABLE TRAY INSIDE RISER 90DEG

SN	DIMENSION TABLE	QTY
133	W=150mm, H =100mm , R= 300mm , T = 2mm W/COVER	32
134	W=100mm, H =100mm , R= 300mm , T = 2mm W/COVER	2

DRAWN BY	EZELDIN
CHECKED BY	AMIR KHAN
APPROVED BY	NASSER ANANI
DATE	22-07-2026
REF NO. :	
CONSULTANT :	

TITLE: CABLE TRAY INSIDE RISER 90DEG

CLIENT: KENT GAD

SEC ITEM NO:


BONN METAL CONS. IND.

BONN GROUP OF COMPANIES
Cable Management Systems

DWRG. NO. :		REV.
SHEET NO. :	SCALE:NTS	01

NOTE:-

MATERIAL HDG 2mm ALL flange inside 15 mm
Hot Dip Galvnaiztion 85 M without Epoxy
Cover Height 12mm

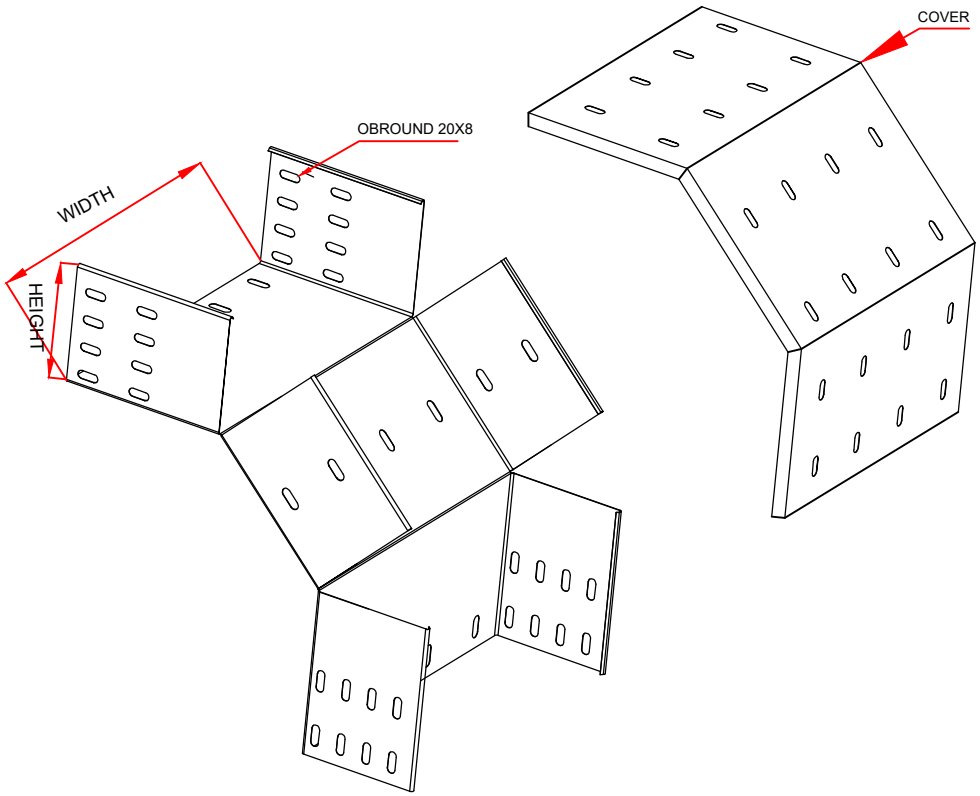

CABLE TRAY OUTSIDE RISER 90DEG

SN	DIMENSION TABLE	QTY
135	W=150mm, H =100mm , R= 300mm , T = 2mm W/COVER	45
136	W=100mm, H =100mm , R= 300mm , T = 2mm W/COVER	18

DRAWN BY	EZELDIN
CHECKED BY	AMIR KHAN
APPROVED BY	NASSER ANANI
DATE	22-07-2026
REF NO. :	
CONSULTANT :	

TITLE: CABLE TRAY OUTSIDE RISER 90DEG

CLIENT: KENT GAD

SEC ITEM NO:

BONN METAL CONS. IND.

BONN GROUP OF COMPANIES
Cable Management Systems

DWRG. NO. :


REV. 01

SHEET NO. :

SCALE:NTS

NOTE:-

MATERIAL HDG 2mm ALL flange inside 15 mm
Hot Dip Galvnaiztion 85 M without Epoxy
Cover Height 12mm

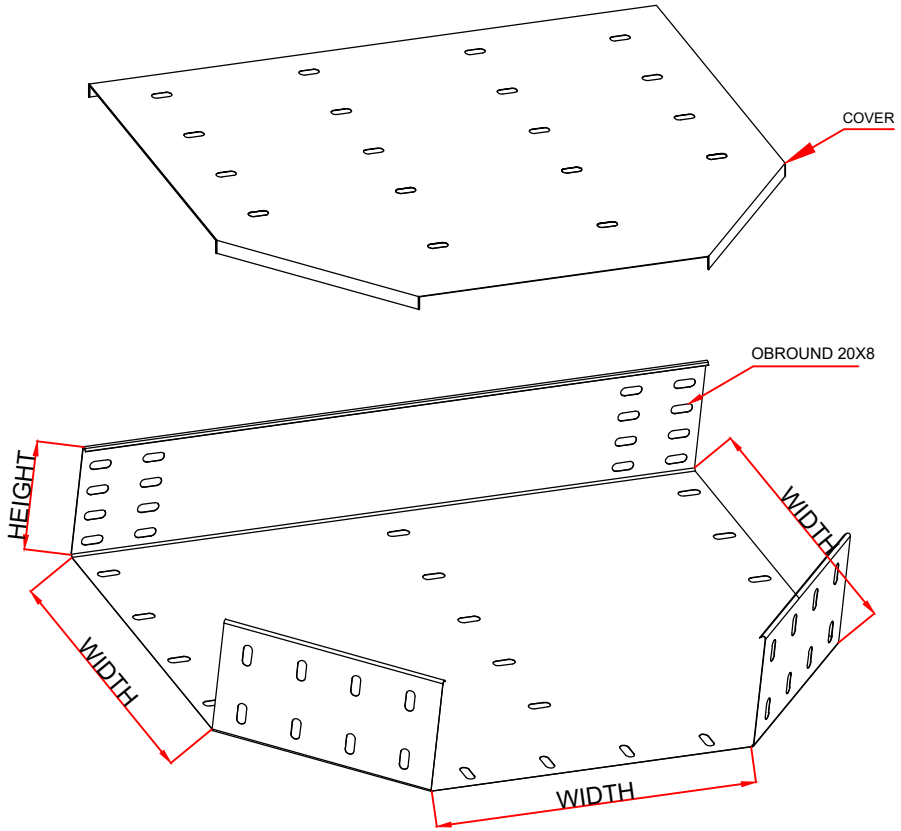

CABLE TRAY EQUAL TEE W/COVER

SN	DIMENSION TABLE	QTY
137	W=150mm, H =100mm , R= 300mm , T = 2mm W/COVER	1

DRAWN BY	EZELDIN
CHECKED BY	AMIR KHAN
APPROVED BY	NASSER ANANI
DATE	22-07-2026
REF NO. :	
CONSULTANT :	

TITLE: CABLE TRAY EQUAL TEE W/COVER

CLIENT: KENT GAD

SEC ITEM NO:

BONN METAL CONS. IND.

BONN GROUP OF COMPANIES
Cable Management Systems

DWRG. NO. :


REV. 01


SHEET NO. :

SCALE:NTS


NOTE:-

MATERIAL HDG 2mm HARDWARES SS316
Hot Dip Galvnaiztion 85 M without Epoxy

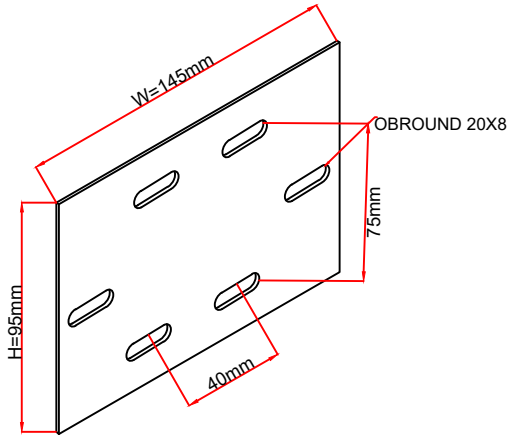


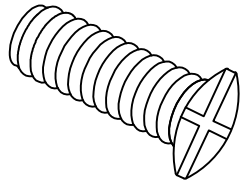

ROOFING BOLT
M6X16

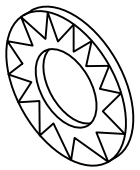

Washers M6

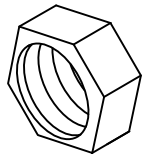

Nuts M6


CABLE LADDER COUPLER


SN	DIMENSION TABLE	QTY	DRAWN BY	EZELDIN	TITLE: CABLE LADDER COUPLER	BONN METAL CONS. IND.
138	W=145mm, H =95mm , T = 2mm	3096	CHECKED BY	AMIR KHAN		
			APPROVED BY	NASSER ANANI	CLIENT: KENT GAD	
			DATE	22-07-2026		
			REF NO. :		SEC ITEM NO:	DWRG. NO. : REV. 01
			CONSULTANT :			SHEET NO. : SCALE:NTS

BONN GROUP OF COMPANIES
Cable Management Systems


NOTE:-

MATERIAL HDG 2mm HARDWARES SS316
Hot Dip Galvnaiztion 85 M without Epoxy

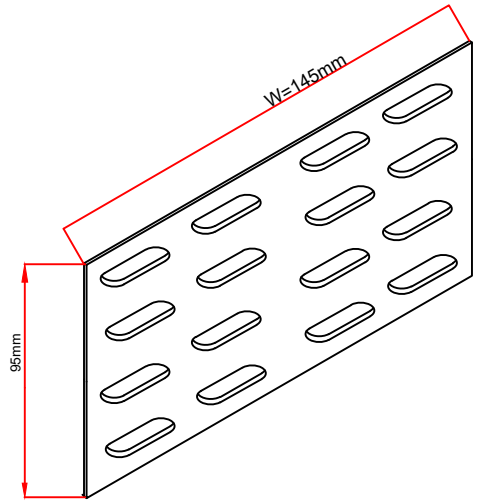


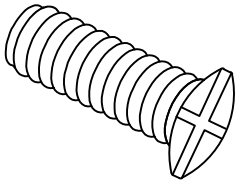

ROOFING BOLT
M6X16

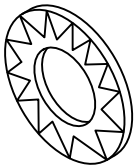

Washers M6

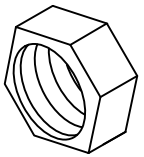

Nuts M6

CABLE TRAY EXPANSION COUPLER

SN	DIMENSION TABLE	QTY
139	W=145mm, H =95mm , T = 2mm	48

DRAWN BY	EZELDIN
CHECKED BY	AMIR KHAN
APPROVED BY	NASSER ANANI
DATE	22-07-2026
REF NO. :	
CONSULTANT :	

TITLE: CABLE TRAY EXPANSION COUPLER

CLIENT: KENT GAD

SEC ITEM NO:

BONN METAL CONS. IND.

BONN GROUP OF COMPANIES
Cable Management Systems

DWRG. NO. :


REV. 01


SHEET NO. :

SCALE:NTS


NOTE:-

MATERIAL HDG 2mm HARDWARES SS316
Hot Dip Galvnaiztion 85 M without Epoxy

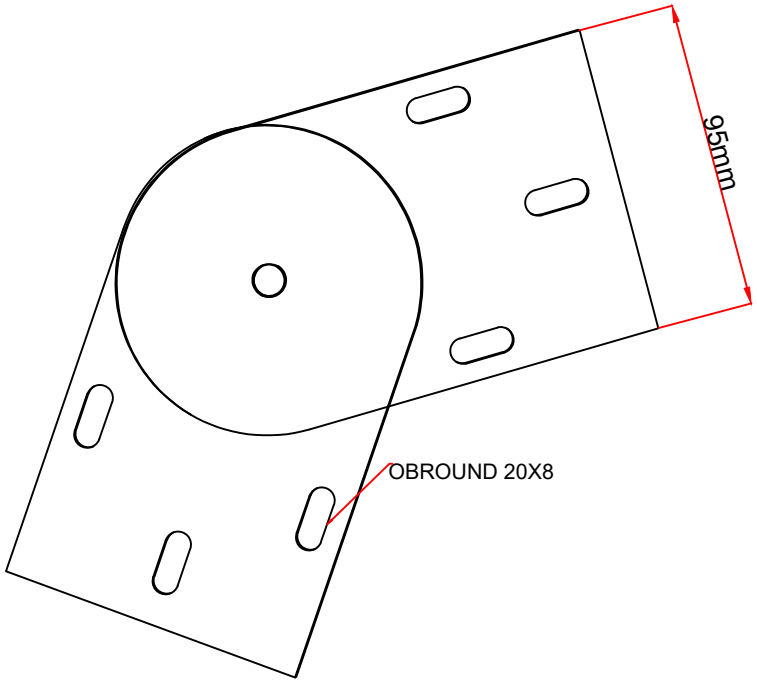


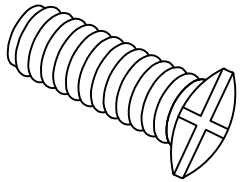

ROOFING BOLT
M6X16

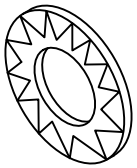

Washers M6

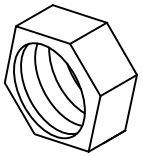

Nuts M6

CABLE LADDER ADJUSTABLE VERTICAL COUPLER

SN	DIMENSION TABLE	QTY
140	H=100mm & T=2.0mm	156

DRAWN BY	EZELDIN
CHECKED BY	AMIR KHAN
APPROVED BY	NASSER ANANI
DATE	22-07-2026
REF NO. :	
CONSULTANT :	

TITLE: CABLE LADDER ADJUSTABLE VERTICAL COUPLER

CLIENT: KENT GAD

SEC ITEM NO:

BONN METAL CONS. IND.

BONN GROUP OF COMPANIES
Cable Management Systems

DWRG. NO. :


SHEET NO. :


SCALE:NTS

REV. 01


NOTE:-

MATERIAL HDG 2mm HARDWARES SS316
Hot Dip Galvnaiztion 85 M without Epoxy

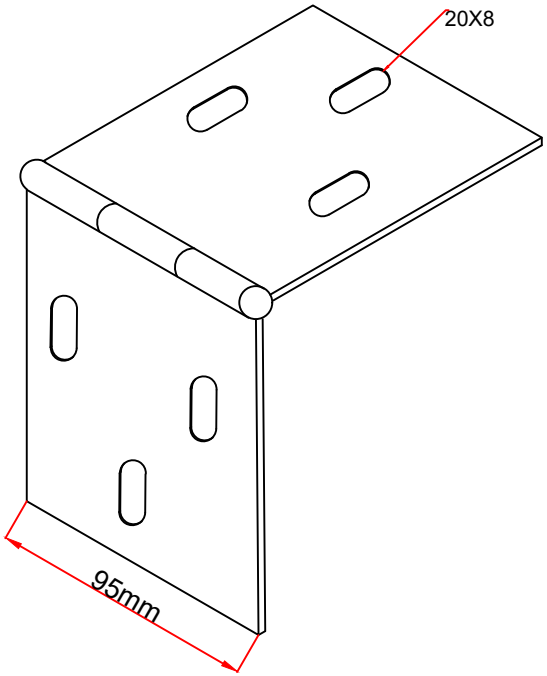


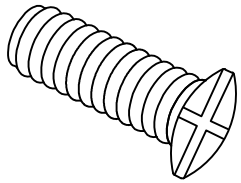

ROOFING BOLT
M6X16

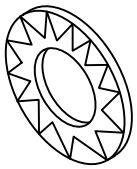

Washers M6

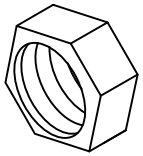

Nuts M6

CABLE LADDER ADJUSTABLE HORIZONTAL COUPLER

SN	DIMENSION TABLE	QTY
141	H=100mm & T=2.0mm	156

DRAWN BY	EZELDIN
CHECKED BY	AMIR KHAN
APPROVED BY	NASSER ANANI
DATE	22-07-2026
REF NO. :	
CONSULTANT :	

TITLE: CABLE LADDER ADJUSTABLE HORIZONTAL COUPLER

CLIENT: KENT GAD

SEC ITEM NO:

BONN METAL CONS. IND.

BONN GROUP OF COMPANIES
Cable Management Systems

DWRG. NO. :


REV. 01

SHEET NO. :


SCALE:NTS

NOTE:-


MATERIAL HDG 2mm HARDWARES SS316
Hot Dip Galvnaiztion 85 M without Epoxy

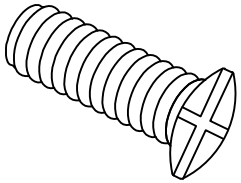


ROOFING BOLT
M8X30

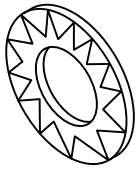

Washers M8

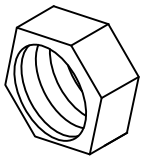

Nuts M8

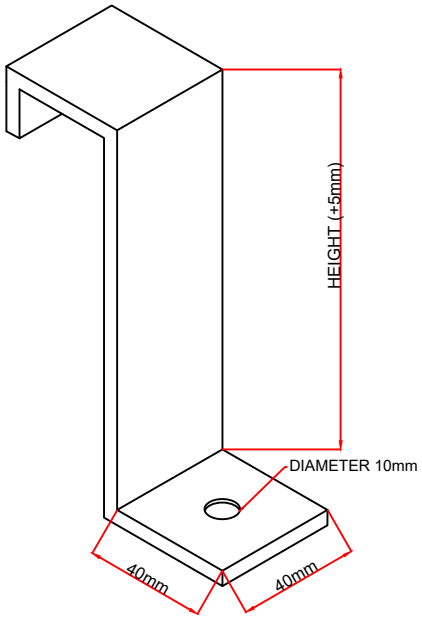


CABLE LADDER HOLD DOWN CLAMP

SN	DIMENSION TABLE	QTY	DRAWN BY	EZELDIN	TITLE: CABLE LADDER HOLD DOWN CLAMP	BONN METAL CONS. IND.
142	W=40mm, H =100+5mm , T = 2mm	4740	CHECKED BY	AMIR KHAN		
			APPROVED BY	NASSER ANANI	CLIENT: KENT GAD	
			DATE	22-07-2026		
			REF NO. :		SEC ITEM NO:	DWRG. NO. : REV. 01
			CONSULTANT :			SHEET NO. : SCALE:NTS

BONN GROUP OF COMPANIES
Cable Management Systems

NOTE:-

MATERIAL HDG 2mm & HARDWARES SS316
Hot Dip Galvnaiztion 85 M without Epoxy

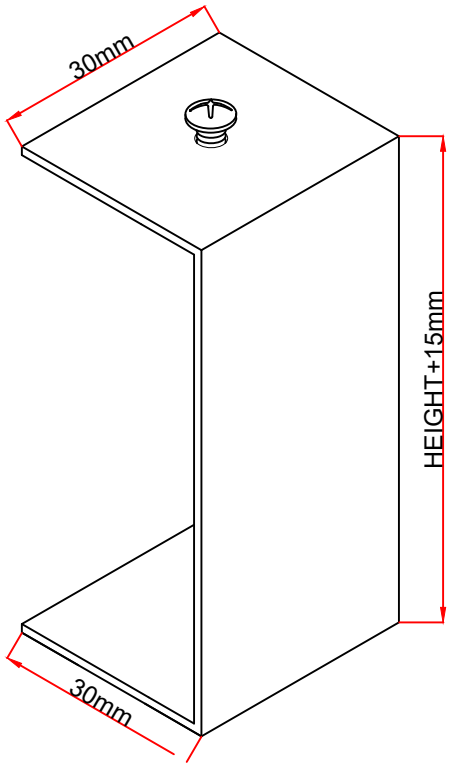


Cable Ladder cover Holding Clamps

SN	DIMENSION TABLE	QTY	DRAWN BY	EZELDIN	TITLE: Cable Ladder cover Holding Clamps	BONN METAL CONS. IND.
143	W=30mm, H =100+5mm , T = 2mm	5700	CHECKED BY	AMIR KHAN		
			APPROVED BY	NASSER ANANI	CLIENT: KENT GAD	
			DATE	22-07-2026		
			REF NO. :		SEC ITEM NO:	DWRG. NO. : / REV. 01
			CONSULTANT :			SHEET NO. : / SCALE:NTS


BONN GROUP OF COMPANIES
Cable Management Systems

NOTE:-


MATERIAL HDG 2mm & HARDWARES SS316
Hot Dip Galvnaiztion 85 M without Epoxy

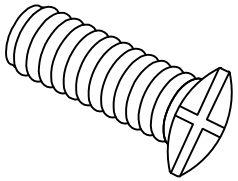


ROOFING BOLT
M6X16

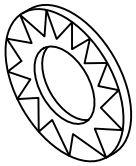

Washers M6

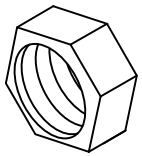

Nuts M6

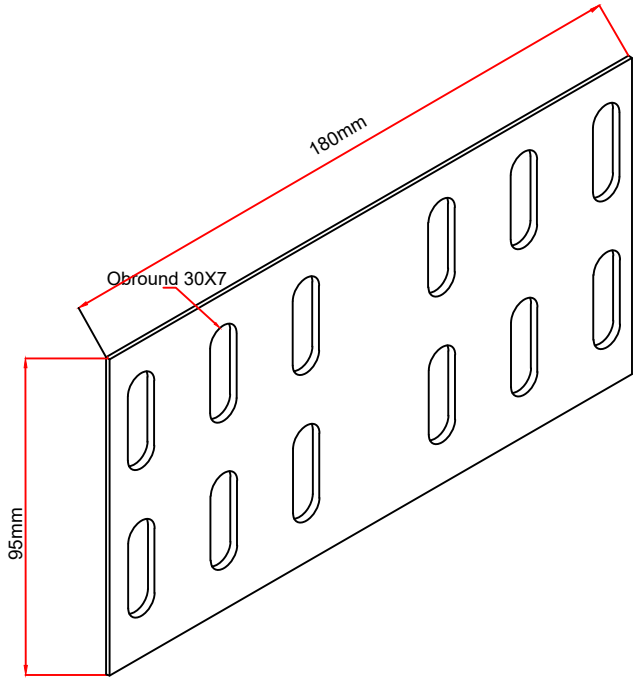

CABLE TRAY STRAIGHT COUPLER

SN	DIMENSION TABLE	QTY
144	W=180mm, H =95mm , T = 2mm	3798

DRAWN BY	EZELDIN
CHECKED BY	AMIR KHAN
APPROVED BY	NASSER ANANI
DATE	22-07-2026
REF NO. :	
CONSULTANT :	

TITLE: CABLE TRAY STRAIGHT COUPLER

CLIENT: KENT GAD

SEC ITEM NO:

BONN METAL CONS. IND.

BONN GROUP OF COMPANIES
Cable Management Systems

DWRG. NO. :


REV. 01

SHEET NO. :


SCALE:NTS


NOTE:-

MATERIAL HDG 2mm HARDWARES SS316
Hot Dip Galvnaiztion 85 M without Epoxy

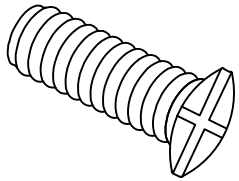


ROOFING BOLT
M6X16

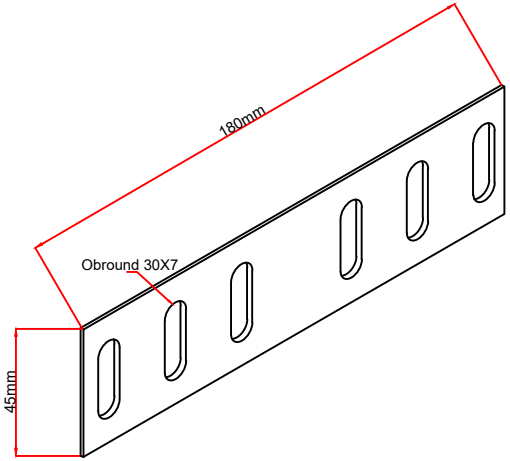

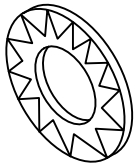

Washers M6

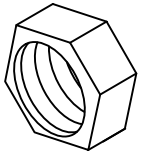

Nuts M6

CABLE TRAY STRAIGHT COUPLER

SN	DIMENSION TABLE	QTY
145	W=180mm, H =45mm , T = 2mm	378

DRAWN BY	EZELDIN
CHECKED BY	AMIR KHAN
APPROVED BY	NASSER ANANI
DATE	22-07-2026
REF NO. :	
CONSULTANT :	

TITLE: CABLE TRAY STRAIGHT COUPLER

CLIENT: KENT GAD

SEC ITEM NO:

BONN METAL CONS. IND.

BONN GROUP OF COMPANIES
Cable Management Systems

DWRG. NO. :


REV. 01

SHEET NO. :


SCALE:NTS

NOTE:-


MATERIAL HDG 2mm HARDWARES SS316
Hot Dip Galvnaiztion 85 M without Epoxy

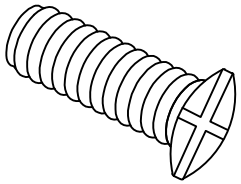


ROOFING BOLT
M6X16

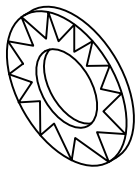

Washers M6

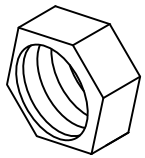

Nuts M6

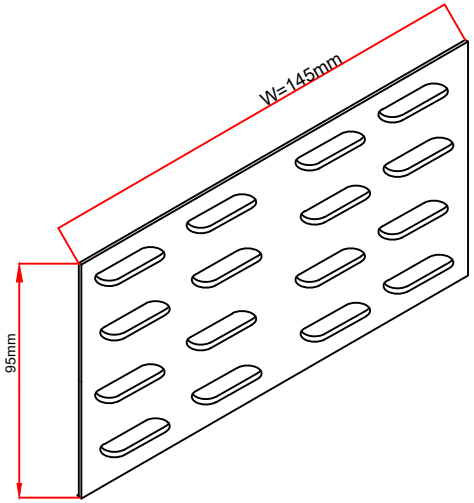

CABLE TRAY EXPANSION COUPLER

SN	DIMENSION TABLE	QTY
146	W=145mm, H =95mm , T = 2mm	60

DRAWN BY	EZELDIN
CHECKED BY	AMIR KHAN
APPROVED BY	NASSER ANANI
DATE	22-07-2026
REF NO. :	
CONSULTANT :	

TITLE: CABLE TRAY EXPANSION COUPLER

CLIENT: KENT GAD

SEC ITEM NO:

BONN METAL CONS. IND.

BONN GROUP OF COMPANIES
Cable Management Systems

DWRG. NO. :


SHEET NO. :


SCALE:NTS

REV. 01


NOTE:-

MATERIAL HDG 2mm HARDWARES SS316
Hot Dip Galvnaiztion 85 M without Epoxy

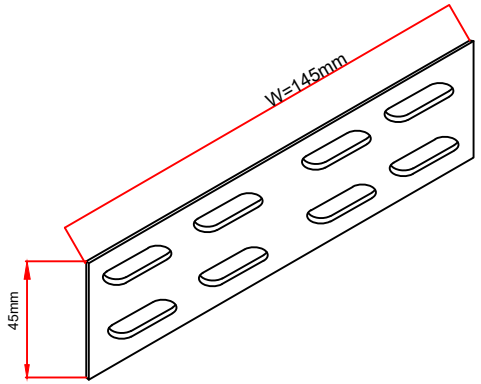


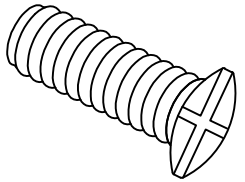

ROOFING BOLT
M6X16

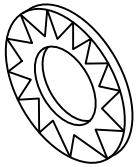

Washers M6

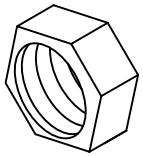

Nuts M6

CABLE TRAY EXPANSION COUPLER

SN	DIMENSION TABLE	QTY
147	W=145mm, H =95mm , T = 2mm	12

DRAWN BY	EZELDIN
CHECKED BY	AMIR KHAN
APPROVED BY	NASSER ANANI
DATE	22-07-2026
REF NO. :	
CONSULTANT :	

TITLE: CABLE TRAY EXPANSION COUPLER

CLIENT: KENT GAD

SEC ITEM NO:

BONN METAL CONS. IND.

BONN GROUP OF COMPANIES
Cable Management Systems

DWRG. NO. :


REV. 01


SHEET NO. :

SCALE:NTS


NOTE:-

MATERIAL HDG 2mm HARDWARES SS316
Hot Dip Galvnaiztion 85 M without Epoxy

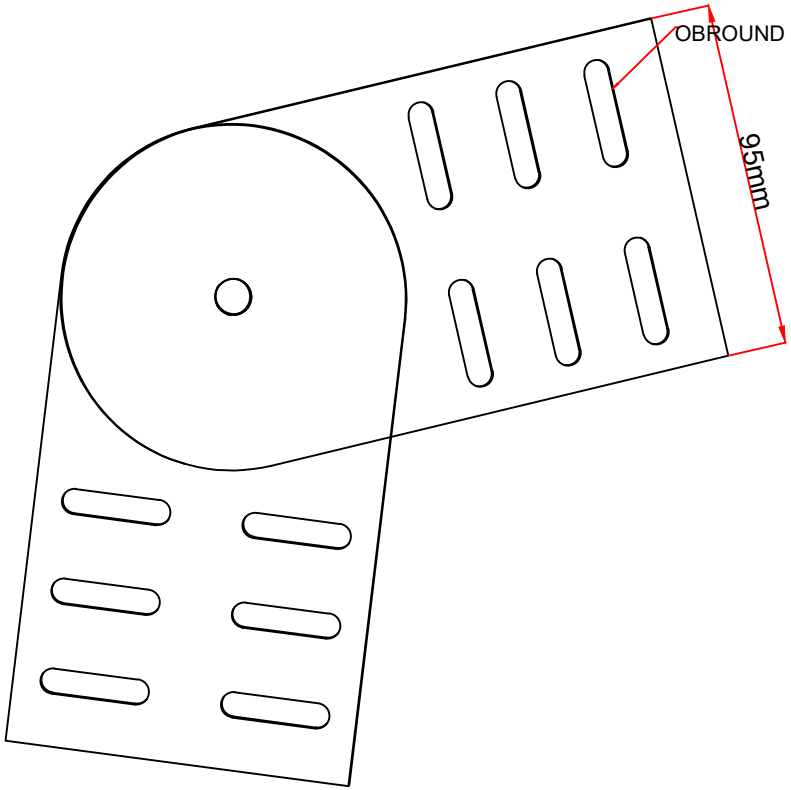


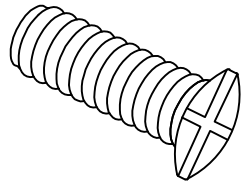

ROOFING BOLT
M6X16

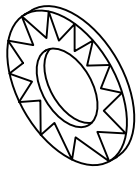

Washers M6

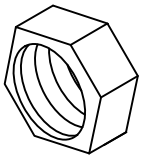

Nuts M6


CABLE TRAY VERTICAL ADJUSTABLE COUPLER


SN	DIMENSION TABLE	QTY	DRAWN BY	EZELDIN	TITLE: CABLE TRAY VERTICAL ADJUSTABLE COUPLER	BONN METAL CONS. IND.
148	H=100mm & T=2.0mm	192	CHECKED BY	AMIR KHAN		
			APPROVED BY	NASSER ANANI	CLIENT: KENT GAD	
			DATE	22-07-2026		
			REF NO. :		SEC ITEM NO:	DWRG. NO. : / REV. 01
			CONSULTANT :			SHEET NO. : / SCALE:NTS

BONN GROUP OF COMPANIES
Cable Management Systems


NOTE:-

MATERIAL HDG 2mm HARDWARES SS316
Hot Dip Galvnaiztion 85 M without Epoxy

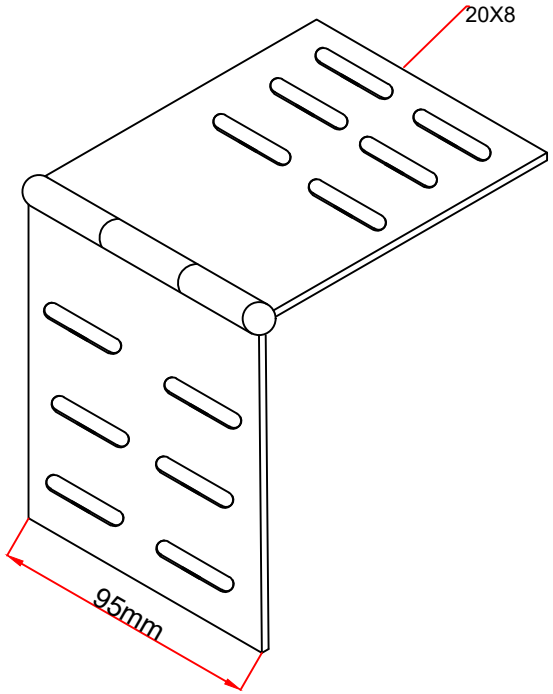


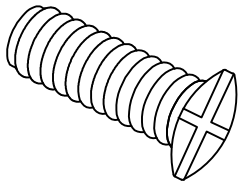

ROOFING BOLT
M6X16

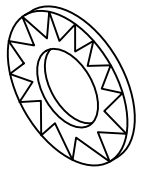

Washers M6

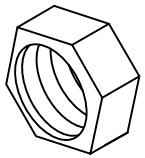

Nuts M6


CABLE TRAY ADJUSTABLE HORIZONTAL COUPLER


SN	DIMENSION TABLE	QTY	DRAWN BY	EZELDIN	TITLE: CABLE TRAY ADJUSTABLE HORIZONTAL COUPLER	BONN METAL CONS. IND.
149	H=100mm & T=2.0mm	192	CHECKED BY	AMIR KHAN		
			APPROVED BY	NASSER ANANI	CLIENT: KENT GAD	
			DATE	22-07-2026		
			REF NO. :		SEC ITEM NO:	DWRG. NO. : REV. 01
			CONSULTANT :			SHEET NO. : SCALE:NTS

BONN GROUP OF COMPANIES
Cable Management Systems


NOTE:-

MATERIAL HDG 2mm HARDWARES SS316
Hot Dip Galvnaiztion 85 M without Epoxy

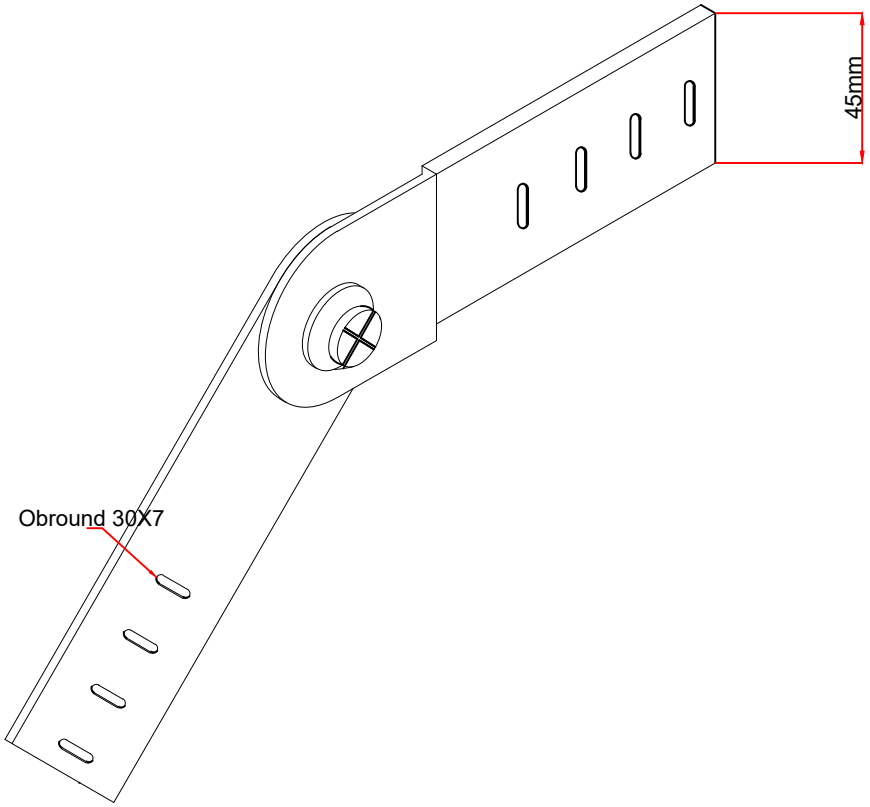


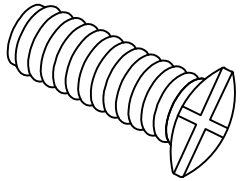

ROOFING BOLT
M6X16

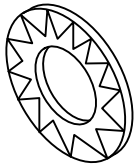

Washers M6

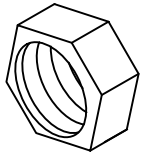

Nuts M6

CABLE TRAY VERTICAL ADJUSTABLE COUPLER

SN	DIMENSION TABLE	QTY
150	H=45mm & T=2.0mm	24

DRAWN BY	EZELDIN
CHECKED BY	AMIR KHAN
APPROVED BY	NASSER ANANI
DATE	22-07-2026
REF NO. :	
CONSULTANT :	

TITLE: CABLE TRAY VERTICAL ADJUSTABLE COUPLER

CLIENT: KENT GAD

SEC ITEM NO:

BONN METAL CONS. IND.

BONN GROUP OF COMPANIES
Cable Management Systems

DWRG. NO. :


REV. 01


SHEET NO. :

SCALE:NTS


NOTE:-

MATERIAL HDG 2mm HARDWARES SS316
Hot Dip Galvnaiztion 85 M without Epoxy

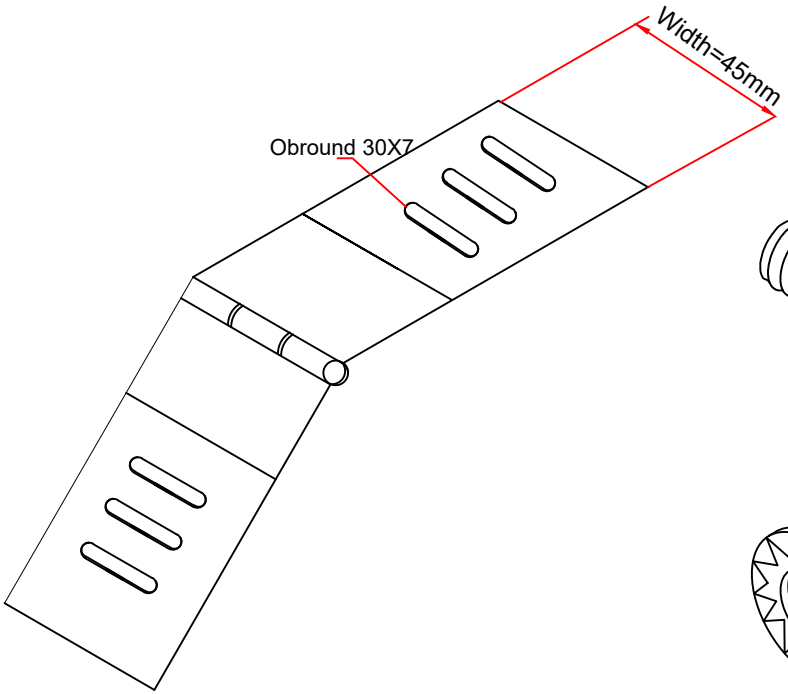


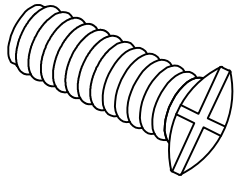

ROOFING BOLT
M6X16

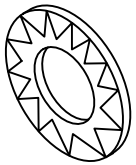

Washers M6

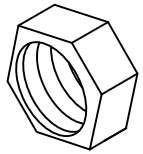

Nuts M6


CABLE TRAY HORIZONTAL ADJUSTABLE COUPLER

SN	DIMENSION TABLE	QTY	DRAWN BY	EZELDIN	TITLE: CABLE TRAY HORIZONTAL ADJUSTABLE COUPLER	BONN METAL CONS. IND.
151	H=45mm & T=2.0mm	24	CHECKED BY	AMIR KHAN		
			APPROVED BY	NASSER ANANI	CLIENT: KENT GAD	
			DATE	22-07-2026		
			REF NO. :		SEC ITEM NO:	DWRG. NO. : REV. 01
			CONSULTANT :			SHEET NO. : SCALE:NTS


Cable Management Systems

NOTE:-


MATERIAL HDG 2mm HARDWARES SS316
Hot Dip Galvnaiztion 85 M without Epoxy

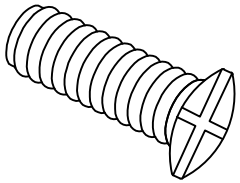


ROOFING BOLT
M8X30

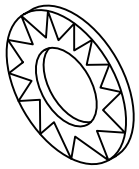

Washers M8

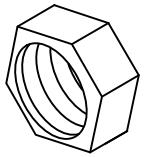

Nuts M8

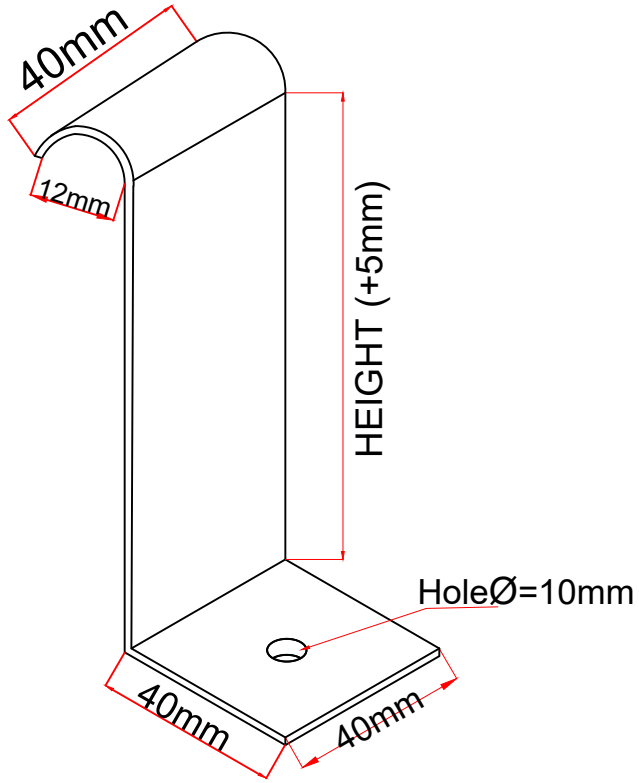

CABLE TRAY HOLD DOWN CLAMP

SN	DIMENSION TABLE	QTY
152	W=40mm, H =100+5mm , T = 2mm	5694

DRAWN BY	EZELDIN
CHECKED BY	AMIR KHAN
APPROVED BY	NASSER ANANI
DATE	22-07-2026
REF NO. :	
CONSULTANT :	

TITLE: CABLE TRAY HOLD DOWN CLAMP

CLIENT: KENT GAD

SEC ITEM NO:

BONN METAL CONS. IND.

BONN GROUP OF COMPANIES
Cable Management Systems

DWRG. NO. :


REV. 01

SHEET NO. :


SCALE:NTS

NOTE:-


MATERIAL HDG 2mm HARDWARES SS316
Hot Dip Galvnaiztion 85 M without Epoxy

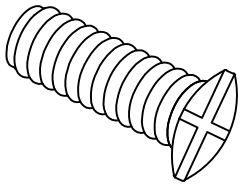


ROOFING BOLT
M8X30

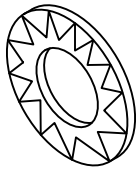

Washers M8

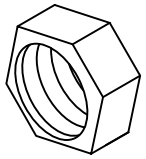

Nuts M8

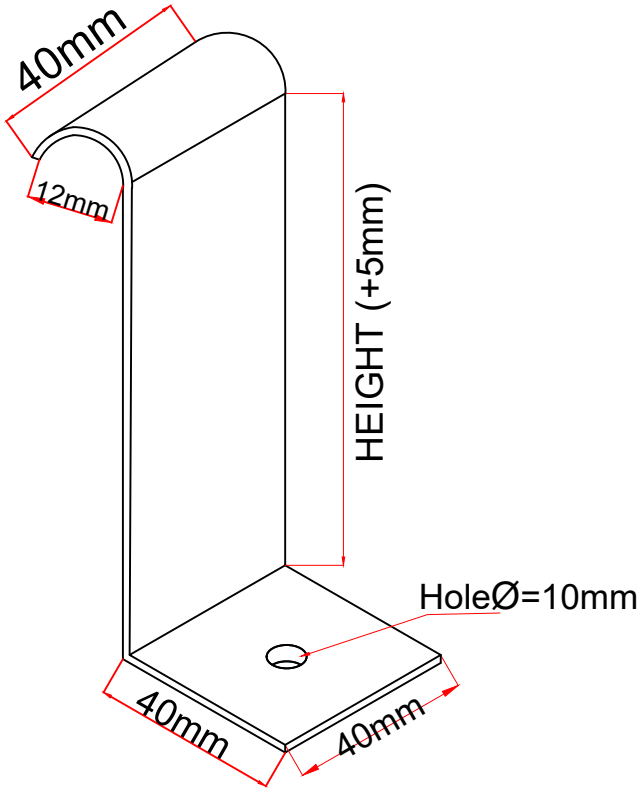

CABLE TRAY HOLD DOWN CLAMP

SN	DIMENSION TABLE	QTY
153	W=40mm, H =50+5mm , T = 2mm	510

DRAWN BY	EZELDIN
CHECKED BY	AMIR KHAN
APPROVED BY	NASSER ANANI
DATE	22-07-2026
REF NO. :	
CONSULTANT :	

TITLE: CABLE TRAY HOLD DOWN CLAMP

CLIENT: KENT GAD

SEC ITEM NO:

BONN METAL CONS. IND.

BONN GROUP OF COMPANIES
Cable Management Systems

DWRG. NO. :


REV. 01

SHEET NO. :

SCALE:NTS

NOTE:-

MATERIAL HDG 2mm HARDWARES SS316
Hot Dip Galvnaiztion 85 M without Epoxy

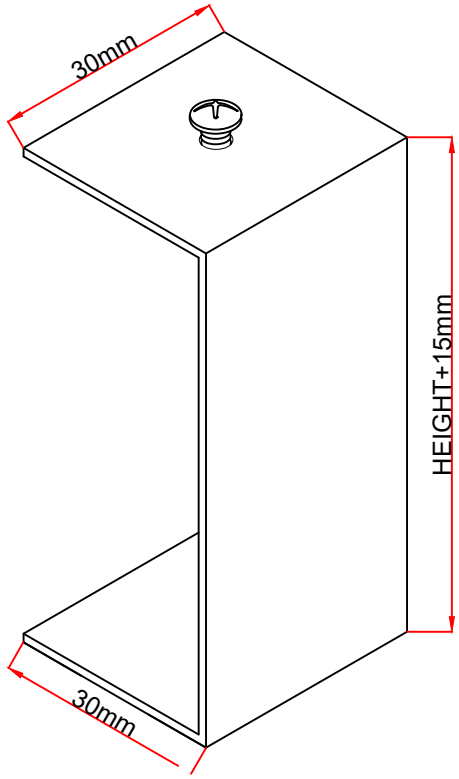

Cable Ladder cover Holding Clamps

SN	DIMENSION TABLE	QTY
154	W=30mm, H =100+5mm , T = 2mm	8121

DRAWN BY	EZELDIN
CHECKED BY	AMIR KHAN
APPROVED BY	NASSER ANANI
DATE	22-07-2026
REF NO. :	
CONSULTANT :	

TITLE: Cable Ladder cover Holding Clamps

CLIENT: KENT GAD

SEC ITEM NO:

BONN METAL CONS. IND.

BONN GROUP OF COMPANIES
Cable Management Systems

DWRG. NO. :


REV. 01

SHEET NO. :

SCALE:NTS

NOTE:-

MATERIAL HDG 2mm HARDWARES SS316
Hot Dip Galvnaiztion 85 M without Epoxy

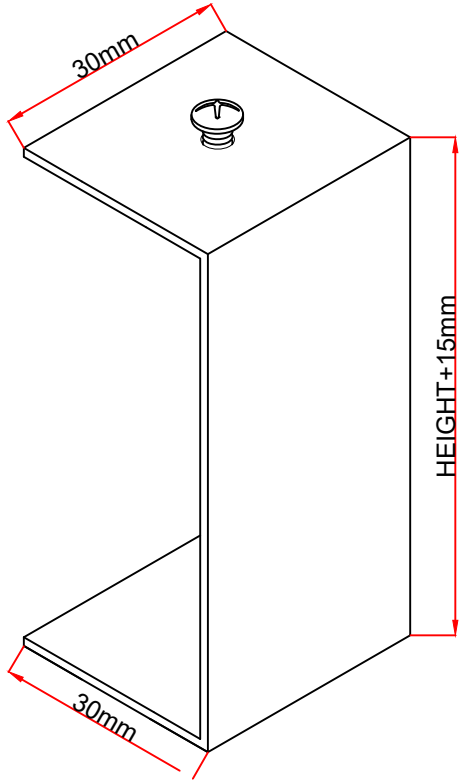



Cable Ladder cover Holding Clamps


SN	DIMENSION TABLE	QTY	DRAWN BY	EZELDIN	TITLE: Cable Ladder cover Holding Clamps	BONN METAL CONS. IND.
155	W=30mm, H =50+5mm , T = 2mm	900	CHECKED BY	AMIR KHAN		
			APPROVED BY	NASSER ANANI	CLIENT: KENT GAD	
			DATE	22-07-2026		
			REF NO. :		SEC ITEM NO:	DWRG. NO. : REV. 01
			CONSULTANT :			SHEET NO. : SCALE:NTS


BONN GROUP OF COMPANIES
Cable Management Systems

NOTE:-
MATERIAL HDG 2mm
Rung Spacing 250mm ALL flange 32 mm
Hot Dip Galvnaiztion 85 M without Epoxy
MIG WELDING

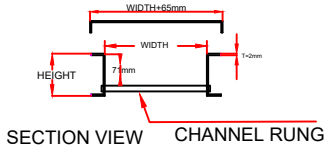

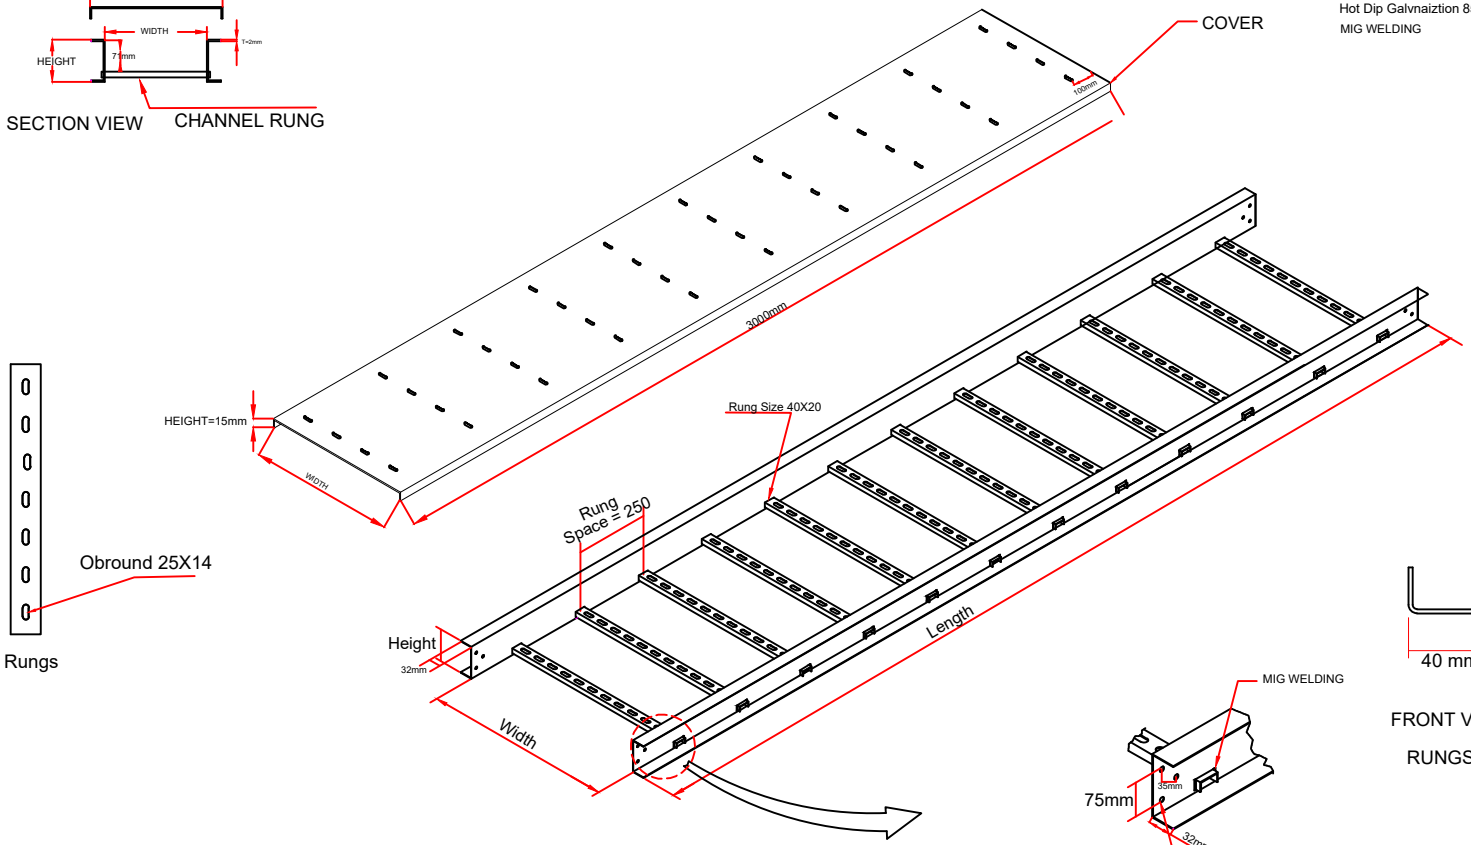

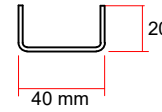

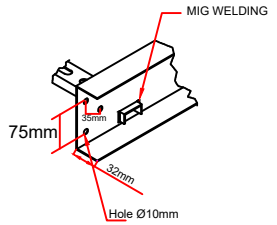

CABLE LADDER STRAIGHT LENGTH W/ COVER

SN	DIMENSION TABLE	QTY
386	W=750mm, H=100mm, T=2mm & L=3000mm W/COVER	232
387	W=600mm, H=100mm, T=2mm & L=3000mm W/COVER	230
388	W=300mm, H=100mm, T=2mm & L=3000mm W/COVER	98

DRAWN BY	EZELDIN
CHECKED BY	AMIR KHAN
APPROVED BY	NASSER ANANI
DATE	22-07-2026
REF NO. :	
CONSULTANT :	


TITLE: CABLE LADDER STRAIGHT LENGTH W/ COVER
CLIENT: KENT GAD
SEC ITEM NO:

BONN METAL CONS. IND.
BONN GROUP OF COMPANIES
Cable Management Systems


DWRG. NO. :
REV. 01
SHEET NO. :
SCALE:NTS


NOTE:-

MATERIAL HDG 2mm ALL flange 32 mm
Hot Dip Galvnaiztion 85 M without Epoxy
MIG WELDING

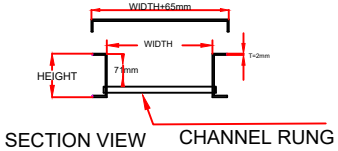


SECTION VIEW CHANNEL RUNG

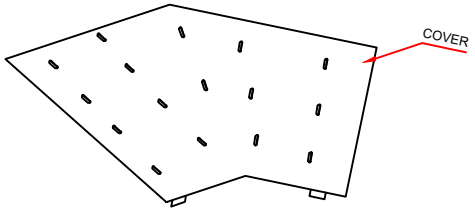


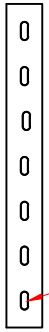


Obround 25X14

Rungs

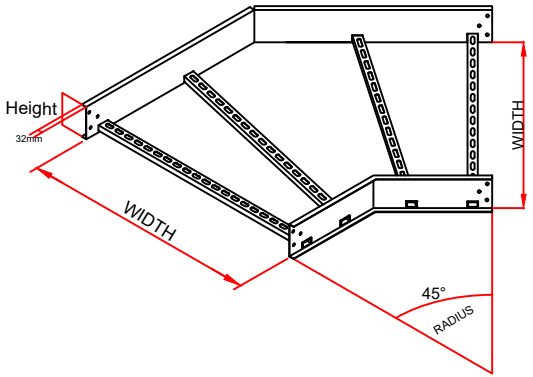

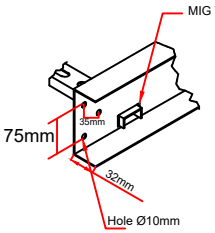

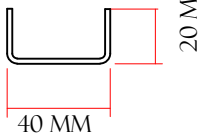

SIDE VIEW

CABLE LADDER BEND 45° DEG W/COVER

SN	DIMENSION TABLE	QTY
389	W=300mm, H =100mm , R= 600mm , T = 2mm W/COVER	2
390	W=600mm, H =100mm , R= 600mm , T = 2mm ,W/COVER	6
391	W=900mm, H =100mm , R= 600mm , T = 2mm , W/COVER	2

DRAWN BY	EZELDIN
CHECKED BY	AMIR KHAN
APPROVED BY	NASSER ANANI
DATE	22-07-2026
REF NO. :	
CONSULTANT :	

TITLE: CABLE LADDER VERTICAL 45° BEND W/COVER

CLIENT: KENT GAD

SEC ITEM NO:

BONN METAL CONS. IND.

BONN GROUP OF COMPANIES
Cable Management Systems

DWRG. NO. :

REV. 01

SHEET NO. :


SCALE:NTS

Project: 04108 EPC FOR SE AiP5 PROJECT (ON PLOT) – ASAB/SAHIL (PACKAGE 1)


ELECTRICAL CABLE TRAY AND ACCESSORIES - SAHIL -WITHOUT EPOXY


NOTE:-

MATERIAL HDG 3mm
Hot Dip Galvnaiztion 85 M without Epoxy
MATERIAL HDG 2mm FOR COVER

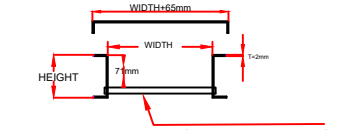



SECTION VIEW CHANNEL RUNG

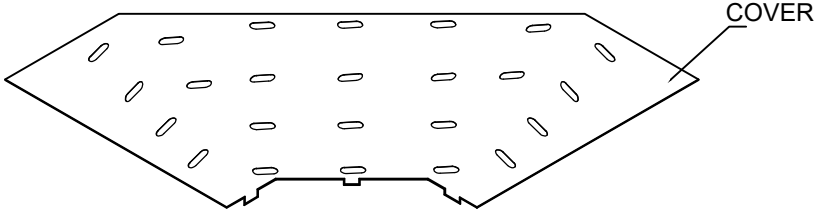

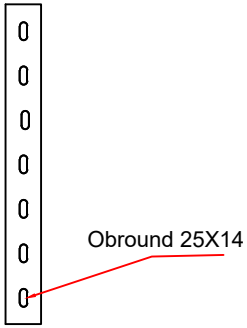


Rungs

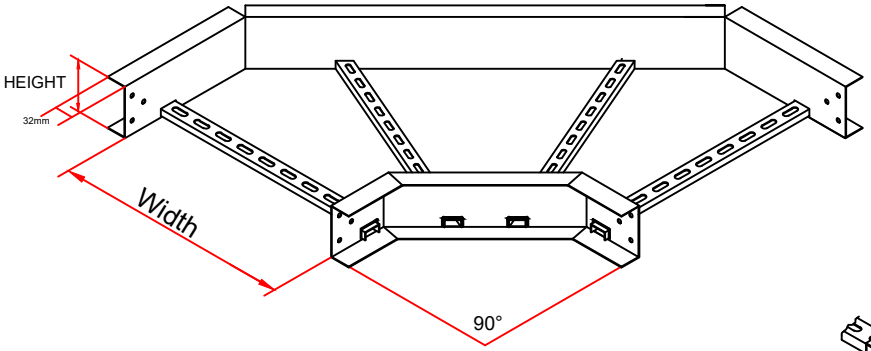

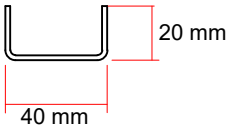

SIDE VIEW

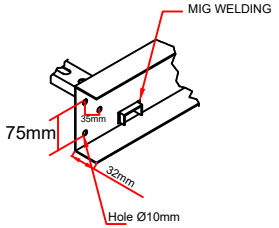

CABLE LADDER BEND 90DEG W/COVER

SN	DIMENSION TABLE	QTY
392	W=300mm, H =100mm , R= 300mm , T = 2mm W/COVER	4
393	W=300mm, H =100mm , R= 600mm , T = 2mm W/COVER	5
394	W=600mm, H =100mm , R= 600mm , T = 2mm W/COVER	14
395	W=750mm, H =100mm , R= 600mm , T = 2mm W/COVER	9
396	W=750mm, H =100mm , R= 900mm , T = 2mm W/COVER	2

DRAWN BY	EZELDIN
CHECKED BY	AMIR KHAN
APPROVED BY	NASSER ANANI
DATE	22-07-2026
REF NO. :	
CONSULTANT :	

TITLE: CABLE LADDER BEND 90DEG W/COVER

CLIENT: KENT GAD

SEC ITEM NO:

BONN METAL CONS. IND.

BONN GROUP OF COMPANIES
Cable Management Systems

DWRG. NO. :


REV. 01

SHEET NO. :


SCALE:NTS


NOTE:-

MATERIAL HDG 2mm ALL flange 32 mm
Hot Dip Galvnaiztion 85 M without Epoxy
MIG WELDING

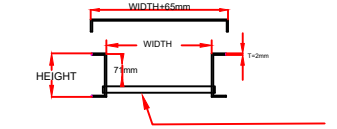


SECTION VIEW CHANNEL RUNG

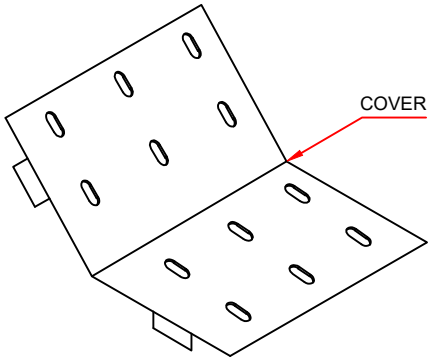


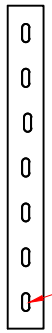


Obround 25X14

Rungs

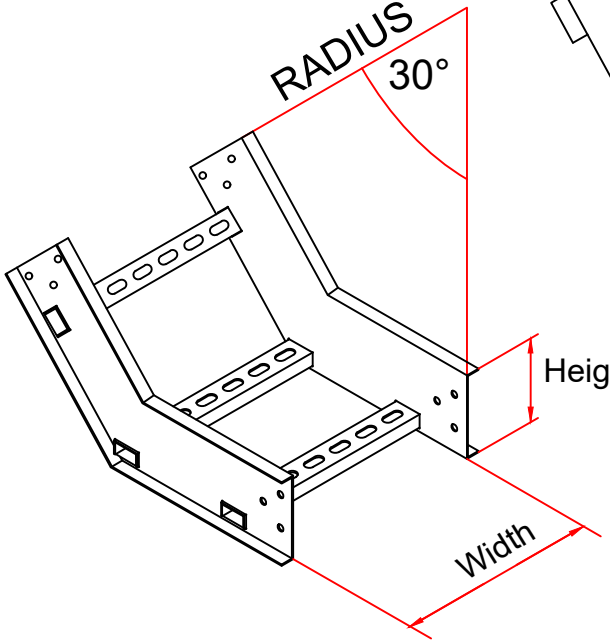

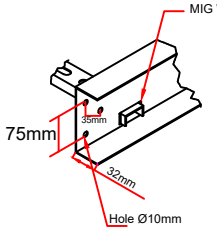

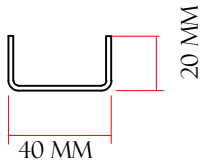

SIDE VIEW

CABLE LADDER 30° DEG INSIDE RISER

SN	DIMENSION TABLE	QTY	DRAWN BY	EZELDIN
397	W=300mm, H =100mm , R= 300mm , T = 2mm W/COVER	2	CHECKED BY	AMIR KHAN
			APPROVED BY	NASSER ANANI
			DATE	22-07-2026
			REF NO. :	
			CONSULTANT :	

TITLE: CABLE LADDER 30° DEG INSIDE RISER

CLIENT: KENT GAD

SEC ITEM NO:

BONN METAL CONS. IND.


BONN GROUP OF COMPANIES
Cable Management Systems

DWRG. NO. :


REV. 01


SHEET NO. :

SCALE:NTS

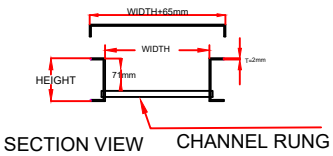


SECTION VIEW CHANNEL RUNG

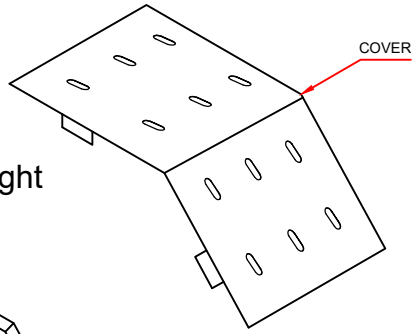

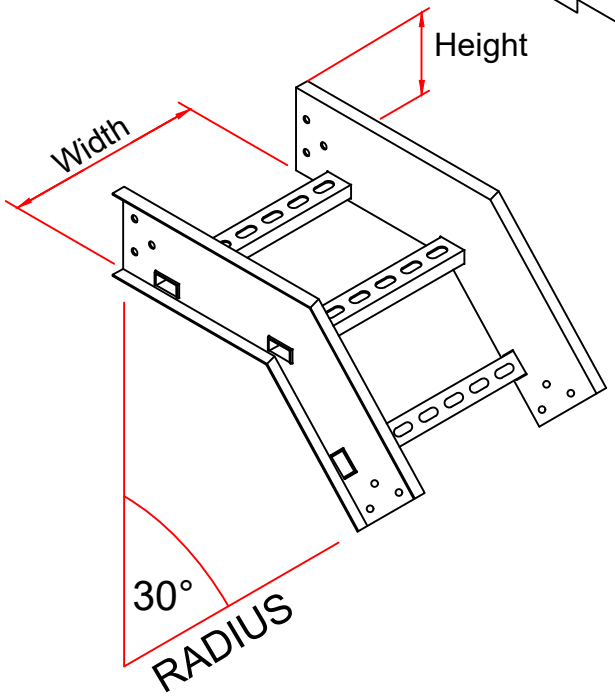


NOTE:-


MATERIAL HDG 2mm ALL flange 32 mm
Hot Dip Galvnaiztion 85 M without Epoxy
MIG WELDING

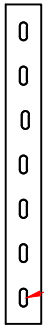

Obround 25X14

Rungs

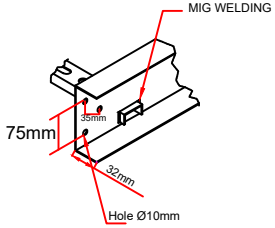

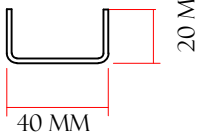

SIDE VIEW

CABLE LADDER 30° DEG OUTSIDE RISER W COVER

SN	DIMENSION TABLE	QTY	DRAWN BY	EZELDIN
398	W=300mm, H =100mm , R= 300mm , T = 2mm W/COVER	2	CHECKED BY	AMIR KHAN
			APPROVED BY	NASSER ANANI
			DATE	22-07-2026
			REF NO. :	
			CONSULTANT :	

TITLE: CABLE LADDER 30° DEG OUTSIDE RISER W COVER

CLIENT: KENT GAD

SEC ITEM NO:

BONN METAL CONS. IND.


BONN GROUP OF COMPANIES
Cable Management Systems

DWRG. NO. :

REV. 01

SHEET NO. :


SCALE:NTS

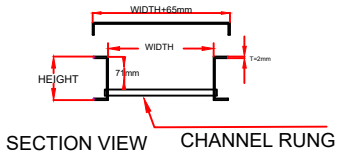



SECTION VIEW CHANNEL RUNG

NOTE:-


MATERIAL HDG 2mm ALL flange 32 mm
Hot Dip Galvnaiztion 85 M without Epoxy
MIG WELDING

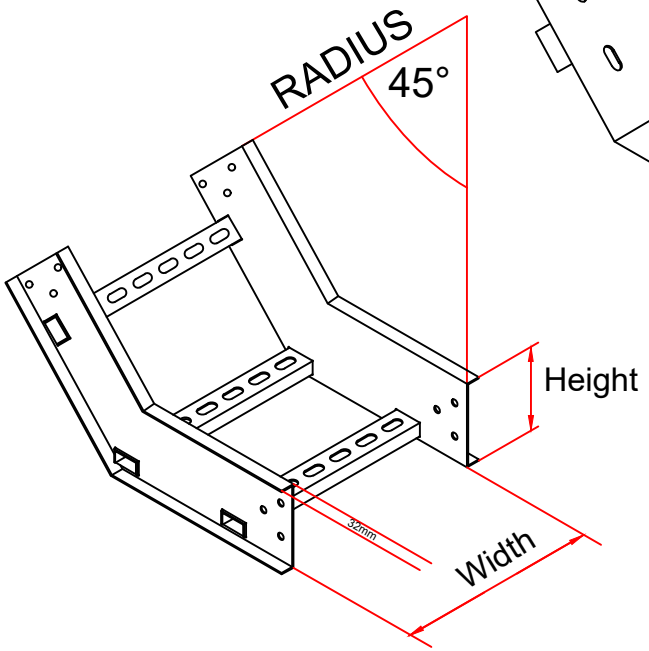


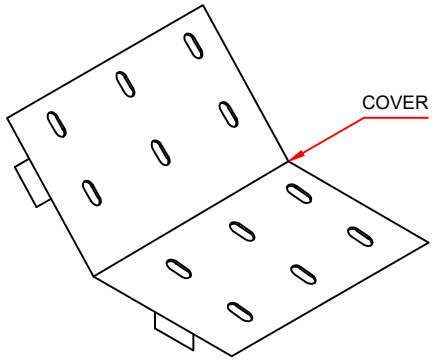

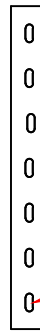

Rungs

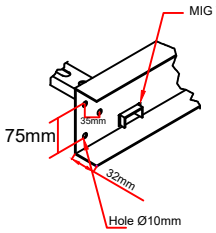

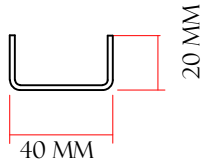

SIDE VIEW

CABLE LADDER 45° DEG (V) INSIDE RISER

SN	DIMENSION TABLE	QTY
399	W=300mm, H =100mm , R= 600mm , T = 2mm W/COVER	5

DRAWN BY	EZELDIN
CHECKED BY	AMIR KHAN
APPROVED BY	NASSER ANANI
DATE	22-07-2026
REF NO. :	
CONSULTANT :	

TITLE: CABLE LADDER 45° DEG INSIDE RISER

CLIENT: KENT GAD

SEC ITEM NO:

BONN METAL CONS. IND.


BONN GROUP OF COMPANIES
Cable Management Systems

DWRG. NO. :


REV. 01


SHEET NO. :

SCALE:NTS

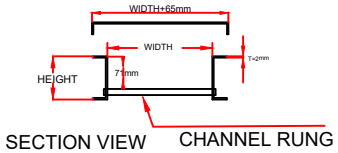


SECTION VIEW CHANNEL RUNG

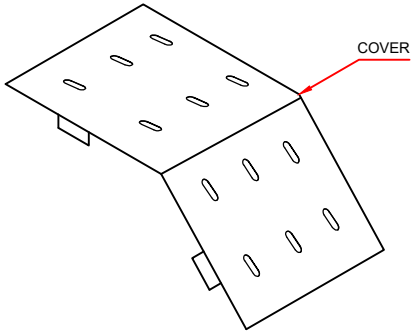

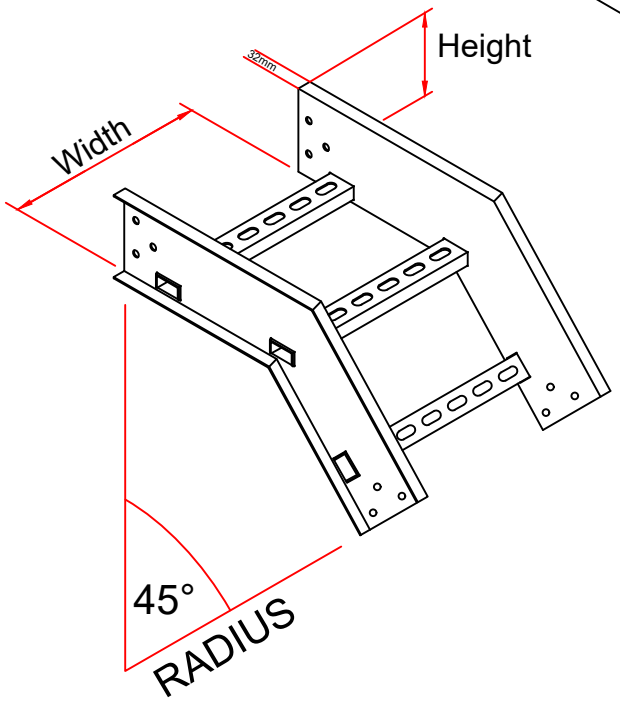


NOTE:-


MATERIAL HDG 2mm ALL flange 32 mm
Hot Dip Galvnaiztion 85 M without Epoxy
MIG WELDING

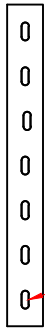

Obround 25X14

Rungs

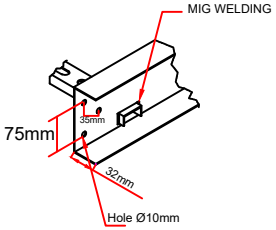

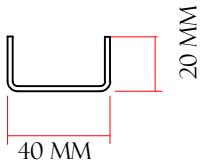

SIDE VIEW

CABLE LADDER 45° DEG (V) OUTSIDE RISER W COVER

SN	DIMENSION TABLE	QTY
400	W=300mm, H =100mm , R= 600mm , T = 2mm W/COVER	5

DRAWN BY	EZELDIN
CHECKED BY	AMIR KHAN
APPROVED BY	NASSER ANANI
DATE	22-07-2026
REF NO. :	
CONSULTANT :	

TITLE: CABLE LADDER 45° DEG OUTSIDE RISER W COVER

CLIENT: KENT GAD

SEC ITEM NO:

BONN METAL CONS. IND.

BONN GROUP OF COMPANIES
Cable Management Systems

DWRG. NO. :


REV. 01

SHEET NO. :


SCALE:NTS


NOTE:-

MATERIAL HDG 2mm ALL flange 32 mm
Hot Dip Galvnaiztion 85 M without Epoxy
MIG WELDING

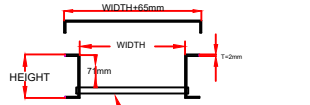


SECTION VIEW CHANNEL RUNG

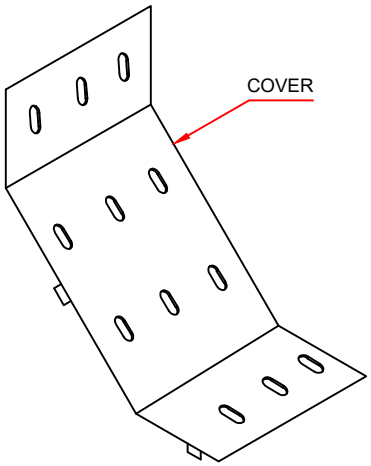


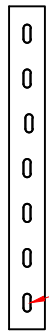


Obround 25X14

Rungs

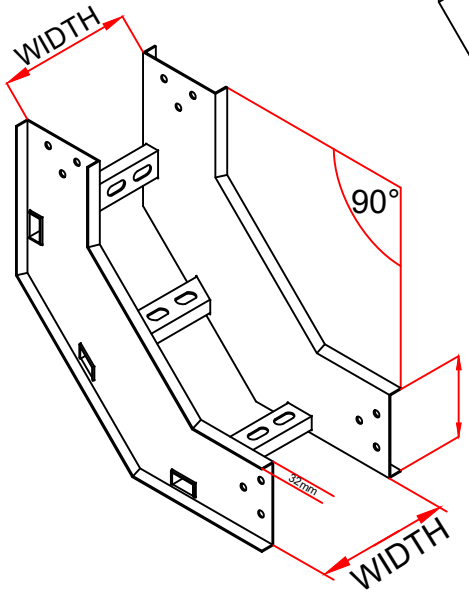

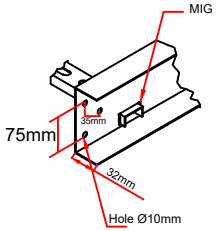

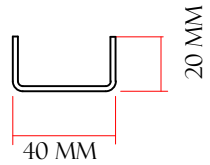

SIDE VIEW

CABLE LADDER BEND 90° INSIDE RISER W/COVER

SN	DIMENSION TABLE	QTY
401	W=300mm, H =100mm , R= 300mm , T = 2mm W/COVER	2
402	W=300mm, H =100mm , R= 600mm , T = 2mm ,W/COVER	2
403	W=600mm, H =100mm , R= 600mm , T = 2mm , W/COVER	3
404	W=750mm, H =100mm , R= 900mm , T = 2mm , W/COVER	2

DRAWN BY	EZELDIN
CHECKED BY	AMIR KHAN
APPROVED BY	NASSER ANANI
DATE	22-07-2026
REF NO. :	
CONSULTANT :	

TITLE: CABLE LADDER BEND 90° INSIDE RISER W/COVER

CLIENT: KENT GAD

SEC ITEM NO:

BONN METAL CONS. IND.

BONN GROUP OF COMPANIES
Cable Management Systems

DWRG. NO. :


REV. 01

SHEET NO. :


SCALE:NTS


NOTE:-


MATERIAL HDG 2mm ALL flange 32 mm
Hot Dip Galvnaiztion 85 M without Epoxy
MIG WELDING

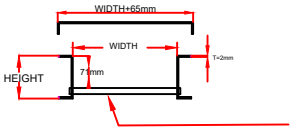

SECTION VIEW CHANNEL RUNG

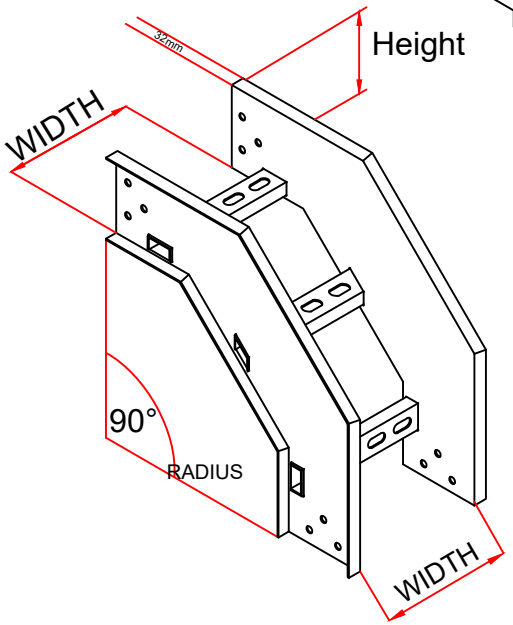


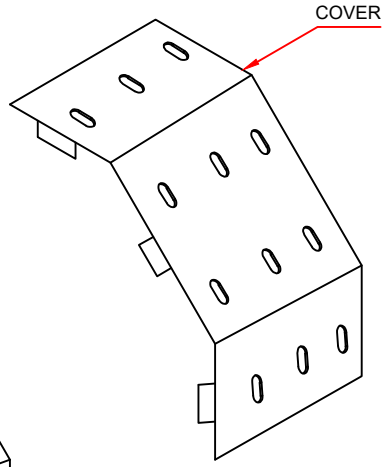


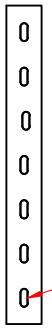

Obround 25X14

Rungs

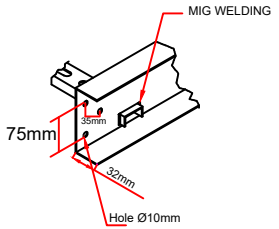

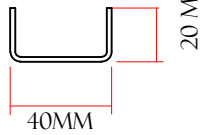

SIDE VIEW

CABLE LADDER BEND 90° OUTSIDE RISER W/COVER

SN	DIMENSION TABLE	QTY
405	W=300mm, H =100mm , R= 300mm , T = 2mm W/COVER	2
406	W=300mm, H =100mm , R= 600mm , T = 2mm ,W/COVER	3
407	W=600mm, H =100mm , R= 600mm , T = 2mm , W/COVER	3
408	W=750mm, H =100mm , R=900mm , T = 2mm , W/COVER	3

DRAWN BY	EZELDIN
CHECKED BY	AMIR KHAN
APPROVED BY	NASSER ANANI
DATE	22-07-2026
REF NO. :	
CONSULTANT :	

TITLE: CABLE LADDER BEND 90° OUTSIDE RISER W/COVER

CLIENT: KENT GAD

SEC ITEM NO:

BONN METAL CONS. IND.

BONN GROUP OF COMPANIES
Cable Management Systems

DWRG. NO. :


REV. 01

SHEET NO. :


SCALE:NTS


NOTE:-

MATERIAL HDG 2mm ALL flange 32 mm
Hot Dip Galvnaiztion 85 M without Epoxy
MIG WELDING

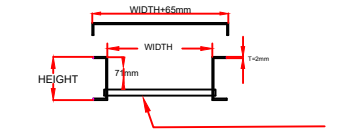


SECTION VIEW CHANNEL RUNG

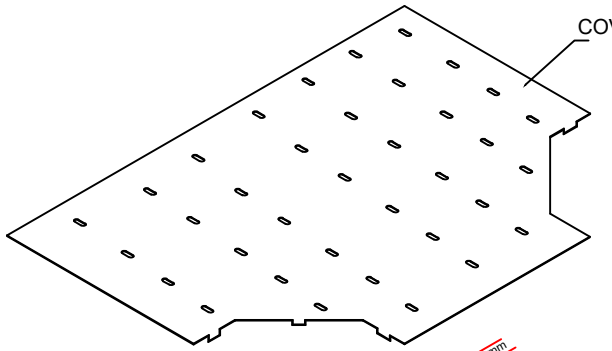

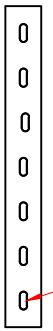



Obround 25X14

Rungs

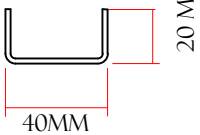

SIDE VIEW

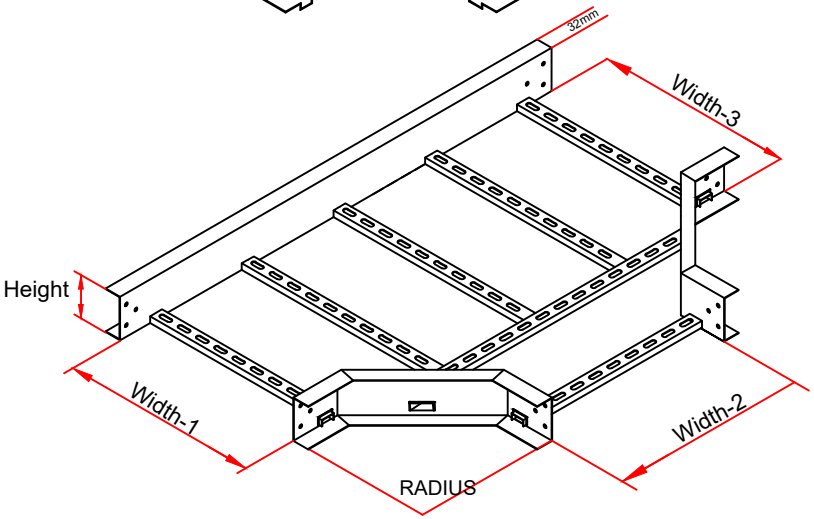

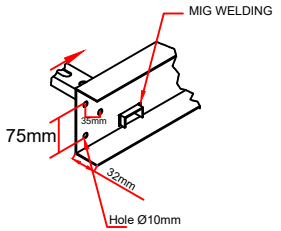

CABLE LADDER EQUAL TEE W/COVER

SN	DIMENSION TABLE	QTY
409	W=300mm, H =100mm , R= 600mm , T = 2mm W/COVER	2
410	W=600mm, H =100mm , R= 600mm , T = 2mm ,W/COVER	41
411	W=750mm, H =100mm , R= 300mm , T = 2mm , W/COVER	43

DRAWN BY	EZELDIN
CHECKED BY	AMIR KHAN
APPROVED BY	NASSER ANANI
DATE	22-07-2026
REF NO. :	
CONSULTANT :	

TITLE: CABLE LADDER EQUAL TEE W/COVER

CLIENT: KENT GAD

SEC ITEM NO:

BONN METAL CONS. IND.


BONN GROUP OF COMPANIES
Cable Management Systems


DWRG. NO. :

REV. 01

SHEET NO. :


SCALE:NTS

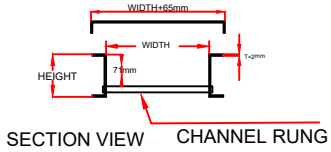


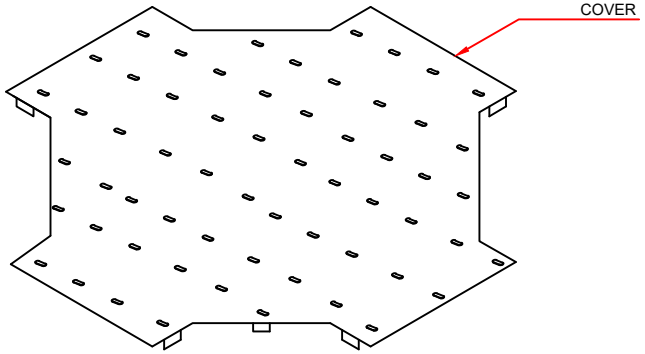



NOTE:-

MATERIAL HDG 2mm ALL flange 32 mm
Hot Dip Galvnaiztion 85 M without Epoxy
MIG WELDING

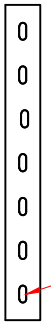

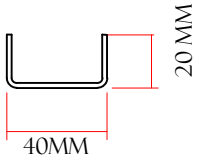

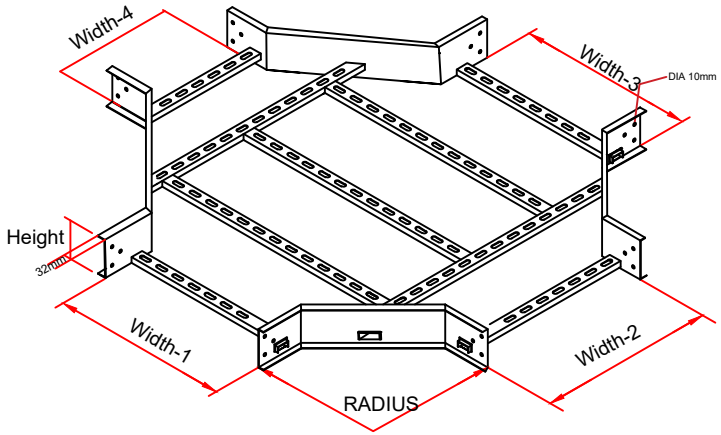

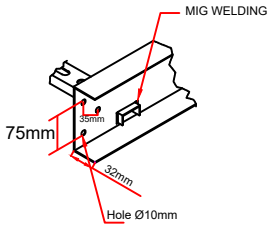

CABLE LADDER CROSS W/COVER

SN	DIMENSION TABLE	QTY
412	W = 750mm, H =100mm , R= 600mm , T = 2mm ,W/COVER	15
413	W = 600mm, H =100mm , R= 600mm , T = 2mm W/COVER	17

DRAWN BY	EZELDIN
CHECKED BY	AMIR KHAN
APPROVED BY	NASSER ANANI
DATE	22-07-2026
REF NO. :	
CONSULTANT :	

TITLE: CABLE LADDER CROSS W/COVER

CLIENT: KENT GAD

SEC ITEM NO:

BONN METAL CONS. IND.

BONN GROUP OF COMPANIES
Cable Management Systems


DWRG. NO. :

REV. 01

SHEET NO. :


SCALE:NTS

NOTE:-
MATERIAL HDG 2mm
Rung Spacing 250mm ALL flange 32 mm
Hot Dip Galvnaiztion 85 M without Epoxy
MIG WELDING
Cover Height 12mm

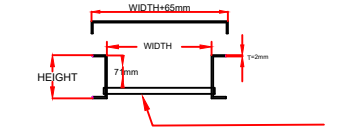



SECTION VIEW

CHANNEL RUNG

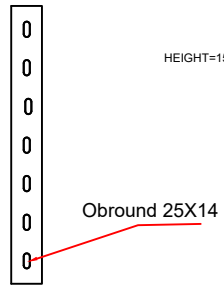


Rungs

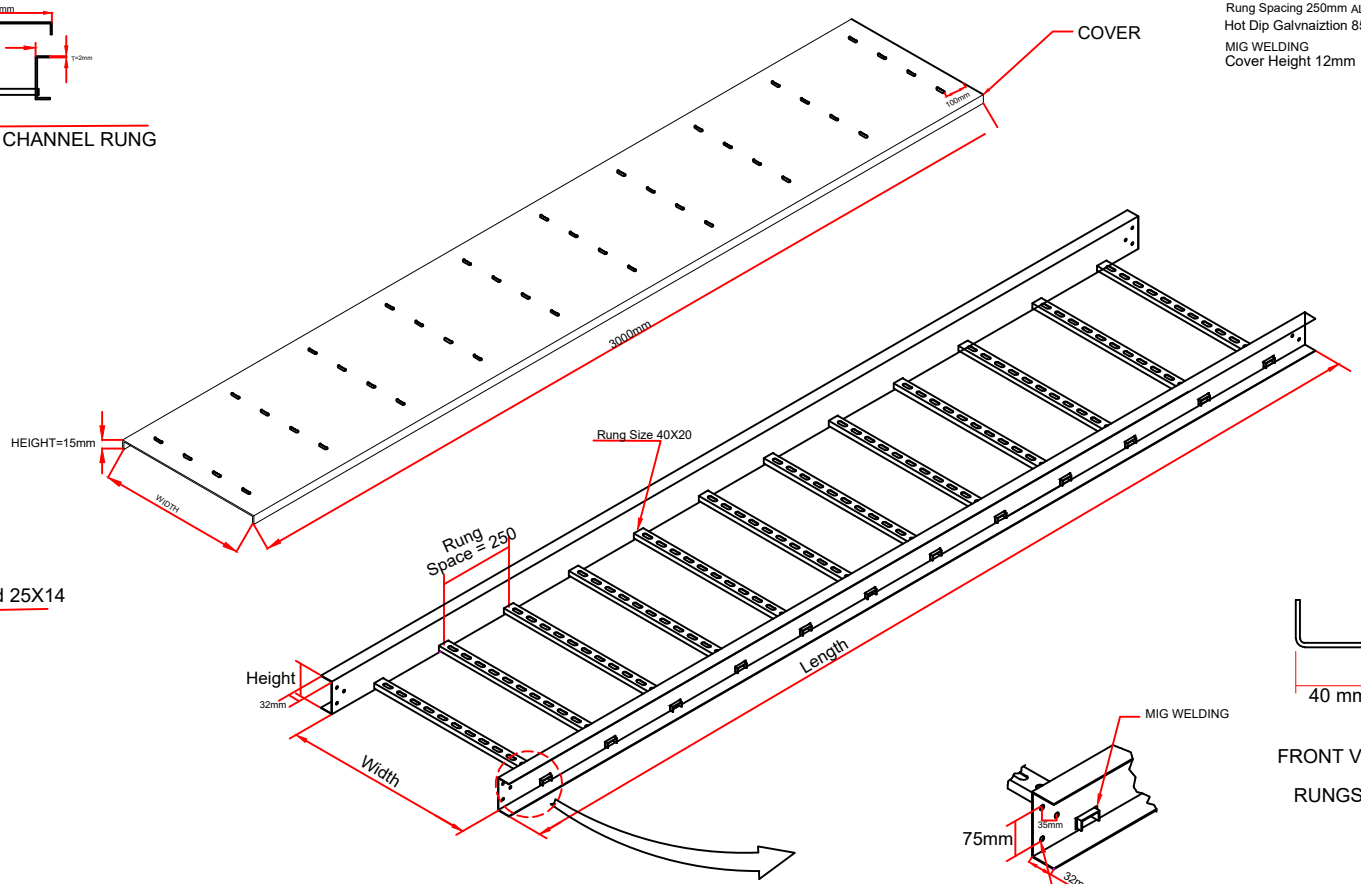

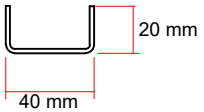

FRONT VIEW

RUNGS

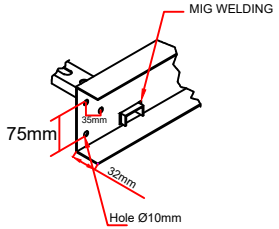

CABLE LADDER STRAIGHT LENGTH W/ COVER

SN	DIMENSION TABLE	QTY
414	W=750mm, H=100mm, T=2mm & L=3000mm W/COVER	4
415	W=600mm, H=100mm, T=2mm & L=3000mm W/COVER	4
416	W=300mm, H=100mm, T=2mm & L=3000mm W/COVER	38

DRAWN BY	EZELDIN
CHECKED BY	AMIR KHAN
APPROVED BY	NASSER ANANI
DATE	22-07-2026
REF NO. :	
CONSULTANT :	

TITLE: CABLE LADDER STRAIGHT LENGTH W/ COVER

CLIENT: KENT GAD

SEC ITEM NO:

BONN METAL CONS. IND.

BONN GROUP OF COMPANIES
Cable Management Systems

DWRG. NO. :


REV. 01

SHEET NO. :


SCALE:NTS


NOTE:-

MATERIAL HDG 2mm ALL flange 32 mm
Hot Dip Galvnaiztion 85 M without Epoxy
MIG WELDING
Cover Height 12mm

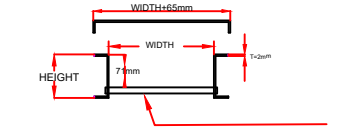


SECTION VIEW CHANNEL RUNG

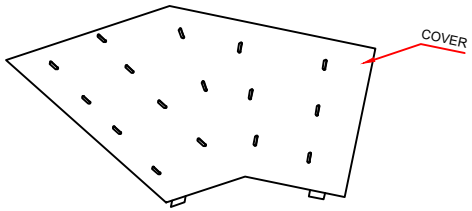


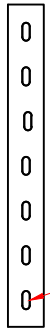


Obround 25X14

Rungs

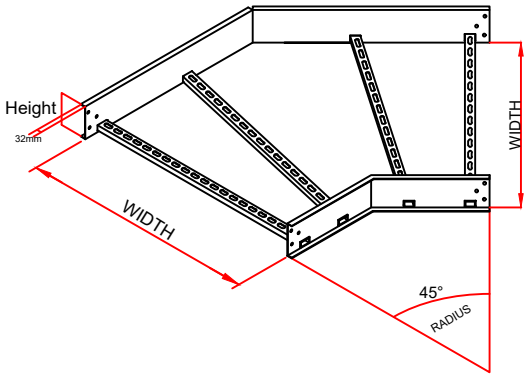

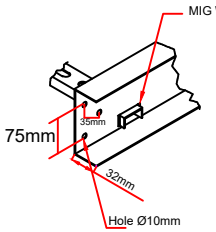

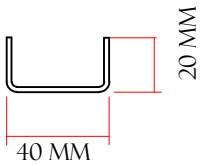

SIDE VIEW

CABLE LADDER BEND 45° DEG W/COVER

SN	DIMENSION TABLE	QTY
417	W=300mm, H =100mm , R= 600mm , T = 2mm W/COVER	2
418	W=600mm, H =100mm , R= 600mm , T = 2mm ,W/COVER	6
419	W=900mm, H =100mm , R= 600mm , T = 2mm , W/COVER	2

DRAWN BY	EZELDIN
CHECKED BY	AMIR KHAN
APPROVED BY	NASSER ANANI
DATE	22-07-2026
REF NO. :	
CONSULTANT :	

TITLE: CABLE LADDER VERTICAL 45° BEND W/COVER

CLIENT: KENT GAD

SEC ITEM NO:

BONN METAL CONS. IND.

BONN GROUP OF COMPANIES
Cable Management Systems

DWRG. NO. :

REV. 01

SHEET NO. :


SCALE:NTS

Project: 04108 EPC FOR SE AiP5 PROJECT (ON PLOT) – ASAB/SAHIL (PACKAGE 1)


ELECTRICAL CABLE TRAY AND ACCESSORIES - SAHIL -WITHOUT EPOXY


NOTE:-

MATERIAL HDG 3mm
Hot Dip Galvnaiztion 85 M without Epoxy
MATERIAL HDG 2mm FOR COVER
Cover Height 12mm

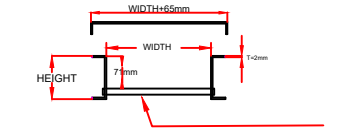



SECTION VIEW CHANNEL RUNG

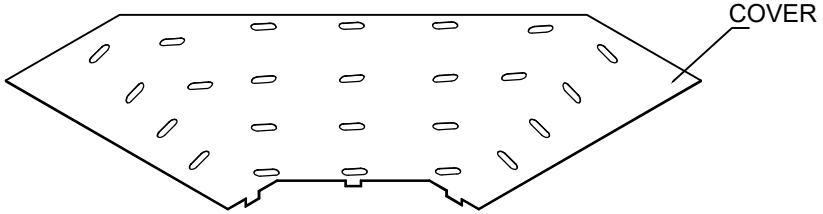

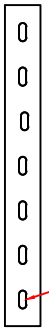


Rungs

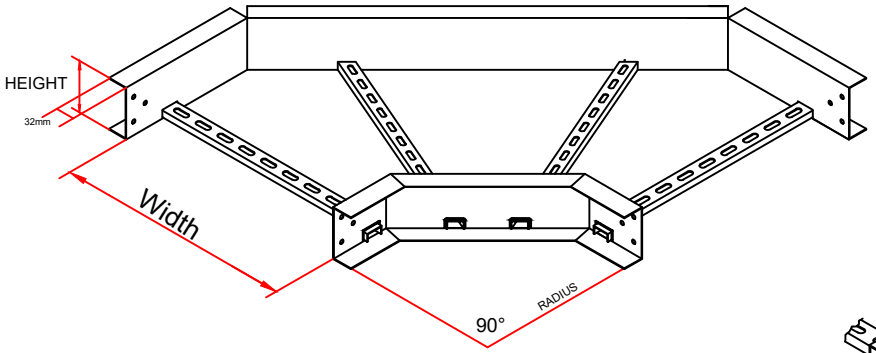

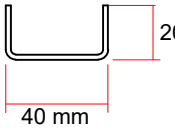

SIDE VIEW

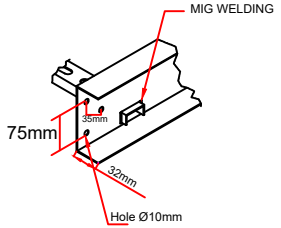

CABLE LADDER BEND 90DEG W/COVER

SN	DIMENSION TABLE	QTY
420	W=300mm, H =100mm , R= 300mm , T = 2mm W/COVER	4
421	W=300mm, H =100mm , R= 600mm , T = 2mm W/COVER	2
422	W=750mm, H =100mm , R=900mm , T = 2mm W/COVER	2

DRAWN BY	EZELDIN
CHECKED BY	AMIR KHAN
APPROVED BY	NASSER ANANI
DATE	22-07-2026
REF NO. :	
CONSULTANT :	

TITLE: CABLE LADDER BEND 90DEG W/COVER

CLIENT: KENT GAD

SEC ITEM NO:

BONN METAL CONS. IND.

BONN GROUP OF COMPANIES
Cable Management Systems

DWRG. NO. :


REV. 01

SHEET NO. :


SCALE:NTS


NOTE:-

MATERIAL HDG 2mm ALL flange 32 mm
Hot Dip Galvnaiztion 85 M without Epoxy
MIG WELDING
Cover Height 12mm

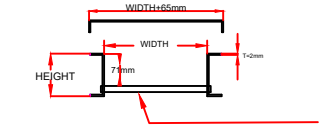


SECTION VIEW CHANNEL RUNG

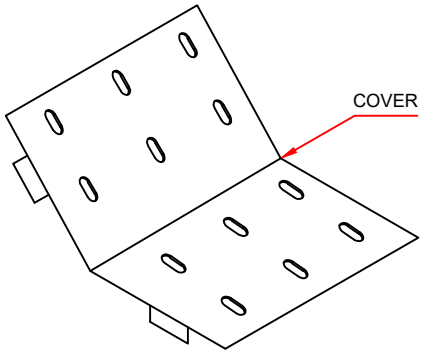


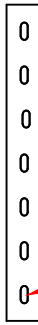


Obround 25X14

Rungs

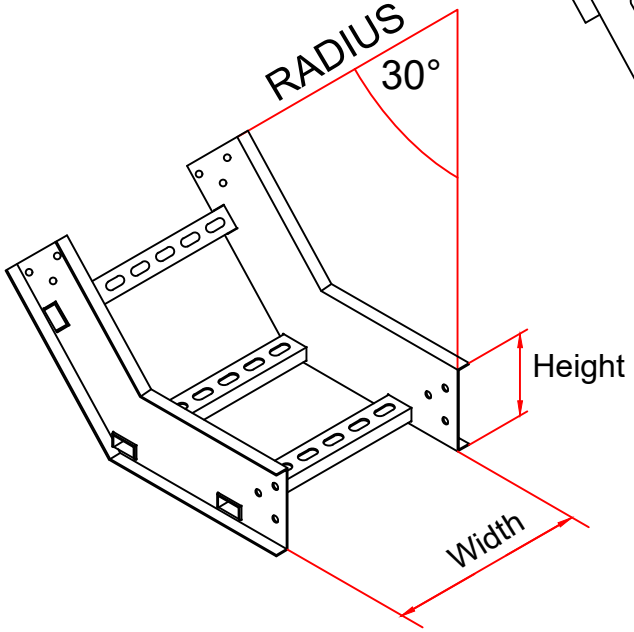

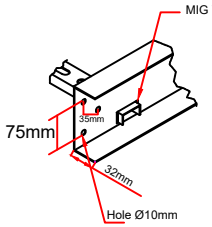

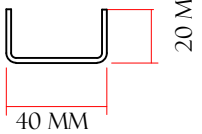

SIDE VIEW

CABLE LADDER 30° DEG INSIDE RISER

SN	DIMENSION TABLE	QTY
423	W=300mm, H =100mm , R= 300mm , T = 2mm W/COVER	2

DRAWN BY	EZELDIN
CHECKED BY	AMIR KHAN
APPROVED BY	NASSER ANANI
DATE	22-07-2026
REF NO. :	
CONSULTANT :	

TITLE: CABLE LADDER 30° DEG INSIDE RISER

CLIENT: KENT GAD

SEC ITEM NO:

BONN METAL CONS. IND.


BONN GROUP OF COMPANIES
Cable Management Systems

DWRG. NO. :


REV. 01

SHEET NO. :

SCALE:NTS

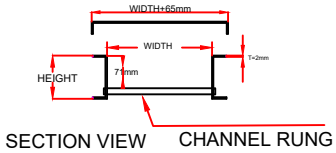


SECTION VIEW CHANNEL RUNG

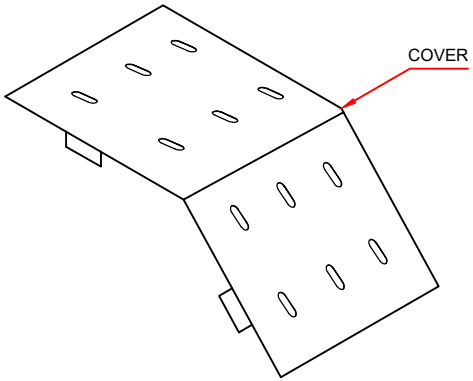


NOTE:-


MATERIAL HDG 2mm ALL flange 32 mm
Hot Dip Galvnaiztion 85 M without Epoxy
MIG WELDING
Cover Height 12mm

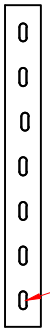


Obround 25X14

Rungs

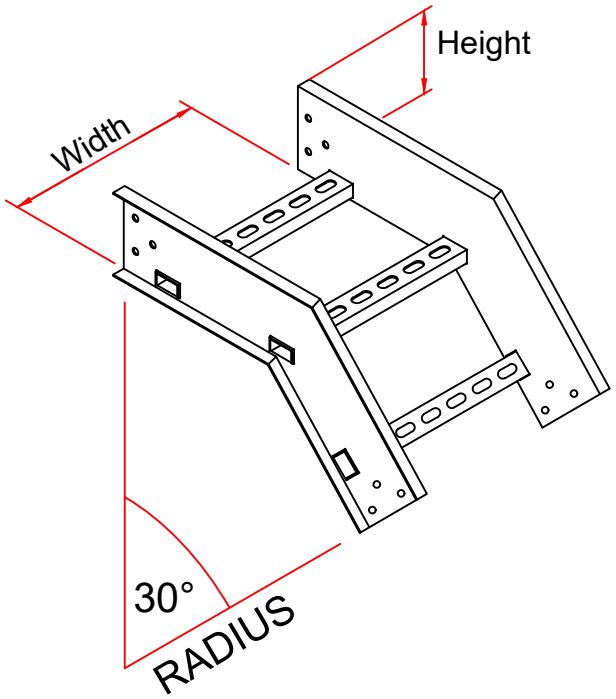

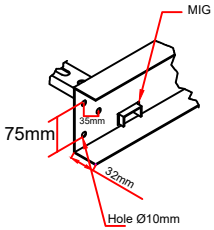

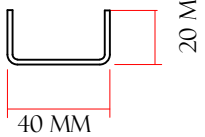

SIDE VIEW

CABLE LADDER 30° DEG OUTSIDE RISER W COVER

SN	DIMENSION TABLE	QTY	DRAWN BY	EZELDIN
424	W=300mm, H =100mm , R= 300mm , T = 2mm W/COVER	2	CHECKED BY	AMIR KHAN
			APPROVED BY	NASSER ANANI
			DATE	22-07-2026
			REF NO. :	
			CONSULTANT :	

TITLE: CABLE LADDER 30° DEG OUTSIDE RISER W COVER

CLIENT: KENT GAD

SEC ITEM NO:

BONN METAL CONS. IND.

BONN GROUP OF COMPANIES
Cable Management Systems

DWRG. NO. :


REV. 01

SHEET NO. :


SCALE:NTS


NOTE:-

MATERIAL HDG 2mm ALL flange 32 mm
Hot Dip Galvnaiztion 85 M without Epoxy
MIG WELDING
Cover Height 12mm

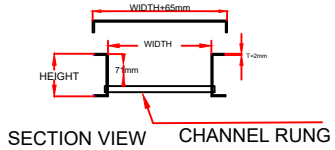


SECTION VIEW CHANNEL RUNG

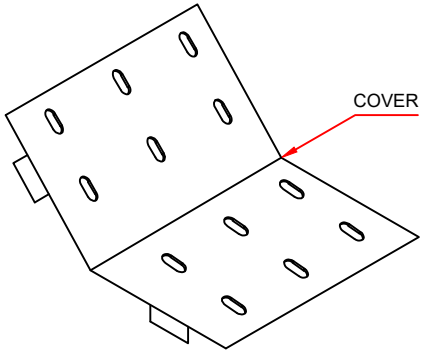


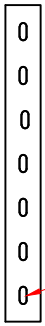


Obround 25X14

Rungs

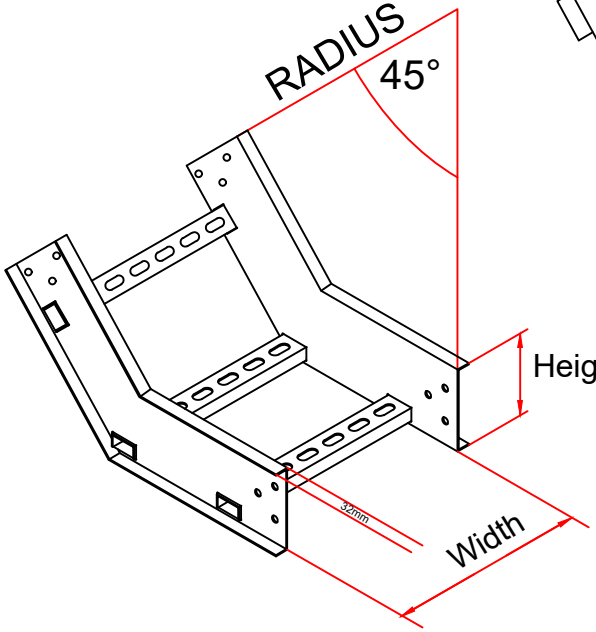

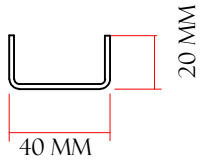

SIDE VIEW

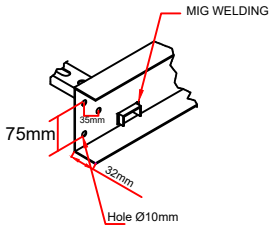

CABLE LADDER 45° DEG (V) INSIDE RISER

SN	DIMENSION TABLE	QTY	DRAWN BY	EZELDIN
425	W=300mm, H =100mm , R= 600mm , T = 2mm W/COVER	2	CHECKED BY	AMIR KHAN
			APPROVED BY	NASSER ANANI
			DATE	22-07-2026
			REF NO. :	
			CONSULTANT :	

TITLE: CABLE LADDER 45° DEG INSIDE RISER

CLIENT: KENT GAD

SEC ITEM NO:

BONN METAL CONS. IND.


BONN GROUP OF COMPANIES
Cable Management Systems

DWRG. NO. :


REV. 01

SHEET NO. :

SCALE:NTS

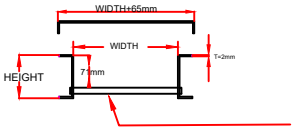


SECTION VIEW CHANNEL RUNG

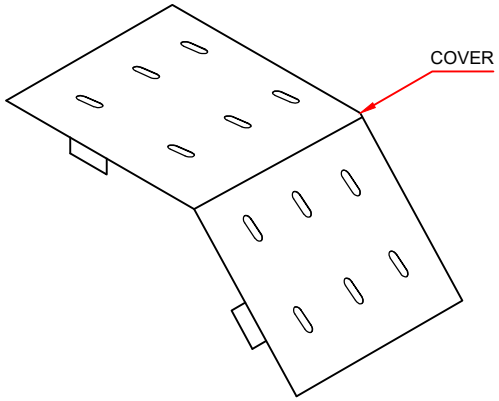


NOTE:-


MATERIAL HDG 2mm ALL flange 32 mm
Hot Dip Galvnaiztion 85 M without Epoxy
MIG WELDING
Cover Height 12mm

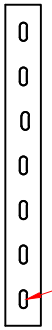


Obround 25X14

Rungs

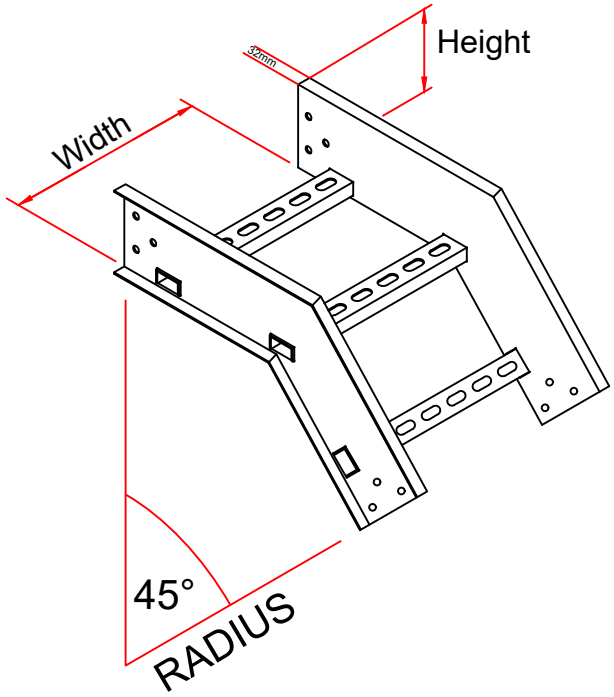

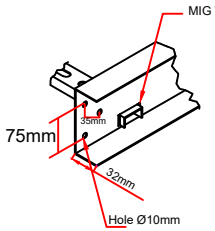

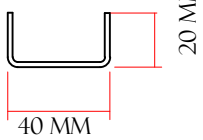

SIDE VIEW

CABLE LADDER 45° DEG (V) OUTSIDE RISER W COVER

SN	DIMENSION TABLE	QTY
426	W=300mm, H =100mm , R= 600mm , T = 2mm W/COVER	2

DRAWN BY	EZELDIN
CHECKED BY	AMIR KHAN
APPROVED BY	NASSER ANANI
DATE	22-07-2026
REF NO. :	
CONSULTANT :	

TITLE: CABLE LADDER 45° DEG OUTSIDE RISER W COVER

CLIENT: KENT GAD

SEC ITEM NO:

BONN METAL CONS. IND.

BONN GROUP OF COMPANIES
Cable Management Systems

DWRG. NO. :


REV. 01


SHEET NO. :


SCALE:NTS


NOTE:-


MATERIAL HDG 2mm ALL flange 32 mm
Hot Dip Galvnaiztion 85 M without Epoxy
MIG WELDING
Cover Height 12mm

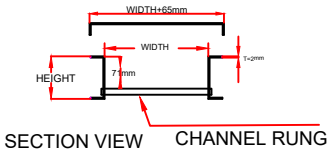


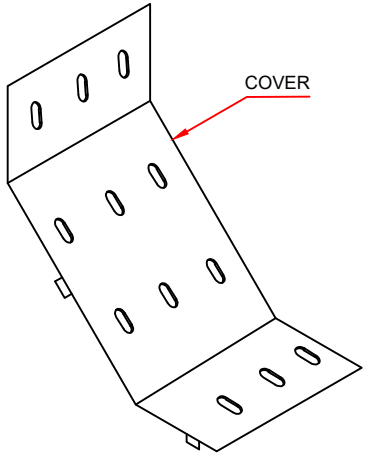

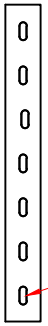

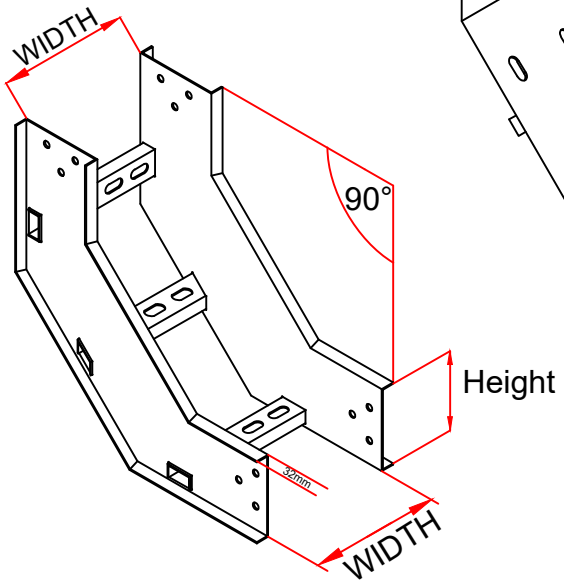

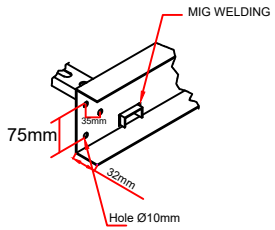

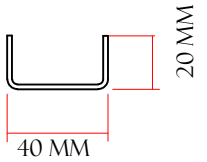

CABLE LADDER BEND 90° INSIDE RISER W/COVER

SN	DIMENSION TABLE	QTY
427	W=300mm, H =100mm , R= 300mm , T = 2mm W/COVER	2
428	W=300mm, H =100mm , R= 600mm , T = 2mm ,W/COVER	2
429	W=600mm, H =100mm , R= 600mm , T = 2mm , W/COVER	3
430	W=750mm, H =100mm , R= 900mm , T = 2mm , W/COVER	2

DRAWN BY	EZELDIN
CHECKED BY	AMIR KHAN
APPROVED BY	NASSER ANANI
DATE	22-07-2026
REF NO. :	
CONSULTANT :	

TITLE: CABLE LADDER BEND 90° INSIDE RISER W/COVER

CLIENT: KENT GAD

SEC ITEM NO:

BONN METAL CONS. IND.


BONN GROUP OF COMPANIES
Cable Management Systems

DWRG. NO. :

REV. 01

SHEET NO. :


SCALE:NTS

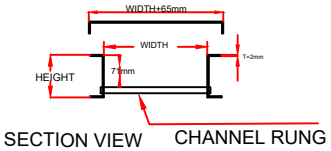



SECTION VIEW CHANNEL RUNG


NOTE:-


MATERIAL HDG 2mm ALL flange 32 mm
Hot Dip Galvnaiztion 85 M without Epoxy
MIG WELDING
Cover Height 12mm

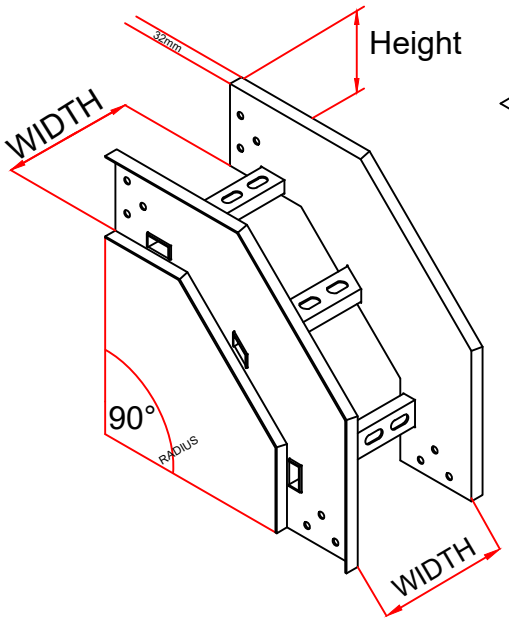

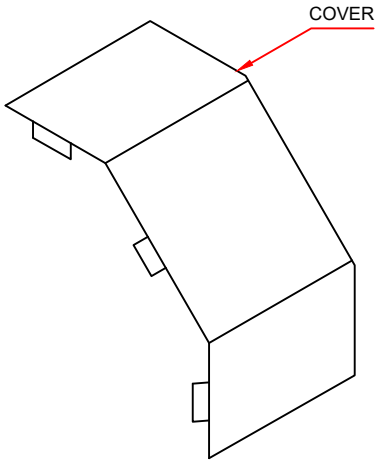

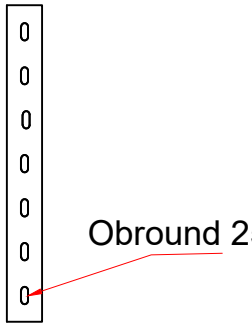

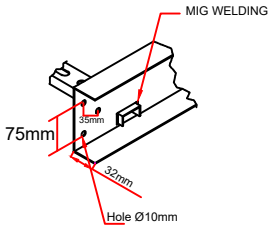

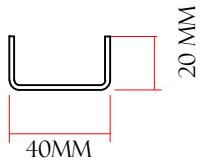

SIDE VIEW

CABLE LADDER BEND 90° OUTSIDE RISER W/COVER

SN	DIMENSION TABLE	QTY
431	W=300mm, H =100mm , R= 300mm , T = 2mm W/COVER	2
432	W=300mm, H =100mm , R= 600mm , T = 2mm ,W/COVER	3
433	W=600mm, H =100mm , R= 600mm , T = 2mm , W/COVER	3
434	W=750mm, H =100mm , R=900mm , T = 2mm , W/COVER	3

DRAWN BY	EZELDIN
CHECKED BY	AMIR KHAN
APPROVED BY	NASSER ANANI
DATE	22-07-2026
REF NO. :	
CONSULTANT :	

TITLE: CABLE LADDER BEND 90° OUTSIDE RISER W/COVER

CLIENT: KENT GAD

SEC ITEM NO:

BONN METAL CONS. IND.


BONN GROUP OF COMPANIES
Cable Management Systems

DWRG. NO. :


REV. 01

SHEET NO. :

SCALE:NTS

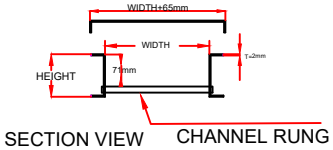


SECTION VIEW CHANNEL RUNG

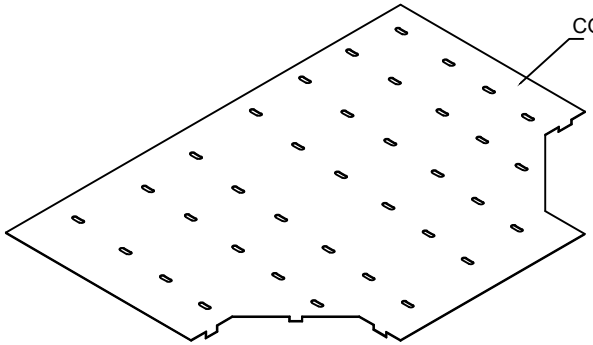


NOTE:-


MATERIAL HDG 2mm ALL flange 32 mm
Hot Dip Galvnaiztion 85 M without Epoxy
MIG WELDING
Cover Height 12mm

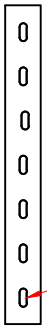


Obround 25X14

Rungs

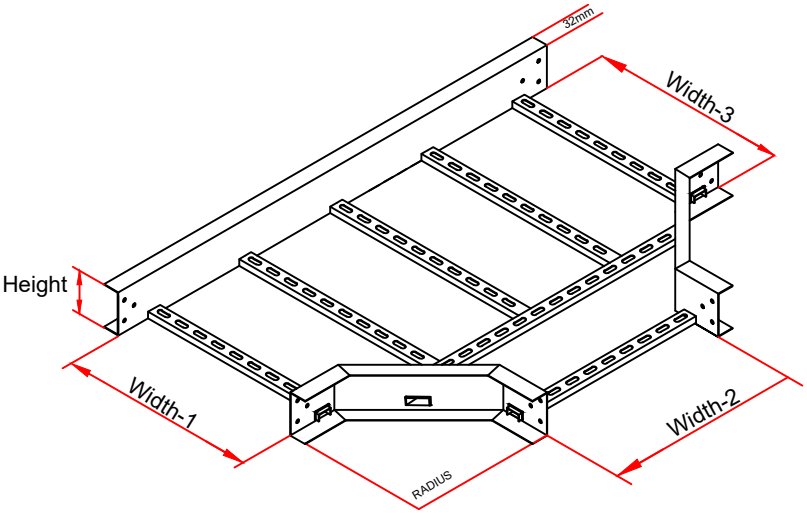

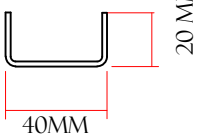

SIDE VIEW

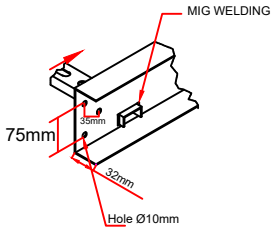

CABLE LADDER EQUAL TEE W/COVER

SN	DIMENSION TABLE	QTY
435	W=300mm, H =100mm , R= 600mm , T = 2mm W/COVER	2

DRAWN BY	EZELDIN
CHECKED BY	AMIR KHAN
APPROVED BY	NASSER ANANI
DATE	22-07-2026
REF NO. :	
CONSULTANT :	

TITLE: CABLE LADDER EQUAL TEE W/COVER

CLIENT: KENT GAD

SEC ITEM NO:

BONN METAL CONS. IND.


BONN GROUP OF COMPANIES
Cable Management Systems

DWRG. NO. :

REV. 01


SHEET NO. :

SCALE:NTS

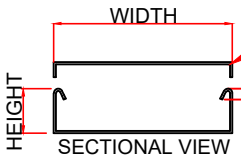

NOTE:-

MATERIAL HDG 2mm ALL flange inside 15 mm
Hot Dip Galvnaiztion 85 M without Epoxy
Cover Height 12mm

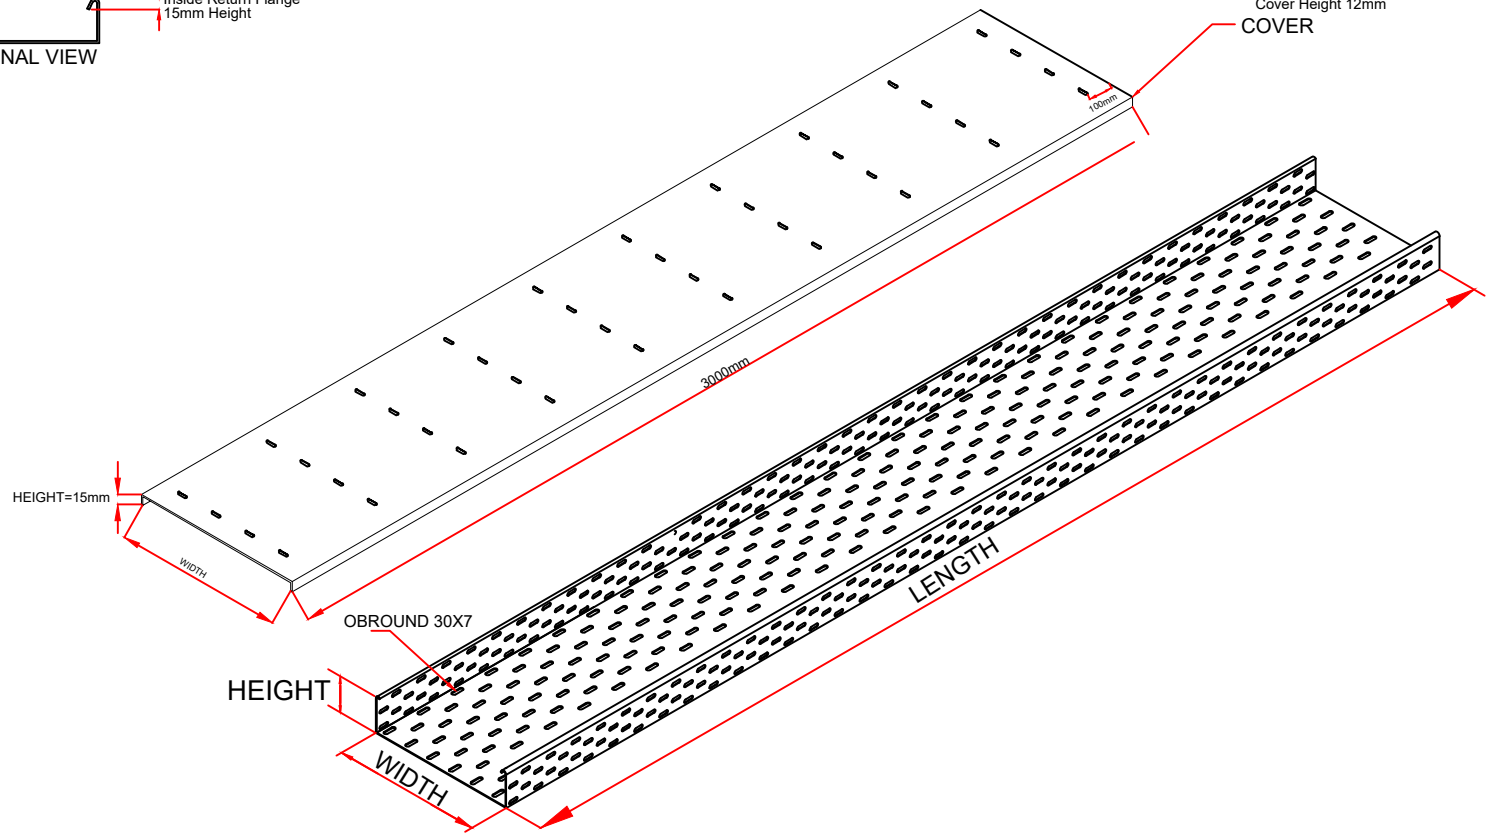

CABLE TRAY STRAIGHT LENGTH W/COVER

SN	DIMENSION TABLE	QTY
436	W=150mm, H =100mm , T = 2mm , W/COVER	867
437	W=100mm, H =100mm , T = 2mm , W/COVER	108
438	W=50mm, H =50mm , T = 2mm , W/COVER	134

DRAWN BY	EZELDIN
CHECKED BY	AMIR KHAN
APPROVED BY	NASSER ANANI
DATE	22-07-2026
REF NO. :	
CONSULTANT :	

TITLE: CABLE TRAY STRAIGHT LENGTH W/COVER

CLIENT: KENT GAD

SEC ITEM NO:

BONN METAL CONS. IND.


BONN GROUP OF COMPANIES
Cable Management Systems

DWRG. NO. :

REV. 01


SHEET NO. :


SCALE:NTS

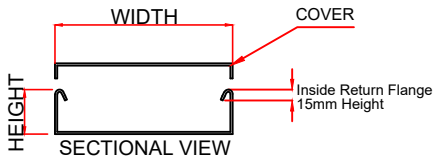

NOTE:-

MATERIAL HDG 2mm ALL flange inside 15 mm
Hot Dip Galvnaiztion 85 M without Epoxy
Cover Height 12mm

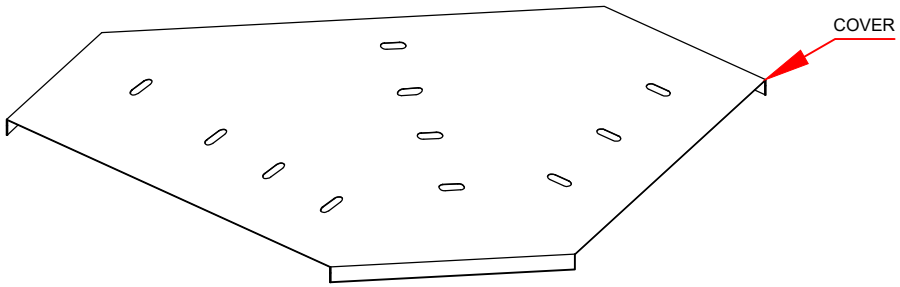

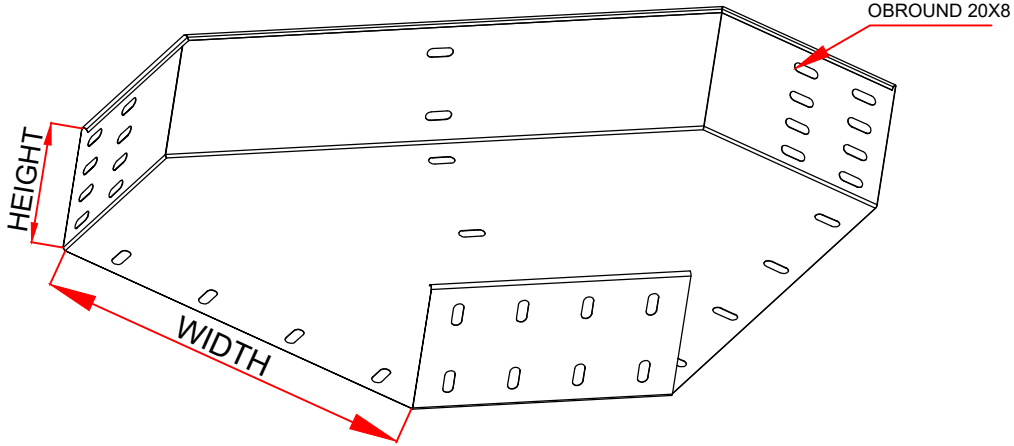

CABLE TRAY BEND 90DEG W/COVER

SN	DIMENSION TABLE	QTY
439	W=150mm, H =100mm , R= 300mm , T = 2mm W/COVER	24

DRAWN BY	EZELDIN
CHECKED BY	AMIR KHAN
APPROVED BY	NASSER ANANI
DATE	22-07-2026
REF NO. :	
CONSULTANT :	

TITLE: CABLE TRAY BEND 90DEG W/COVER

CLIENT: KENT GAD

SEC ITEM NO:

BONN METAL CONS. IND.


BONN GROUP OF COMPANIES
Cable Management Systems

DWRG. NO. :

REV. 01


SHEET NO. :

SCALE:NTS

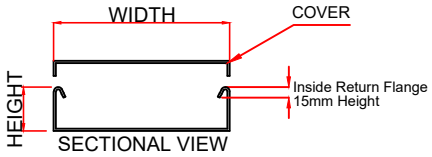

NOTE:-

MATERIAL HDG 2mm ALL flange inside 15 mm
Hot Dip Galvnaiztion 85 M without Epoxy
Cover Height 12mm

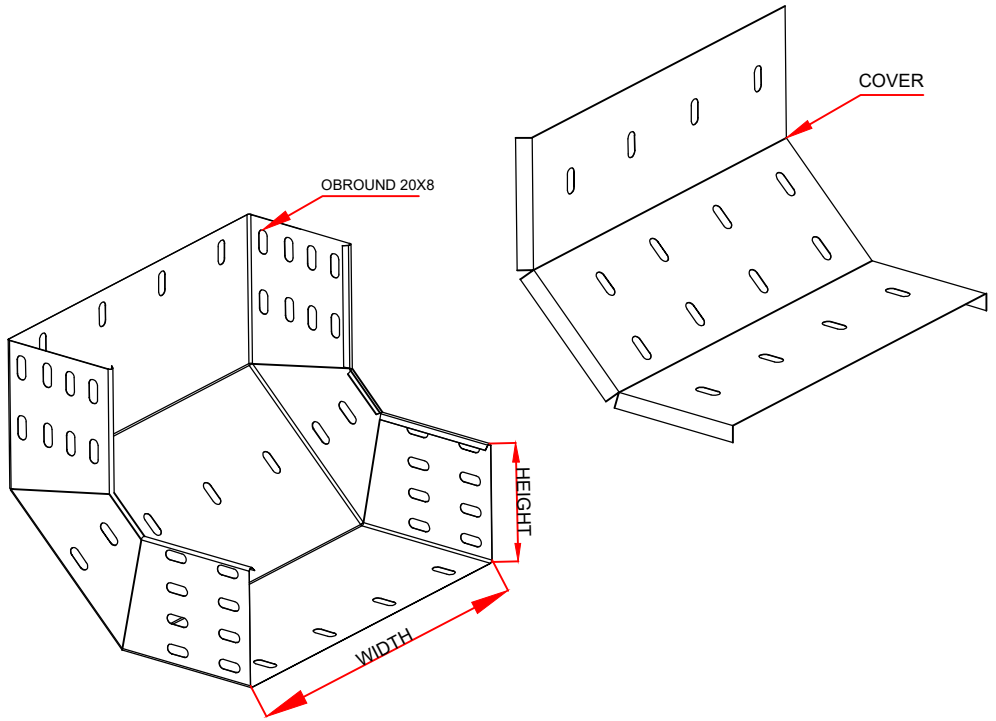

CABLE TRAY INSIDE RISER 90DEG

SN	DIMENSION TABLE	QTY
440	W=150mm, H =100mm , R= 300mm , T = 2mm W/COVER	14
441	W=150mm, H =100mm , R= 600mm , T = 2mm W/COVER	2

DRAWN BY	EZELDIN
CHECKED BY	AMIR KHAN
APPROVED BY	NASSER ANANI
DATE	22-07-2026
REF NO. :	
CONSULTANT :	

TITLE: CABLE TRAY INSIDE RISER 90DEG

CLIENT: KENT GAD

SEC ITEM NO:

BONN METAL CONS. IND.


BONN GROUP OF COMPANIES
Cable Management Systems

DWRG. NO. :

REV. 01


SHEET NO. :


SCALE:NTS

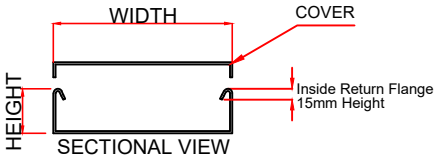

NOTE:-

MATERIAL HDG 2mm ALL flange inside 15 mm
Hot Dip Galvnaiztion 85 M without Epoxy
Cover Height 12mm

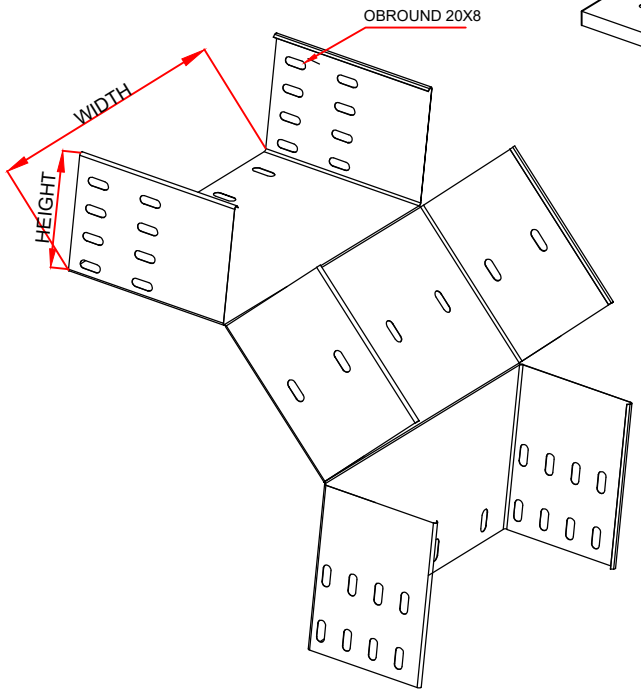

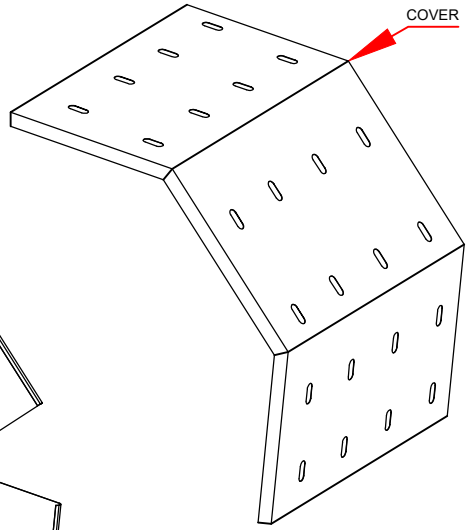

CABLE TRAY OUTSIDE RISER 90DEG

SN	DIMENSION TABLE	QTY
442	W=150mm, H =100mm , R= 300mm , T = 2mm W/COVER	21

DRAWN BY	EZELDIN
CHECKED BY	AMIR KHAN
APPROVED BY	NASSER ANANI
DATE	22-07-2026
REF NO. :	
CONSULTANT :	

TITLE: CABLE TRAY OUTSIDE RISER 90DEG

CLIENT: KENT GAD

SEC ITEM NO:

BONN METAL CONS. IND.


BONN GROUP OF COMPANIES
Cable Management Systems

DWRG. NO. :

REV. 01


SHEET NO. :

SCALE:NTS

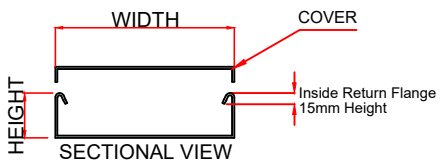

NOTE:-

MATERIAL HDG 2mm ALL flange inside 15 mm
Hot Dip Galvnaiztion 85 M without Epoxy
Cover Height 12mm

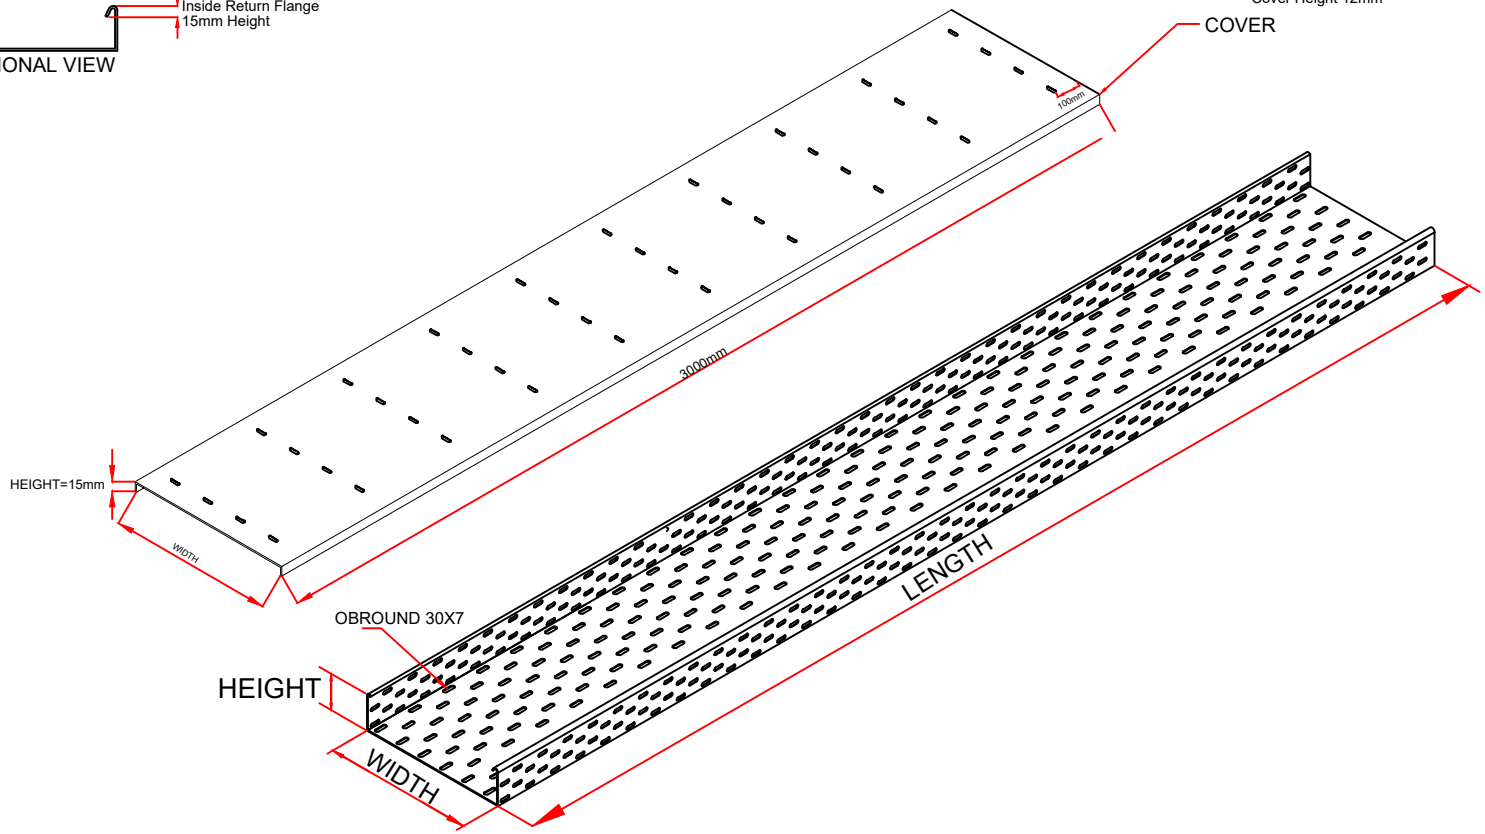

CABLE TRAY STRAIGHT LENGTH W/COVER

SN	DIMENSION TABLE	QTY
443	W=150mm, H =100mm , T = 2mm , W/COVER	694
444	W=100mm, H =100mm , T = 2mm , W/COVER	87
445	W=50mm, H =50mm , T = 2mm , W/COVER	108

DRAWN BY	EZELDIN
CHECKED BY	AMIR KHAN
APPROVED BY	NASSER ANANI
DATE	22-07-2026
REF NO. :	
CONSULTANT :	

TITLE: CABLE TRAY STRAIGHT LENGTH W/COVER

CLIENT: KENT GAD

SEC ITEM NO:

BONN METAL CONS. IND.


BONN GROUP OF COMPANIES
Cable Management Systems

DWRG. NO. :

REV. 01


SHEET NO. :


SCALE:NTS

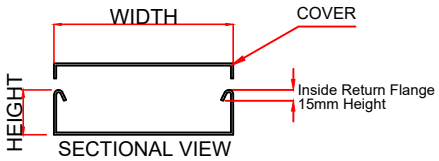

NOTE:-

MATERIAL HDG 2mm ALL flange inside 15 mm
Hot Dip Galvnaiztion 85 M without Epoxy
Cover Height 12mm

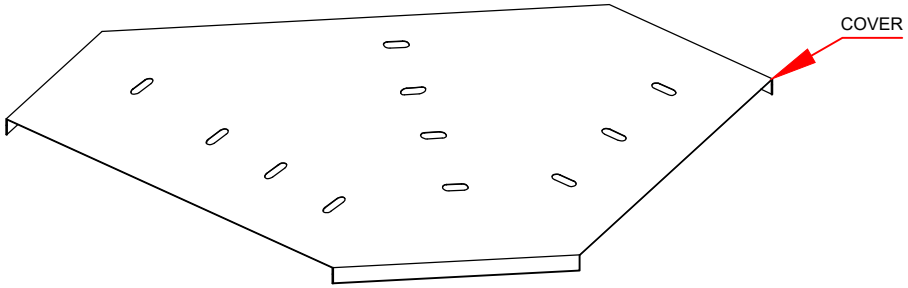

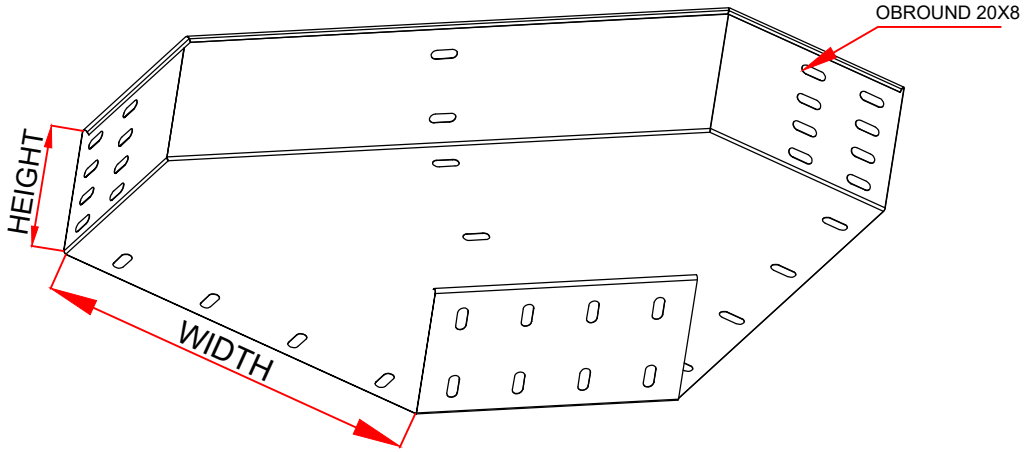

CABLE TRAY BEND 90DEG W/COVER

SN	DIMENSION TABLE	QTY
446	W=150mm, H =100mm , R= 300mm , T = 2mm W/COVER	10

DRAWN BY	EZELDIN
CHECKED BY	AMIR KHAN
APPROVED BY	NASSER ANANI
DATE	22-07-2026
REF NO. :	
CONSULTANT :	

TITLE: CABLE TRAY BEND 90DEG W/COVER

CLIENT: KENT GAD

SEC ITEM NO:

BONN METAL CONS. IND.


BONN GROUP OF COMPANIES
Cable Management Systems

DWRG. NO. :

REV. 01


SHEET NO. :

SCALE:NTS

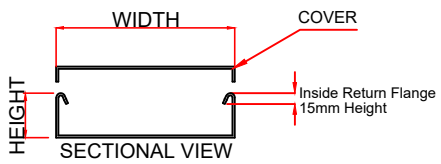

NOTE:-

MATERIAL HDG 2mm ALL flange inside 15 mm
Hot Dip Galvnaiztion 85 M without Epoxy
Cover Height 12mm

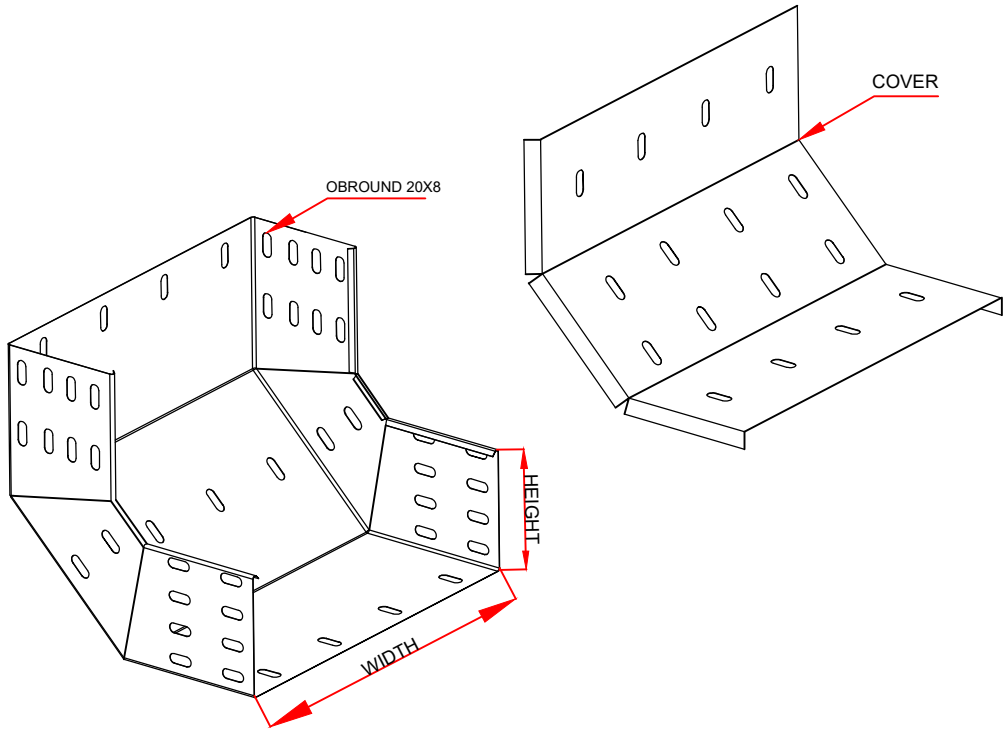

CABLE TRAY INSIDE RISER 90DEG

SN	DIMENSION TABLE	QTY
447	W=150mm, H =100mm , R= 300mm , T = 2mm W/COVER	7
448	W=150mm, H =100mm , R= 600mm , T = 2mm W/COVER	2

DRAWN BY	EZELDIN
CHECKED BY	AMIR KHAN
APPROVED BY	NASSER ANANI
DATE	22-07-2026
REF NO. :	
CONSULTANT :	

TITLE: CABLE TRAY INSIDE RISER 90DEG


CLIENT: KENT GAD

SEC ITEM NO:

BONN METAL CONS. IND.


BONN GROUP OF COMPANIES
Cable Management Systems


DWRG. NO. :		REV.
SHEET NO. :	SCALE:NTS	01

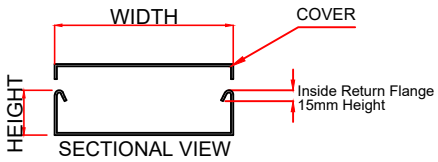

NOTE:-

MATERIAL HDG 2mm ALL flange inside 15 mm
Hot Dip Galvnaiztion 85 M without Epoxy
Cover Height 12mm

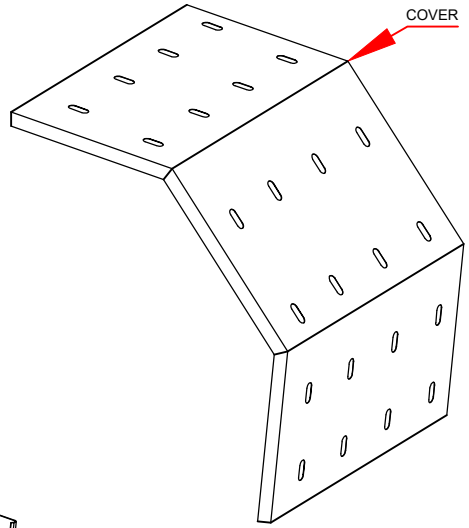

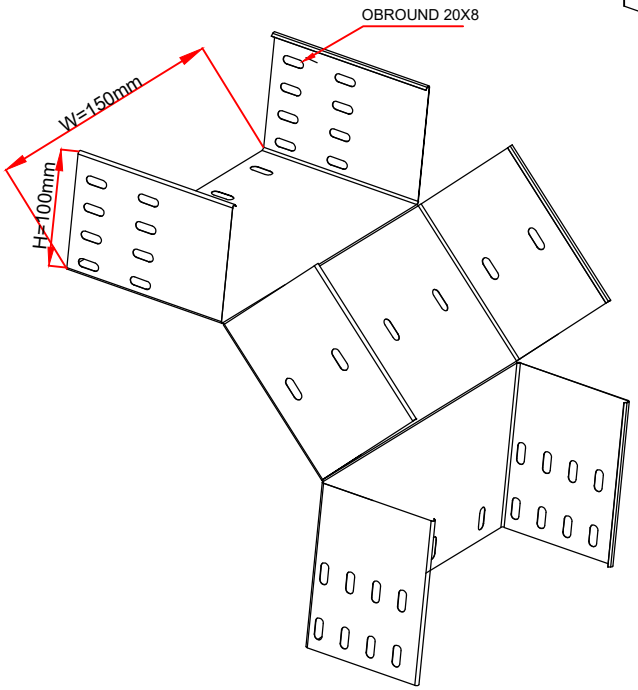

CABLE TRAY OUTSIDE RISER 90DEG

SN	DIMENSION TABLE	QTY
449	W=150mm, H =100mm , R= 300mm , T = 2mm W/COVER	14

DRAWN BY	EZELDIN
CHECKED BY	AMIR KHAN
APPROVED BY	NASSER ANANI
DATE	22-07-2026
REF NO. :	
CONSULTANT :	

TITLE: CABLE TRAY OUTSIDE RISER 90DEG

CLIENT: KENT GAD

SEC ITEM NO:


BONN METAL CONS. IND.

BONN GROUP OF COMPANIES
Cable Management Systems


DWRG. NO. :		REV.
SHEET NO. :	SCALE:NTS	01

NOTE:-


MATERIAL HDG 2mm HARDWARES SS316
Hot Dip Galvnaiztion 85 M without Epoxy

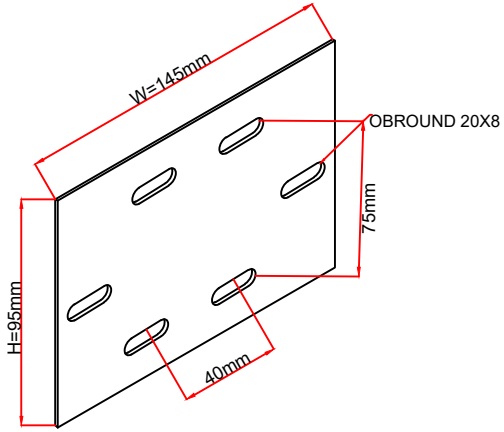


CABLE LADDER COUPLER

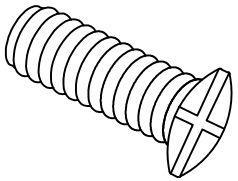

ROOFING BOLT
M6X16

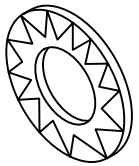

Washers M6

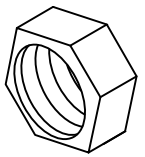

Nuts M6


CABLE LADDER COUPLER


SN	DIMENSION TABLE	QTY	DRAWN BY	EZELDIN	TITLE: CABLE LADDER COUPLER	BONN METAL CONS. IND.
450	W=145mm, H =95mm , T = 2mm	1656	CHECKED BY	AMIR KHAN		
			APPROVED BY	NASSER ANANI	CLIENT: KENT GAD	
			DATE	22-07-2026		
			REF NO. :		SEC ITEM NO:	DWRG. NO. : / REV. 01
			CONSULTANT :			SHEET NO. : / SCALE:NTS

BONN GROUP OF COMPANIES
Cable Management Systems


NOTE:-

MATERIAL HDG 2mm HARDWARES SS316
Hot Dip Galvnaiztion 85 M without Epoxy

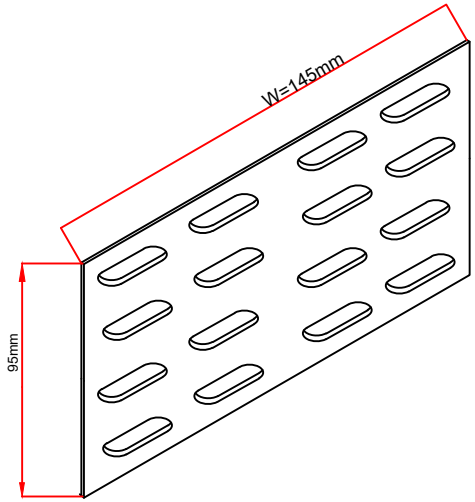


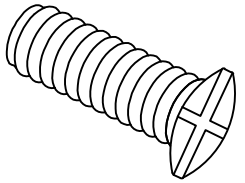

ROOFING BOLT
M6X16

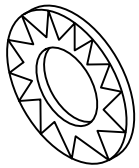

Washers M6

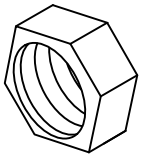

Nuts M6

CABLE TRAY EXPANSION COUPLER

SN	DIMENSION TABLE	QTY
451	W=145mm, H =95mm , T = 2mm	24

DRAWN BY	EZELDIN
CHECKED BY	AMIR KHAN
APPROVED BY	NASSER ANANI
DATE	22-07-2026
REF NO. :	
CONSULTANT :	

TITLE: CABLE TRAY EXPANSION COUPLER

CLIENT: KENT GAD

SEC ITEM NO:

BONN METAL CONS. IND.


BONN GROUP OF COMPANIES
Cable Management Systems

DWRG. NO. :		REV.
SHEET NO. :	SCALE:NTS	01


NOTE:-

MATERIAL SS316 2mm


Hardwares SS316

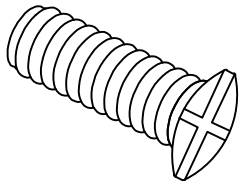


ROOFING BOLT
M8X30

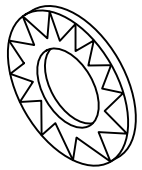

Washers M8

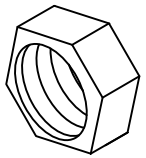

Nuts M8

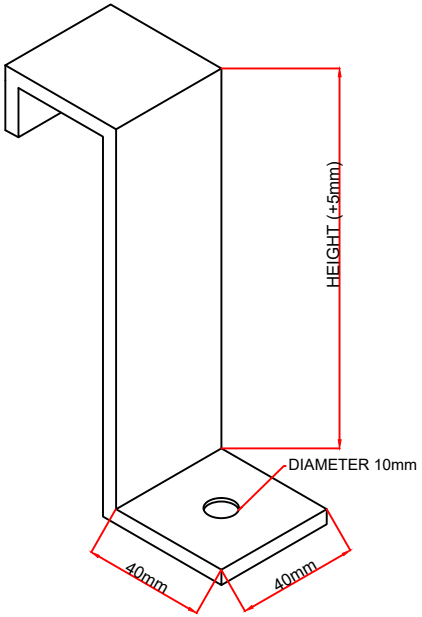

CABLE LADDER HOLD DOWN CLAMP

SN	DIMENSION TABLE	QTY
452	W=40mm, H =100+5mm , T = 2mm	2514

DRAWN BY	EZELDIN
CHECKED BY	AMIR KHAN
APPROVED BY	NASSER ANANI
DATE	22-07-2026
REF NO. :	
CONSULTANT :	

TITLE: CABLE LADDER HOLD DOWN CLAMP

CLIENT: KENT GAD

SEC ITEM NO:

BONN METAL CONS. IND.

BONN GROUP OF COMPANIES
Cable Management Systems

DWRG. NO. :


REV. 01


SHEET NO. :

SCALE:NTS


NOTE:-

MATERIAL HDG 2mm HARDWARES SS316
Hot Dip Galvnaiztion 85 M without Epoxy

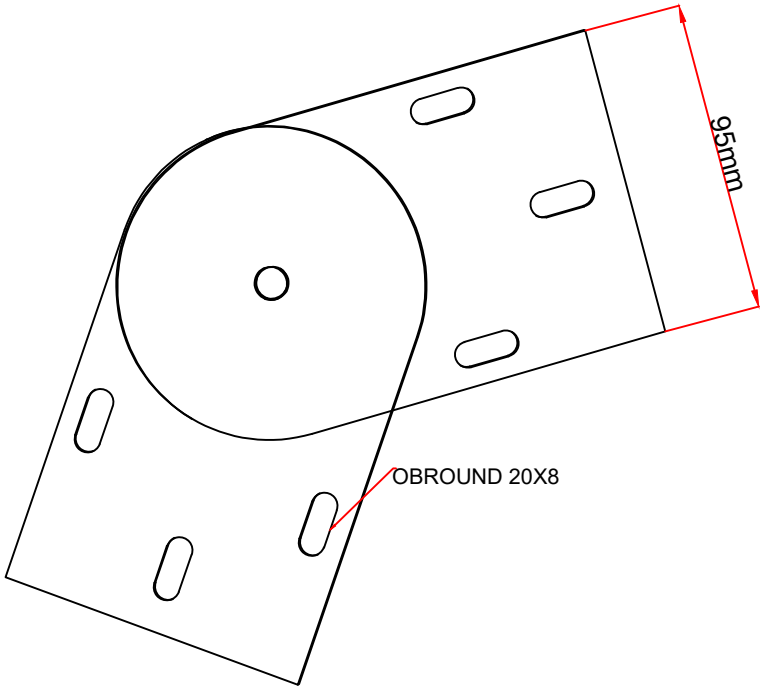


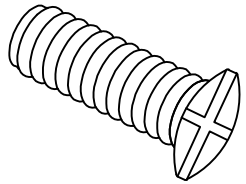

ROOFING BOLT
M6X16

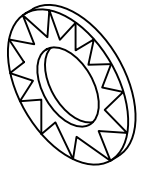

Washers M6

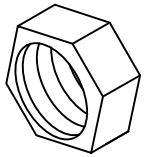

Nuts M6

CABLE LADDER ADJUSTABLE VERTICAL COUPLER

SN	DIMENSION TABLE	QTY
453	H=100mm & T=2.0mm	84

DRAWN BY	EZELDIN
CHECKED BY	AMIR KHAN
APPROVED BY	NASSER ANANI
DATE	22-07-2026
REF NO. :	
CONSULTANT :	

TITLE: CABLE LADDER ADJUSTABLE VERTICAL COUPLER

CLIENT: KENT GAD

SEC ITEM NO:

BONN METAL CONS. IND.

BONN GROUP OF COMPANIES
Cable Management Systems

DWRG. NO. :


REV. 01


SHEET NO. :

SCALE:NTS


NOTE:-

MATERIAL HDG 2mm HARDWARES SS316
Hot Dip Galvnaiztion 85 M without Epoxy

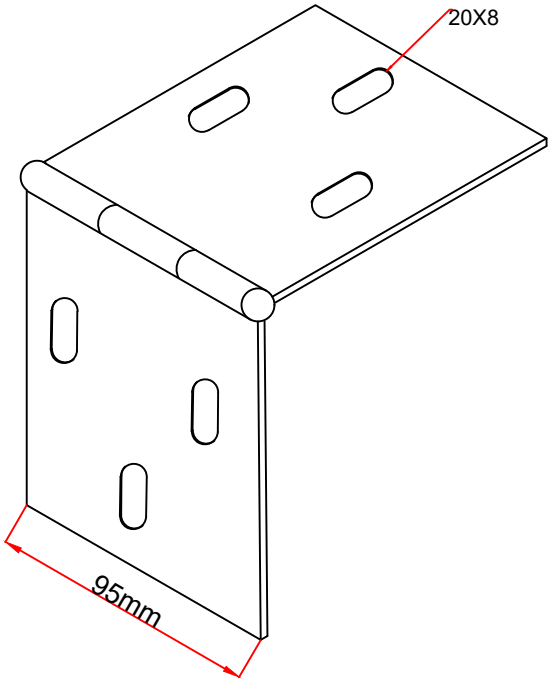


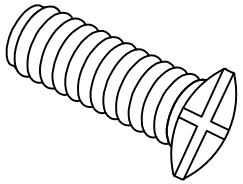

ROOFING BOLT
M6X16

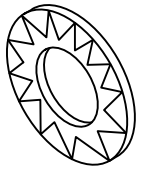

Washers M6

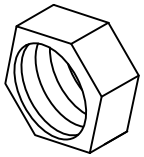

Nuts M6


CABLE LADDER ADJUSTABLE HORIZONTAL COUPLER


SN	DIMENSION TABLE	QTY	DRAWN BY	EZELDIN	TITLE: CABLE LADDER ADJUSTABLE HORIZONTAL COUPLER	BONN METAL CONS. IND.
454	H=100mm & T=2.0mm	84	CHECKED BY	AMIR KHAN		
			APPROVED BY	NASSER ANANI	CLIENT: KENT GAD	
			DATE	22-07-2026		
			REF NO. :		SEC ITEM NO:	DWRG. NO. : REV. 01
			CONSULTANT :			SHEET NO. : SCALE:NTS

BONN GROUP OF COMPANIES
Cable Management Systems


NOTE:-

MATERIAL HDG 2mm HARDWARES SS316
Hot Dip Galvnaiztion 85 M without Epoxy

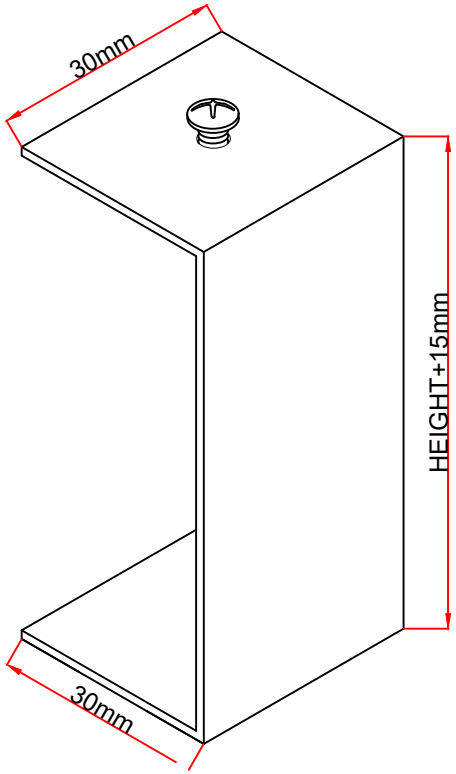


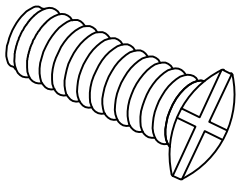

ROOFING BOLT
M6X16

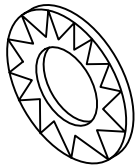

Washers M6

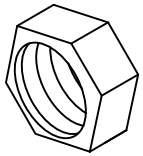

Nuts M6

Cable Ladder cover Holding Clamps

SN	DIMENSION TABLE	QTY	DRAWN BY	EZELDIN
455	W=30mm, H =100+5mm , T = 2mm	803	CHECKED BY	AMIR KHAN
			APPROVED BY	NASSER ANANI
			DATE	22-07-2026
			REF NO. :	
			CONSULTANT :	

TITLE: Cable Ladder cover Holding Clamps

CLIENT: KENT GAD

SEC ITEM NO:

BONN METAL CONS. IND.

BONN GROUP OF COMPANIES
Cable Management Systems

DWRG. NO. :


REV. 01


SHEET NO. :

SCALE:NTS


NOTE:-

MATERIAL HDG 2mm HARDWARES SS316
Hot Dip Galvnaiztion 85 M without Epoxy

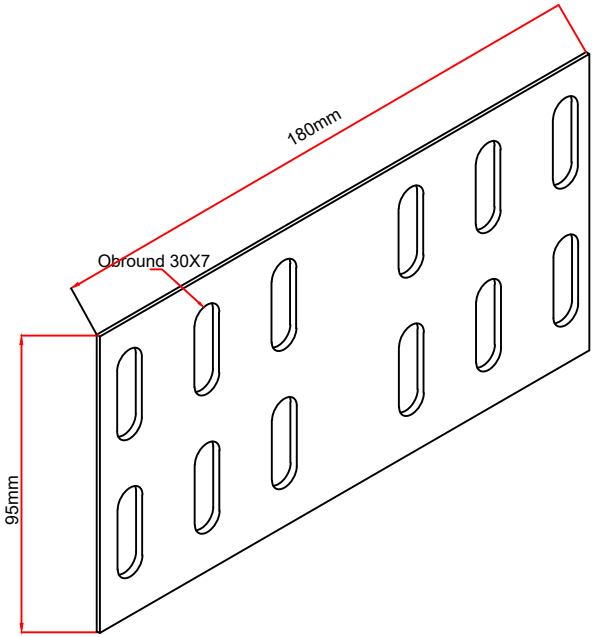


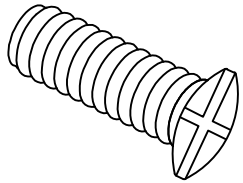

ROOFING BOLT
M6X16

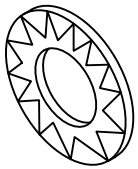

Washers M6

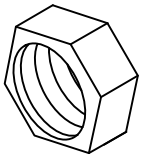

Nuts M6

CABLE TRAY STRAIGHT COUPLER

SN	DIMENSION TABLE	QTY
456	W=180mm, H =95mm , T = 2mm	2064

DRAWN BY	EZELDIN
CHECKED BY	AMIR KHAN
APPROVED BY	NASSER ANANI
DATE	22-07-2026
REF NO. :	
CONSULTANT :	

TITLE: CABLE TRAY STRAIGHT COUPLER

CLIENT: KENT GAD

SEC ITEM NO:


BONN METAL CONS. IND.


BONN GROUP OF COMPANIES
Cable Management Systems

DWRG. NO. :		REV.
SHEET NO. :	SCALE:NTS	01


NOTE:-

MATERIAL HDG 2mm HARDWARES SS316
Hot Dip Galvnaiztion 85 M without Epoxy

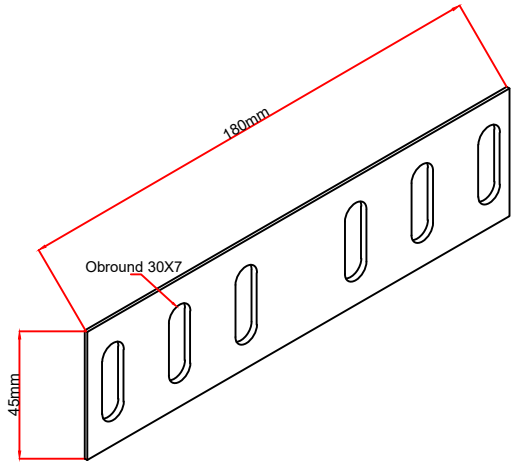


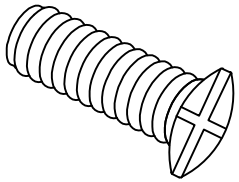

ROOFING BOLT
M6X16

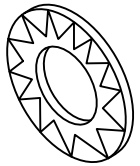

Washers M6

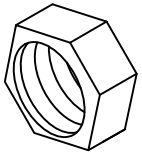

Nuts M6


CABLE TRAY STRAIGHT COUPLER


SN	DIMENSION TABLE	QTY	DRAWN BY	EZELDIN	TITLE:	BONN METAL CONS. IND.
457	W=180mm, H =45mm , T = 2mm	42	CHECKED BY	AMIR KHAN		
			APPROVED BY	NASSER ANANI	CLIENT: KENT GAD	
			DATE	22-07-2026		
			REF NO. :		SEC ITEM NO:	DWRG. NO. : REV. 01
			CONSULTANT :			SHEET NO. : SCALE:NTS

BONN GROUP OF COMPANIES
Cable Management Systems


NOTE:-

MATERIAL HDG 2mm HARDWARES SS316
Hot Dip Galvnaiztion 85 M without Epoxy

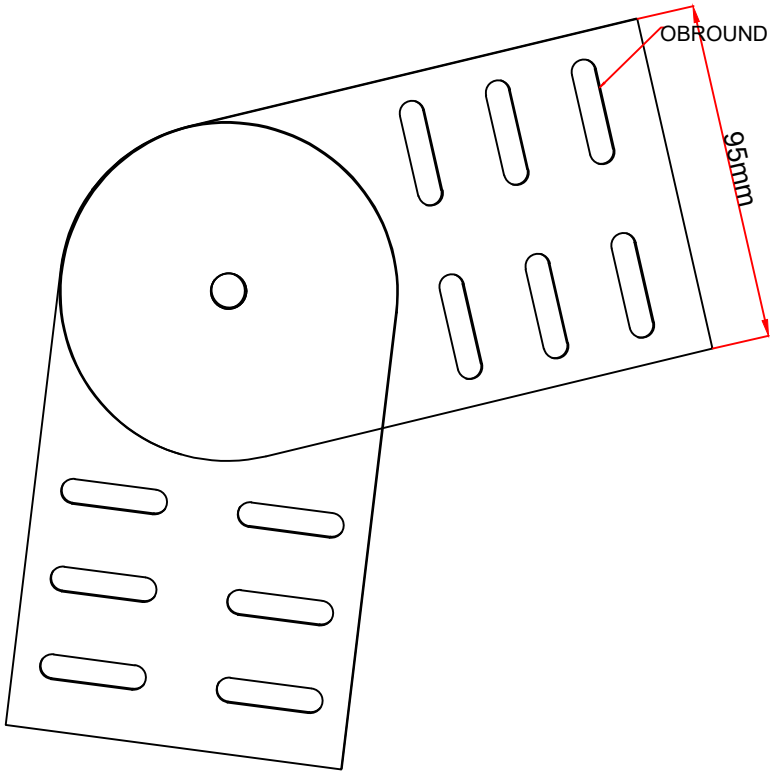


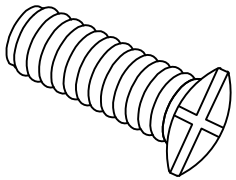

ROOFING BOLT
M6X16

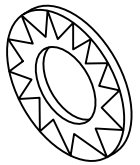

Washers M6

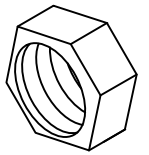

Nuts M6

CABLE TRAY VERTICAL ADJUSTABLE COUPLER

SN	DIMENSION TABLE	QTY
458	H=100mm & T=2.0mm	108

DRAWN BY	EZELDIN
CHECKED BY	AMIR KHAN
APPROVED BY	NASSER ANANI
DATE	22-07-2026
REF NO. :	
CONSULTANT :	

TITLE: CABLE TRAY VERTICAL ADJUSTABLE COUPLER

CLIENT: KENT GAD

SEC ITEM NO:

BONN METAL CONS. IND.

BONN GROUP OF COMPANIES
Cable Management Systems

DWRG. NO. :


SHEET NO. :


SCALE:NTS

REV. 01


NOTE:-

MATERIAL HDG 2mm HARDWARES SS316
Hot Dip Galvnaiztion 85 M without Epoxy

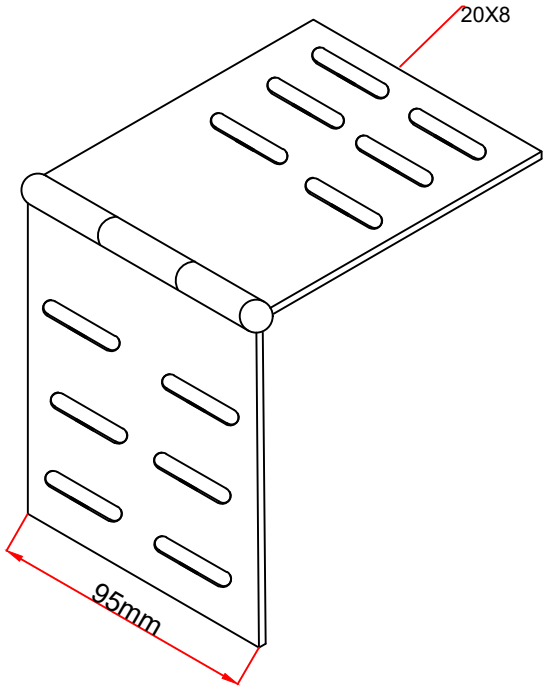


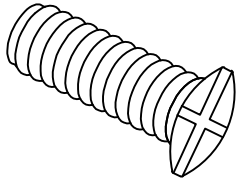

ROOFING BOLT
M6X16

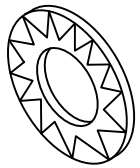

Washers M6

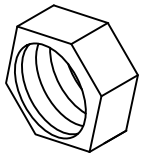

Nuts M6


CABLE TRAY ADJUSTABLE HORIZONTAL COUPLER

SN	DIMENSION TABLE	QTY	DRAWN BY	EZELDIN	TITLE: CABLE TRAY ADJUSTABLE HORIZONTAL COUPLER	BONN METAL CONS. IND.
459	H=100mm & T=2.0mm	108	CHECKED BY	AMIR KHAN		
			APPROVED BY	NASSER ANANI	CLIENT: KENT GAD	
			DATE	22-07-2026		
			REF NO. :		SEC ITEM NO:	DWRG. NO. : / REV. 01
			CONSULTANT :			SHEET NO. : / SCALE:NTS


BONN GROUP OF COMPANIES
Cable Management Systems

NOTE:-


MATERIAL HDG 2mm HARDWARES SS316
Hot Dip Galvnaiztion 85 M without Epoxy

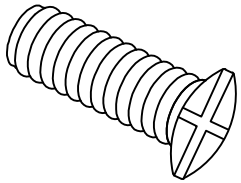


ROOFING BOLT
M8X30

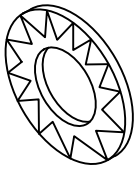

Washers M8

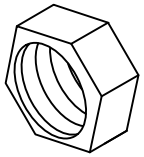

Nuts M8

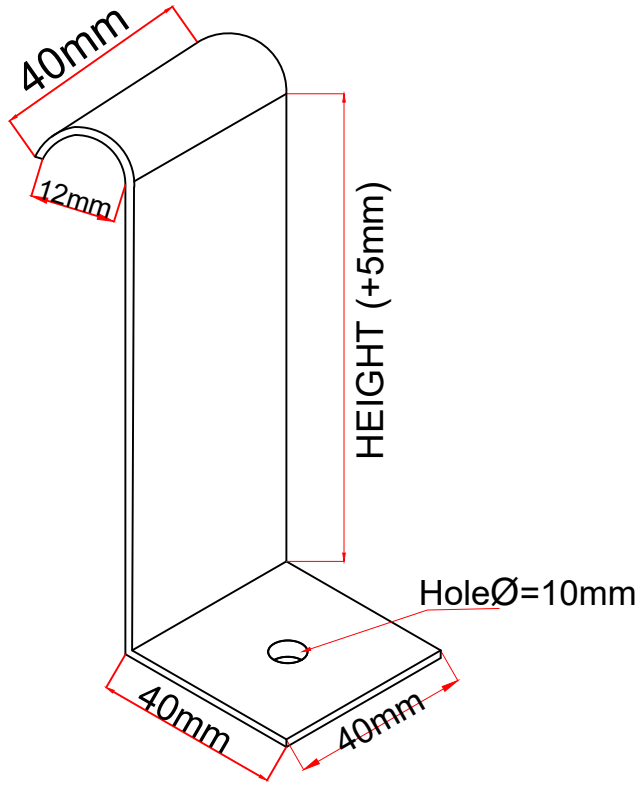

CABLE TRAY HOLD DOWN CLAMP

SN	DIMENSION TABLE	QTY
460	W=40mm, H =100+5mm , T = 2mm	2814

DRAWN BY	EZELDIN
CHECKED BY	AMIR KHAN
APPROVED BY	NASSER ANANI
DATE	22-07-2026
REF NO. :	
CONSULTANT :	

TITLE: CABLE TRAY HOLD DOWN CLAMP

CLIENT: KENT GAD

SEC ITEM NO:

BONN METAL CONS. IND.

BONN GROUP OF COMPANIES
Cable Management Systems

DWRG. NO. :


REV. 01

SHEET NO. :

SCALE:NTS

NOTE:-

MATERIAL HDG 2mm HARDWARES SS316
Hot Dip Galvnaiztion 85 M without Epoxy

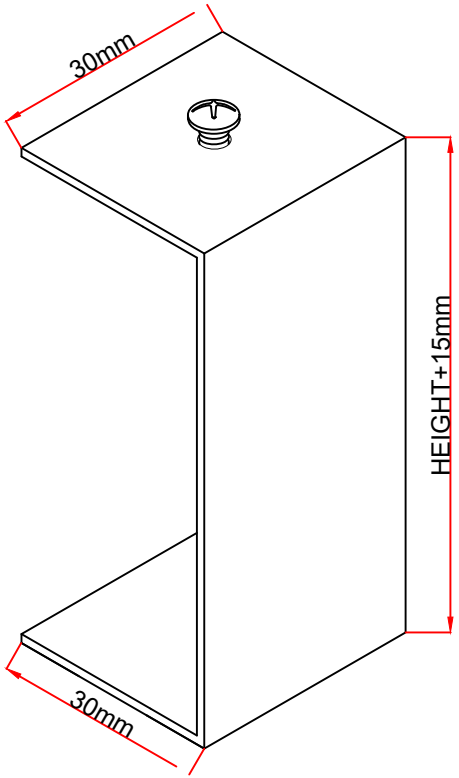



Cable Ladder cover Holding Clamps

SN	DIMENSION TABLE	QTY	DRAWN BY	EZELDIN	TITLE: Cable Ladder cover Holding Clamps	BONN METAL CONS. IND.
461	W=30mm, H =100+5mm , T = 2mm	4745	CHECKED BY	AMIR KHAN		
			APPROVED BY	NASSER ANANI	CLIENT: KENT GAD	
			DATE	22-07-2026		
			REF NO. :		SEC ITEM NO:	DWRG. NO. : REV. 01
			CONSULTANT :			SHEET NO. : SCALE:NTS


BONN GROUP OF COMPANIES
Cable Management Systems

MATERIAL HDG 2mm HARDWARES SS316
Hot Dip Galvnaiztion 85 M without Epoxy

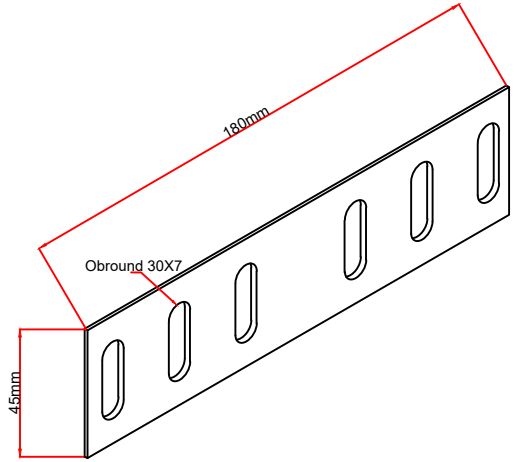


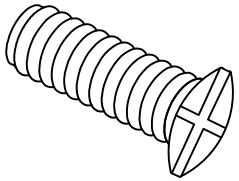

ROOFING BOLT
M6X16

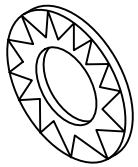

Washers M6

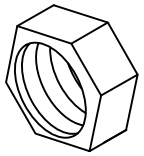

Nuts M6


CABLE TRAY STRAIGHT COUPLER


SN	DIMENSION TABLE	QTY	DRAWN BY	EZELDIN	TITLE: CABLE TRAY STRAIGHT COUPLER	BONN METAL CONS. IND.
462	W=180mm, H =45mm , T = 2mm	270	CHECKED BY	AMIR KHAN		
			APPROVED BY	NASSER ANANI	CLIENT: KENT GAD	
			DATE	22-07-2026		
			REF NO. :		SEC ITEM NO:	DWRG. NO. : / REV. 01
			CONSULTANT :			SHEET NO. : / SCALE:NTS

BONN GROUP OF COMPANIES
Cable Management Systems


NOTE:-

MATERIAL HDG 2mm HARDWARES SS316
Hot Dip Galvnaiztion 85 M without Epoxy

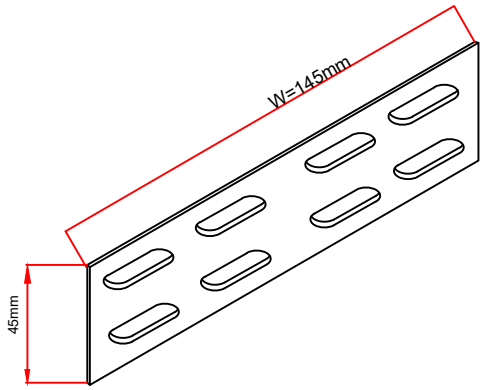


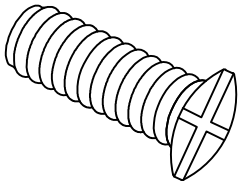

ROOFING BOLT
M6X16

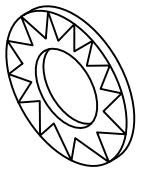

Washers M6

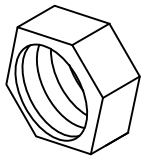

Nuts M6

CABLE TRAY EXPANSION COUPLER

SN	DIMENSION TABLE	QTY
463	W=145mm, H =95mm , T = 2mm	6

DRAWN BY	EZELDIN
CHECKED BY	AMIR KHAN
APPROVED BY	NASSER ANANI
DATE	22-07-2026
REF NO. :	
CONSULTANT :	

TITLE: CABLE TRAY EXPANSION COUPLER

CLIENT: KENT GAD

SEC ITEM NO:

BONN METAL CONS. IND.

BONN GROUP OF COMPANIES
Cable Management Systems

DWRG. NO. :


REV. 01


SHEET NO. :

SCALE:NTS


NOTE:-

MATERIAL HDG 2mm HARDWARES SS316
Hot Dip Galvnaiztion 85 M without Epoxy

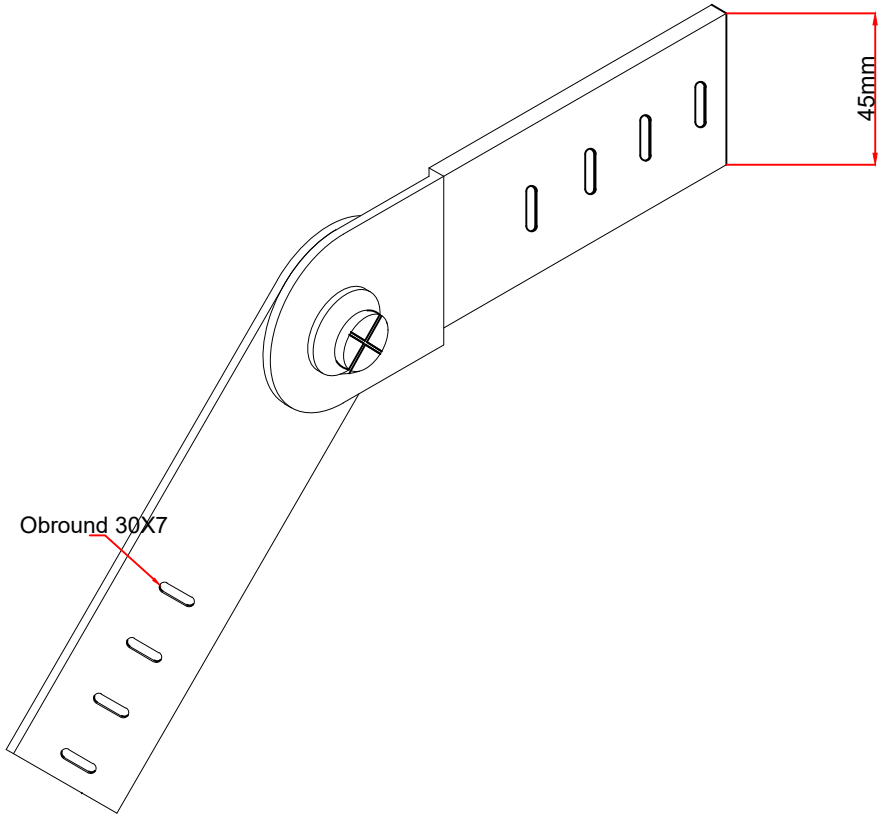


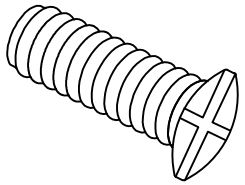

ROOFING BOLT
M6X16

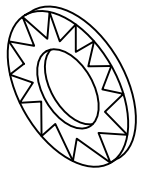

Washers M6

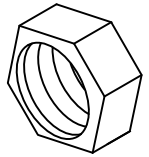

Nuts M6


CABLE TRAY VERTICAL ADJUSTABLE COUPLER


SN	DIMENSION TABLE	QTY	DRAWN BY	EZELDIN	TITLE: CABLE TRAY VERTICAL ADJUSTABLE COUPLER	BONN METAL CONS. IND.
464	H=45mm & T=2.0mm	18	CHECKED BY	AMIR KHAN		
			APPROVED BY	NASSER ANANI	CLIENT: KENT GAD	
			DATE	22-07-2026		
			REF NO. :		SEC ITEM NO:	DWRG. NO. : / REV. 01
			CONSULTANT :			SHEET NO. : / SCALE:NTS

BONN GROUP OF COMPANIES
Cable Management Systems


NOTE:-

MATERIAL HDG 2mm HARDWARES SS316
Hot Dip Galvnaiztion 85 M without Epoxy

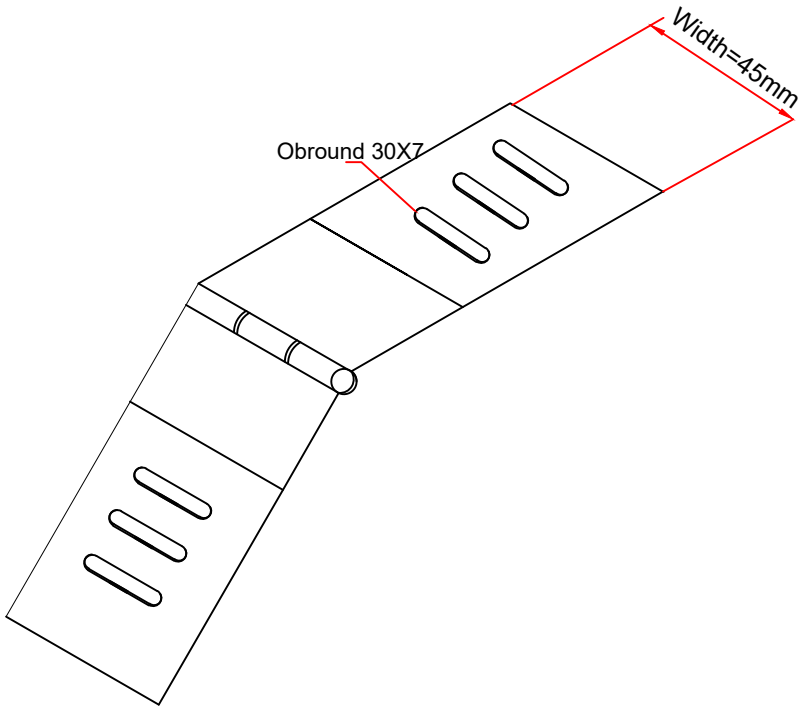


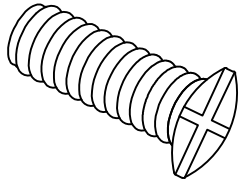

ROOFING BOLT
M6X16

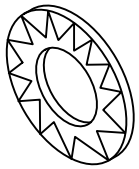

Washers M6

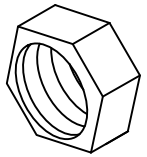

Nuts M6


CABLE TRAY HORIZONTAL ADJUSTABLE COUPLER

SN	DIMENSION TABLE	QTY	DRAWN BY	EZELDIN	TITLE: CABLE TRAY HORIZONTAL ADJUSTABLE COUPLER	BONN METAL CONS. IND.
465	H=45mm & T=2.0mm	18	CHECKED BY	AMIR KHAN		
			APPROVED BY	NASSER ANANI	CLIENT: KENT GAD	
			DATE	22-07-2026		
			REF NO. :		SEC ITEM NO:	DWRG. NO. : REV. 01
			CONSULTANT :			SHEET NO. : SCALE:NTS


BONN GROUP OF COMPANIES
Cable Management Systems

NOTE:-


MATERIAL HDG 2mm HARDWARES SS316
Hot Dip Galvnaiztion 85 M without Epoxy

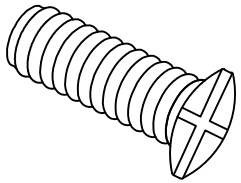


ROOFING BOLT
M8X30

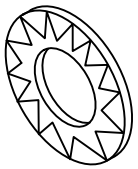

Washers M8

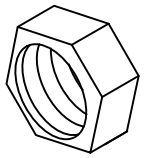

Nuts M8

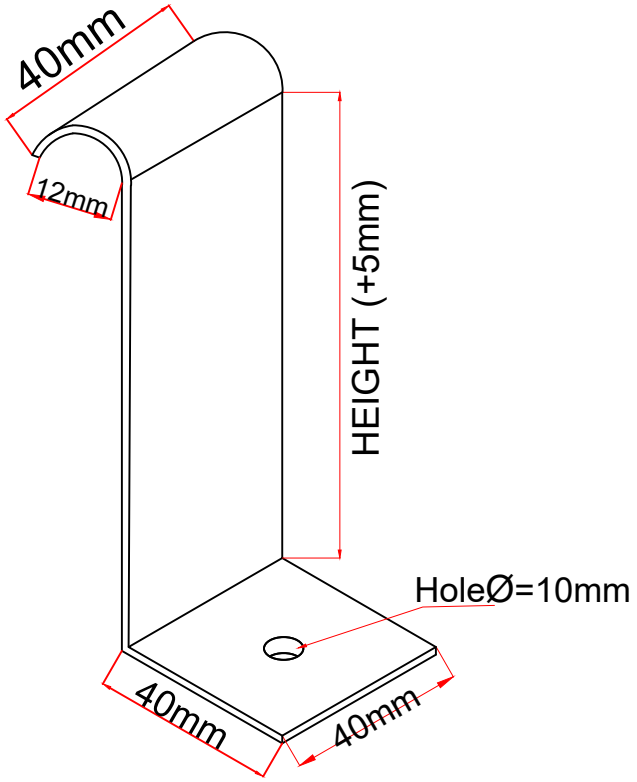

CABLE TRAY HOLD DOWN CLAMP

SN	DIMENSION TABLE	QTY
466	W=40mm, H =50+5mm , T = 2mm	354

DRAWN BY	EZELDIN
CHECKED BY	AMIR KHAN
APPROVED BY	NASSER ANANI
DATE	22-07-2026
REF NO. :	
CONSULTANT :	

TITLE:
CABLE LADDER HOLD DOWN CLAMP

CLIENT:
KENT GAD

SEC ITEM NO:

BONN METAL CONS. IND.

BONN GROUP OF COMPANIES
Cable Management Systems

DWRG. NO. :


REV.
01

SHEET NO. :

SCALE:NTS

NOTE:-

MATERIAL HDG 2mm HARDWARES SS316
Hot Dip Galvnaiztion 85 M without Epoxy

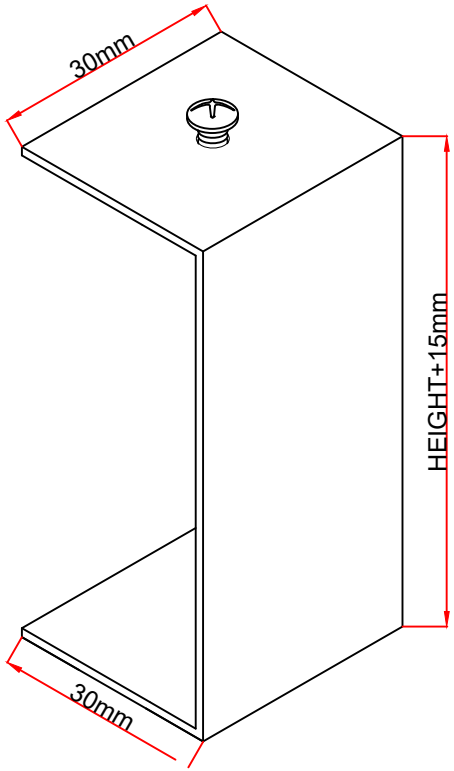

Cable Ladder cover Holding Clamps

SN	DIMENSION TABLE	QTY	DRAWN BY	EZELDIN	TITLE: Cable Ladder cover Holding Clamps	BONN METAL CONS. IND.
467	W=30mm, H =50+5mm , T = 2mm	648	CHECKED BY	AMIR KHAN		
	M6X20		APPROVED BY	NASSER ANANI	CLIENT: KENT GAD	
			DATE	22-07-2026		
			REF NO. :		SEC ITEM NO:	DWRG. NO. : REV. 01
			CONSULTANT :			SHEET NO. : SCALE:NTS

BONN GROUP OF COMPANIES
Cable Management Systems